
F13-SR-001
415V SAG MILL SWITCHROOM

F13-SW-002
SAG MILL 415V MOTOR CONTROL CENTRE

CONTINUED ON SHT 2
2000-F13-SLD-EL-10302

CONTINUED ON SHT 4
2000-F13-SLD-EL-10304

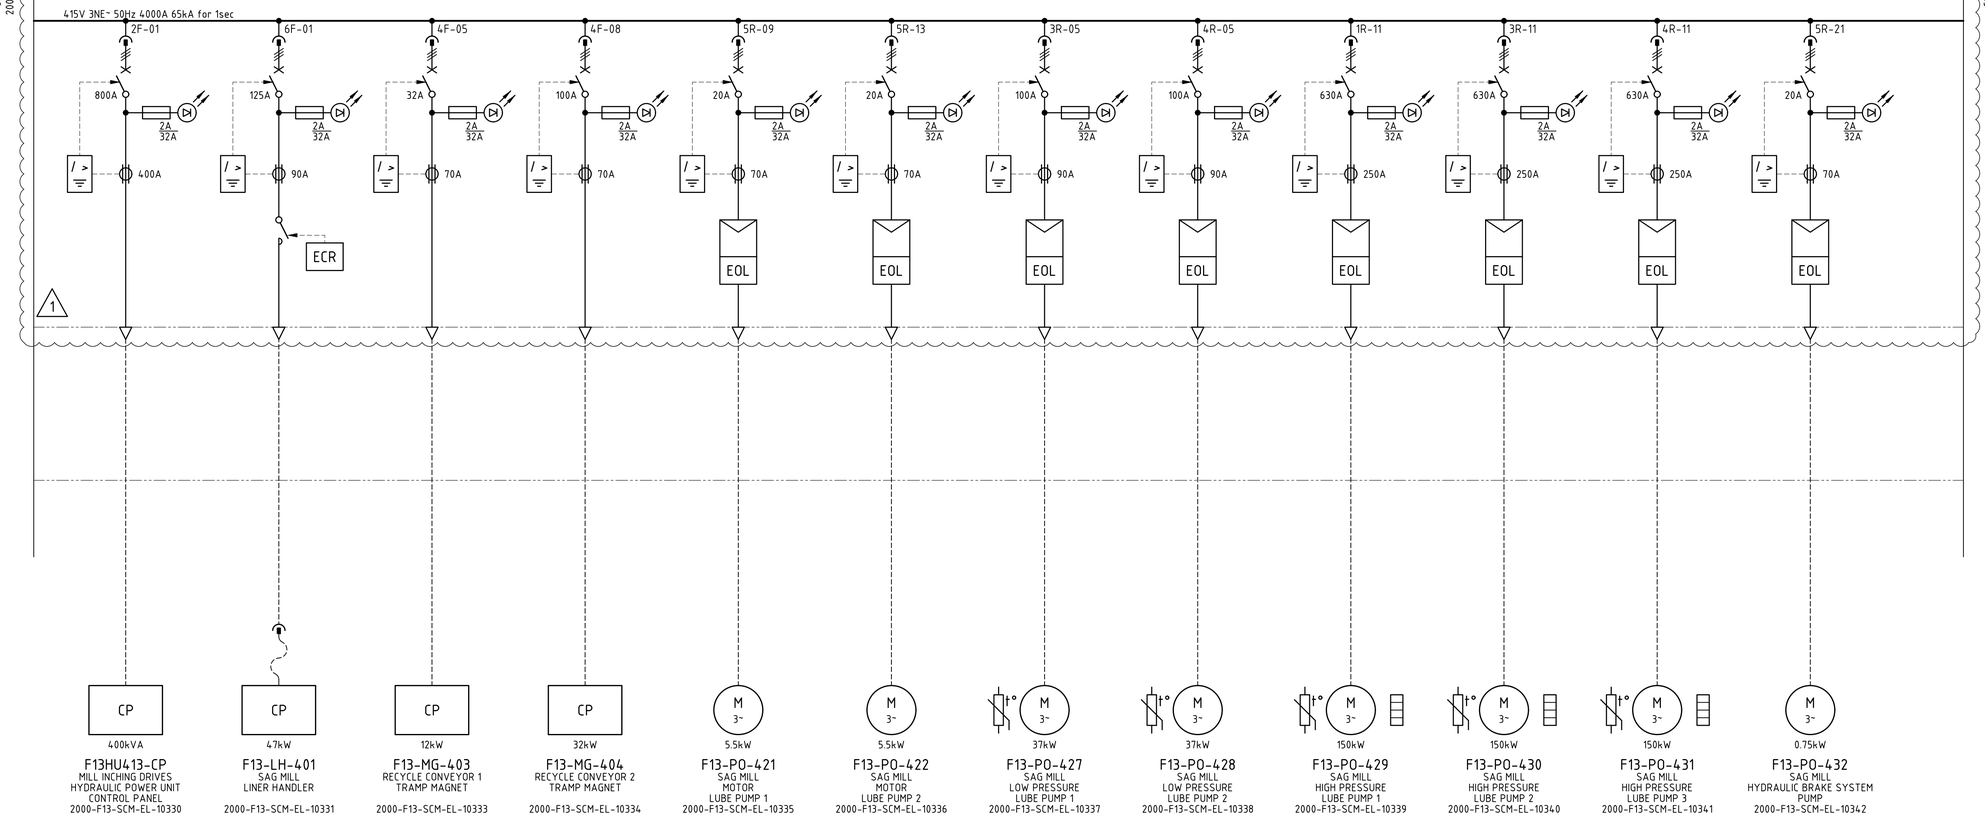

NOTES

1. REFER TO SHEET 1.

LEGEND

1. REFER TO SHEET 1.

Approved	X
Approved as Noted	
Not Approved	
For Information Only	

ACCEPTANCE DOES NOT RELIEVE THE SUPPLIER / CONTRACTOR OF ITS RESPONSIBILITY OR LIABILITIES UNDER THE PURCHASE ORDER / CONTRACT

2000-F13-SLD-EL-10303_Rev1

SAG mill F13-SW-002 415V MCC single line diagram sheet 3