
F13-SR-002
415V BALL MILL SWITCHROOM

F13-SW-003
BALL MILL 415V MOTOR CONTROL CENTRE

CONTINUED ON SHT 1
2000-F13-SLD-EL-10901

CONTINUED ON SHT 3
2000-F13-SLD-EL-10903

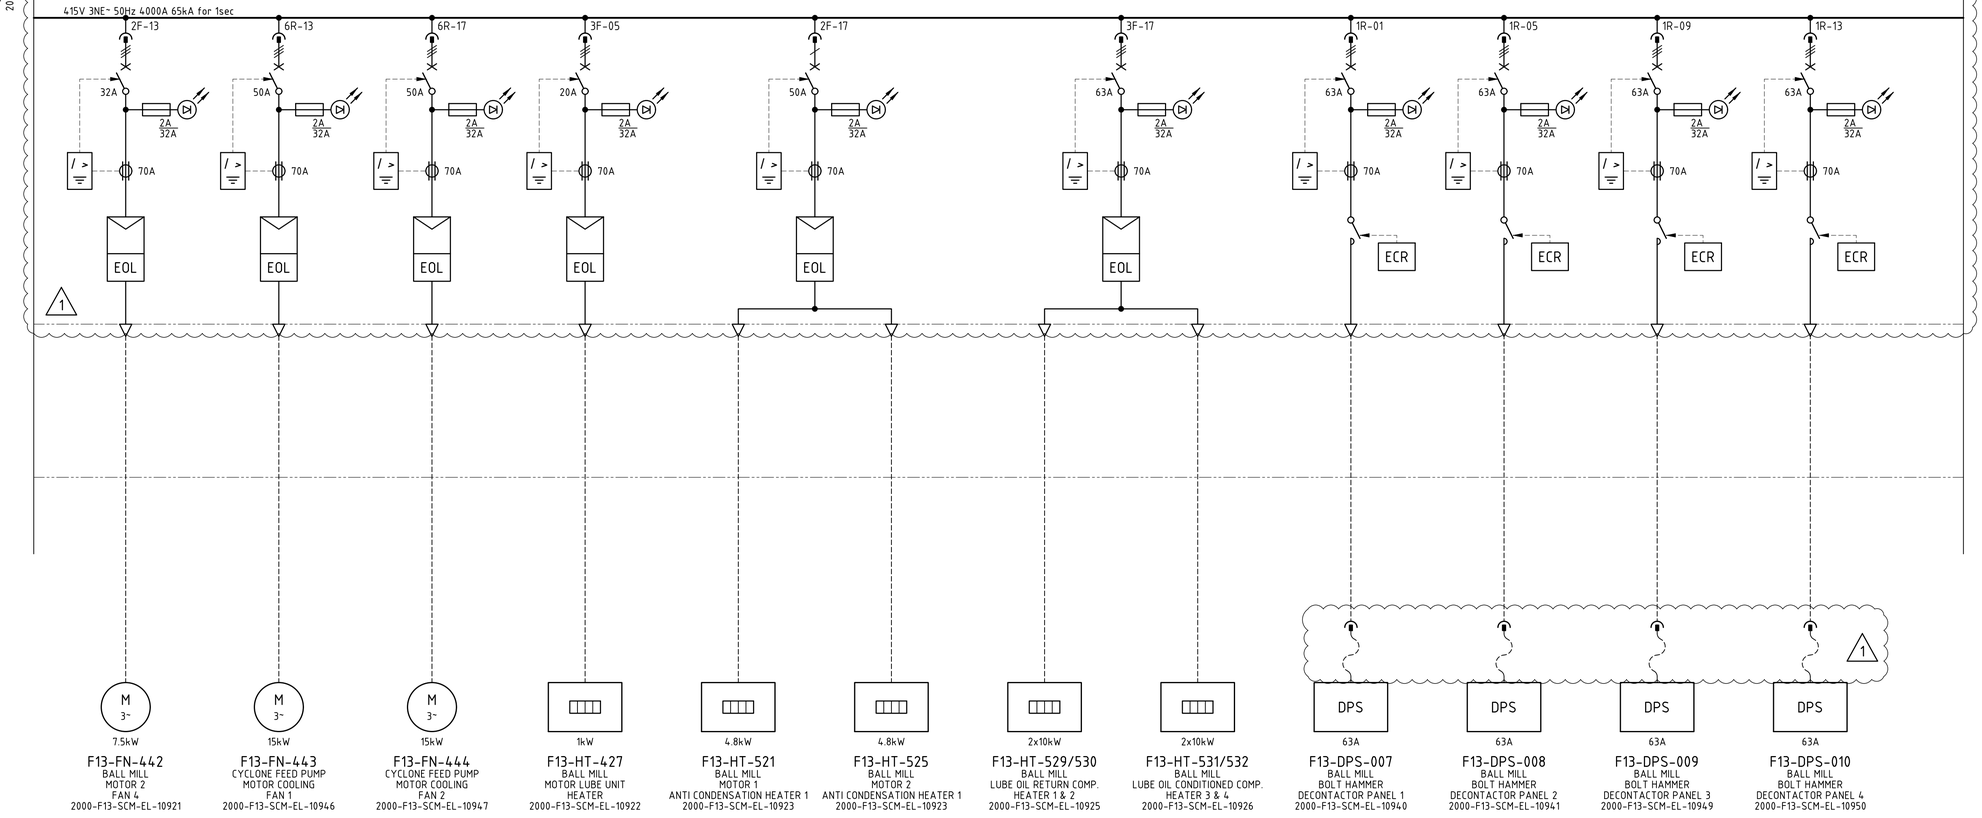

NOTES

1. REFER TO SHEET 1.

LEGEND

1. REFER TO SHEET 1.

Approved	[X]
Approved as Noted	[ ]
Not Approved	[ ]
For Information Only	

ACCEPTANCE DOES NOT RELIEVE THE SUPPLIER / CONTRACTOR OF ITS RESPONSIBILITY OR LIABILITIES UNDER THE PURCHASE ORDER / CONTRACT

2000-F13-SLD-EL-10902_Rev1

Ball mill F13-SW-003 415V MCC single line diagram sheet 2