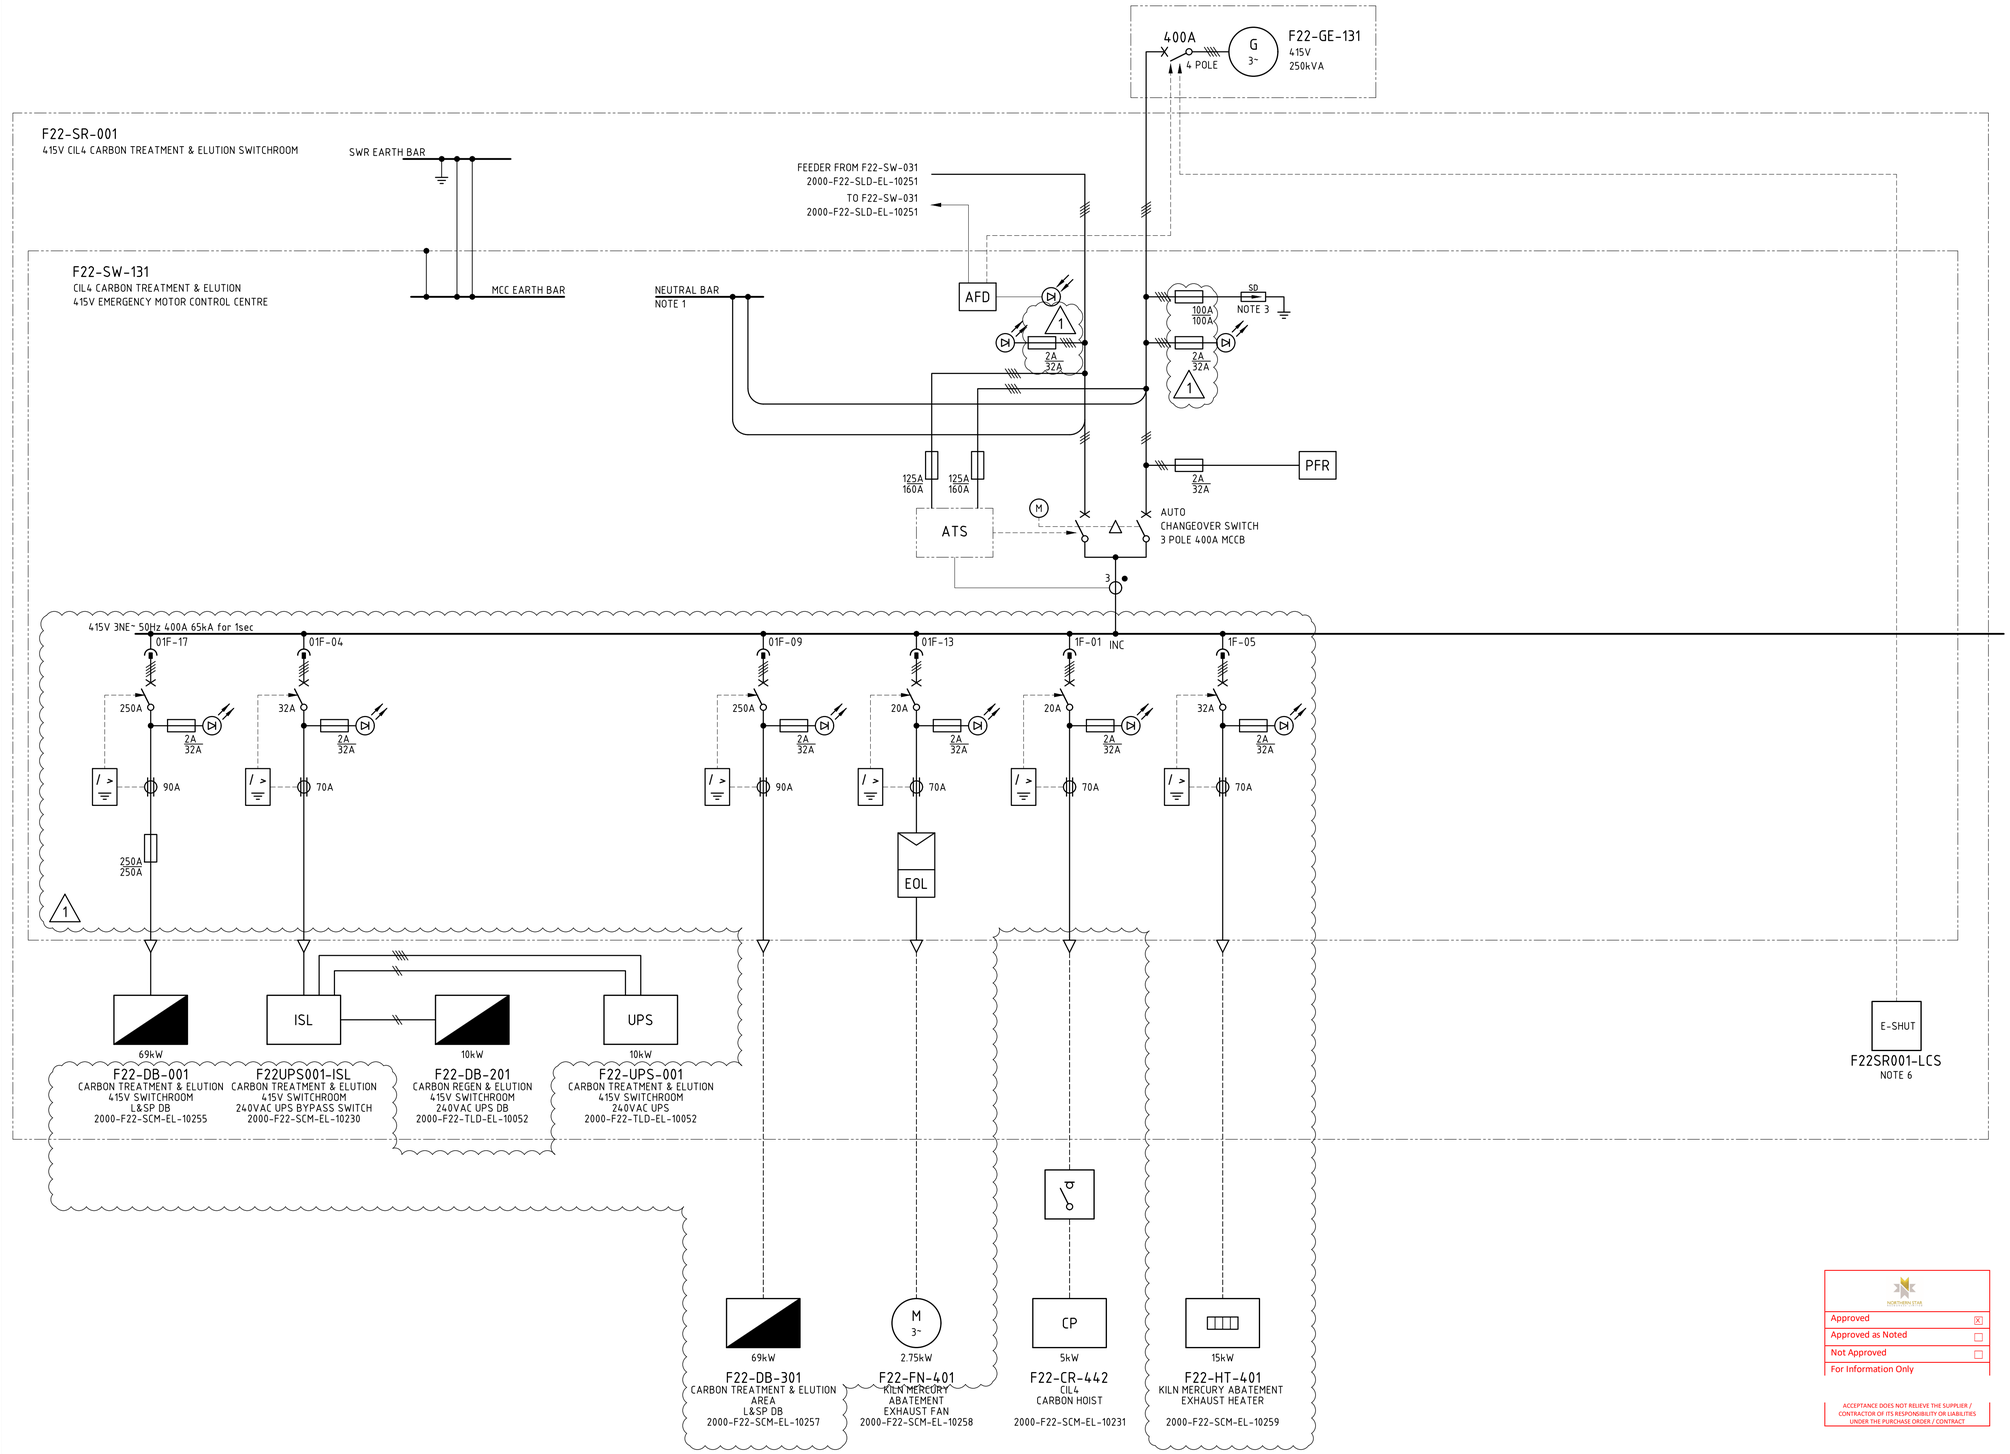



## NOTES

1. EARTH-NEUTRAL LINK INSTALLED IN UPSTREAM F22-SW-030 INCOMER TIER. SIGNAGE SHALL BE PLACED ON F22-SW-131 SWITCHBOARD AND ON GENERATOR READING "M.E.N. LINK LOCATED IN F22-SW-030 INCOMER TIER"
2. SWITCHBOARD SHALL BE EXTENSIBLE AND BE PROVIDED WITH THE FACILITY TO EXTEND THE MAIN BUSBAR AND APPEND ADDITIONAL TIERS AT ONE END WITHOUT MAJOR STRUCTURAL DISASSEMBLY.
3. SURGE DIVERTERS SHALL PROVIDE FEEDBACK TO DCS VIA VOLT-FREE CONTACTS. SURGE DIVERTER FUSES SHALL BE SIZED BY VENDOR TO SUIT DUTY.
4. MINIATURE CIRCUIT BREAKERS SHALL BE SIZED AND RATED TO SUIT ACB AND INCOMER REQUIREMENTS.
5. CIRCUIT BREAKER TO BE SUBSTITUED FOR FUSED-SWITCH WHERE REQUIRED BY EQUIPMENT MANUFACTURERS GUIDELINES.
6. EMERGENCY SHUTDOWN (E-SHUT) PUSH BUTTON WIRED TO SHUNT TRIP NOMINATED CIRCUIT BREAKERS.
7. SWITCHBOARD VENDOR SHALL SELECT SWITCHGEAR TO PROVIDE TYPE-2 CO-ORDINATION SUITABLE FOR HIGH EFFICIENCY MOTORS.
8. ALL DRIVE I/O VIA COMMS NETWORK TO DCS. FOR COMMUNICATIONS BLOCK DIAGRAM REFER 2000-F22-BLK-IC-10001.

## LEGEND

| | |
|---|---|
| PFR | PHASE FAILURE RELAY |
| / > | EARTH LEAKAGE RELAY |
| xxxA / xxxA | ST TRIP SET POINT / CB SIZE |
| AFD | ARC FLASH DETECTION |
| ECR | EARTH CONTINUITY RELAY |
| E-SHUT | SWITCHROOM EMERGENCY SHUTDOWN |
| | DIRECT ON-LINE MOTOR STARTER GENERIC - NOTE 7,8 |
| EOL | ELECTRONIC OVERLOAD UNIT NOTE 7,8 |

| | |
|---|---|
| Approved | ☒ |
| Approved as Noted | ☐ |
| Not Approved | ☐ |
| For Information Only | |

ACCEPTANCE DOES NOT RELIEVE THE SUPPLIER / CONTRACTOR OF ITS RESPONSIBILITY OR LIABILITIES UNDER THE PURCHASE ORDER / CONTRACT

# 2000-F22-SLD-EL-10261_Rev1

CIL4 carbon treatment & elution F22-SW-131 415V emergency MCC single line diagram