
F23PP467-VS
VARIABLE SPEED DRIVE
SYSTEM INTERCONNECTION DIAGRAM DRG. No. 2000-EL005-B02-10002

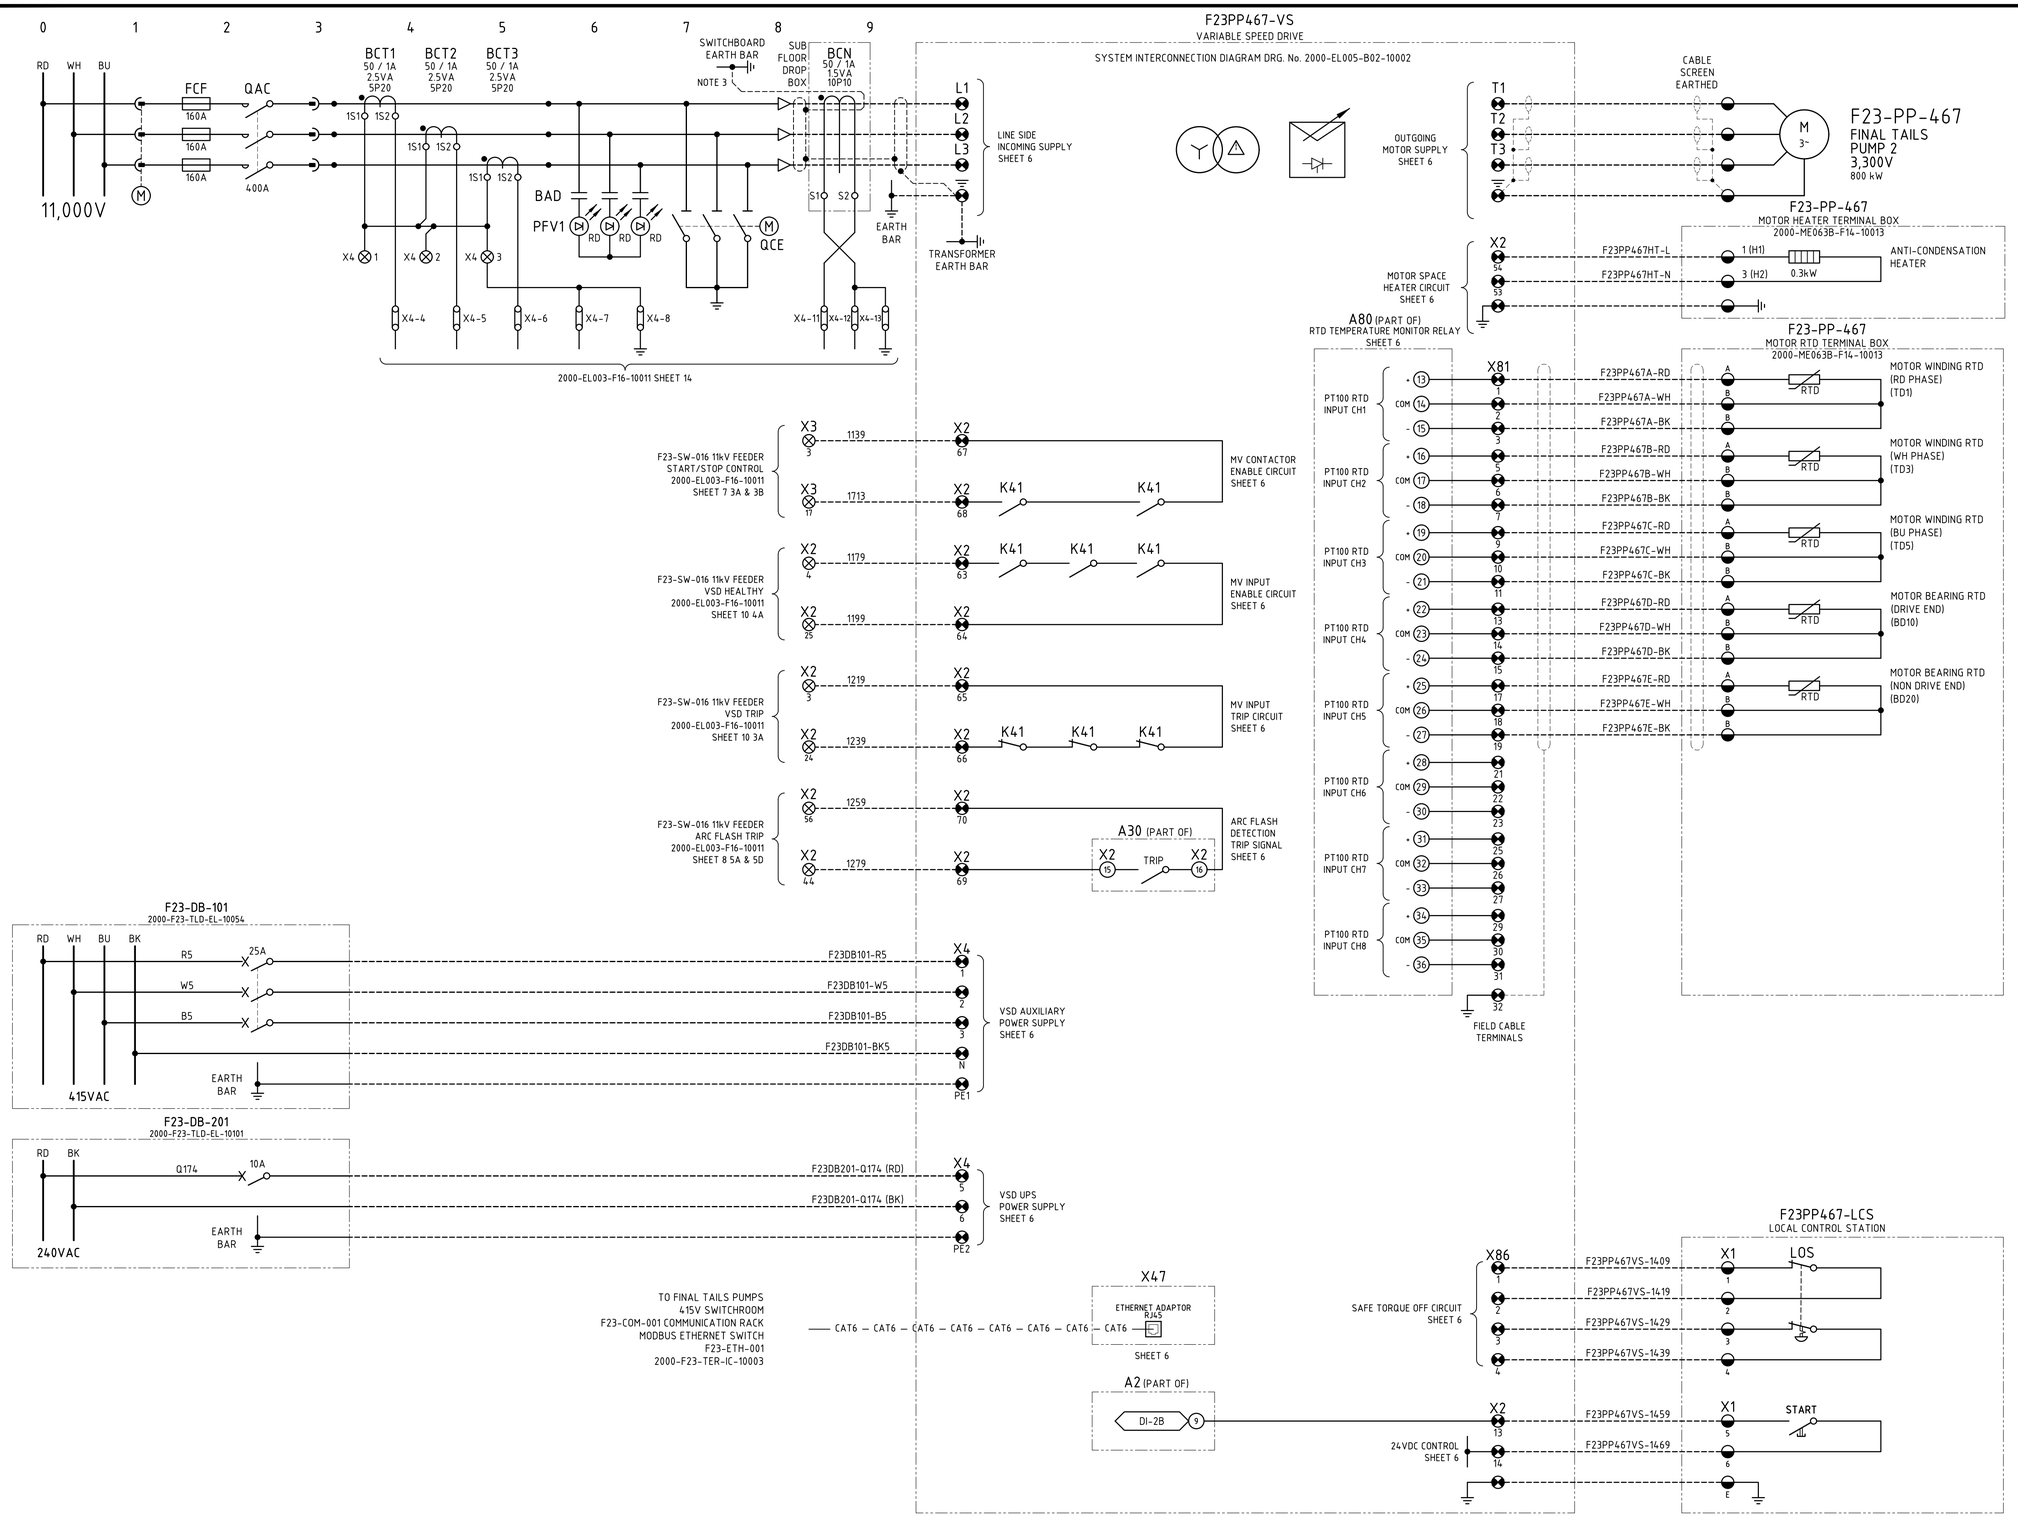

NOTES

1. WIRE NUMBER FERRULES ON TERMINAL STRIP SHALL BE PREFIXED WITH EQUIPMENT NUMBER e.g. F23PP467-1200, UNLESS OTHERWISE NOTED.
2. EACH WIRE SHALL BE IDENTIFIED AT BOTH ENDS WITH FERRULES.
3. IF THE CABLE SCREENS PASS THROUGH CORE BALANCE CT BEFORE BREAKING OUT THEN THE SCREEN EARTHS MUST BE BOUGHT BACK THROUGH THE CORE BALANCE CT AND TERMINATED TO EARTH.

LEGEND

- ⊗ 11kV SWITCHBOARD TERMINAL
- ⊗ VSD TERMINAL
- ◒ FIELD TERMINAL
- ◑ DCS OR I/O TERMINAL
- ◨ MARSHALLING TERMINAL
- (x) DEVICE TERMINAL

PANEL A03

2000-F23-SCM-EL-10105_Rev1

F23-SW-016 - F23-PP-467 final tails pump 2 VSD feeder - schematic diagram