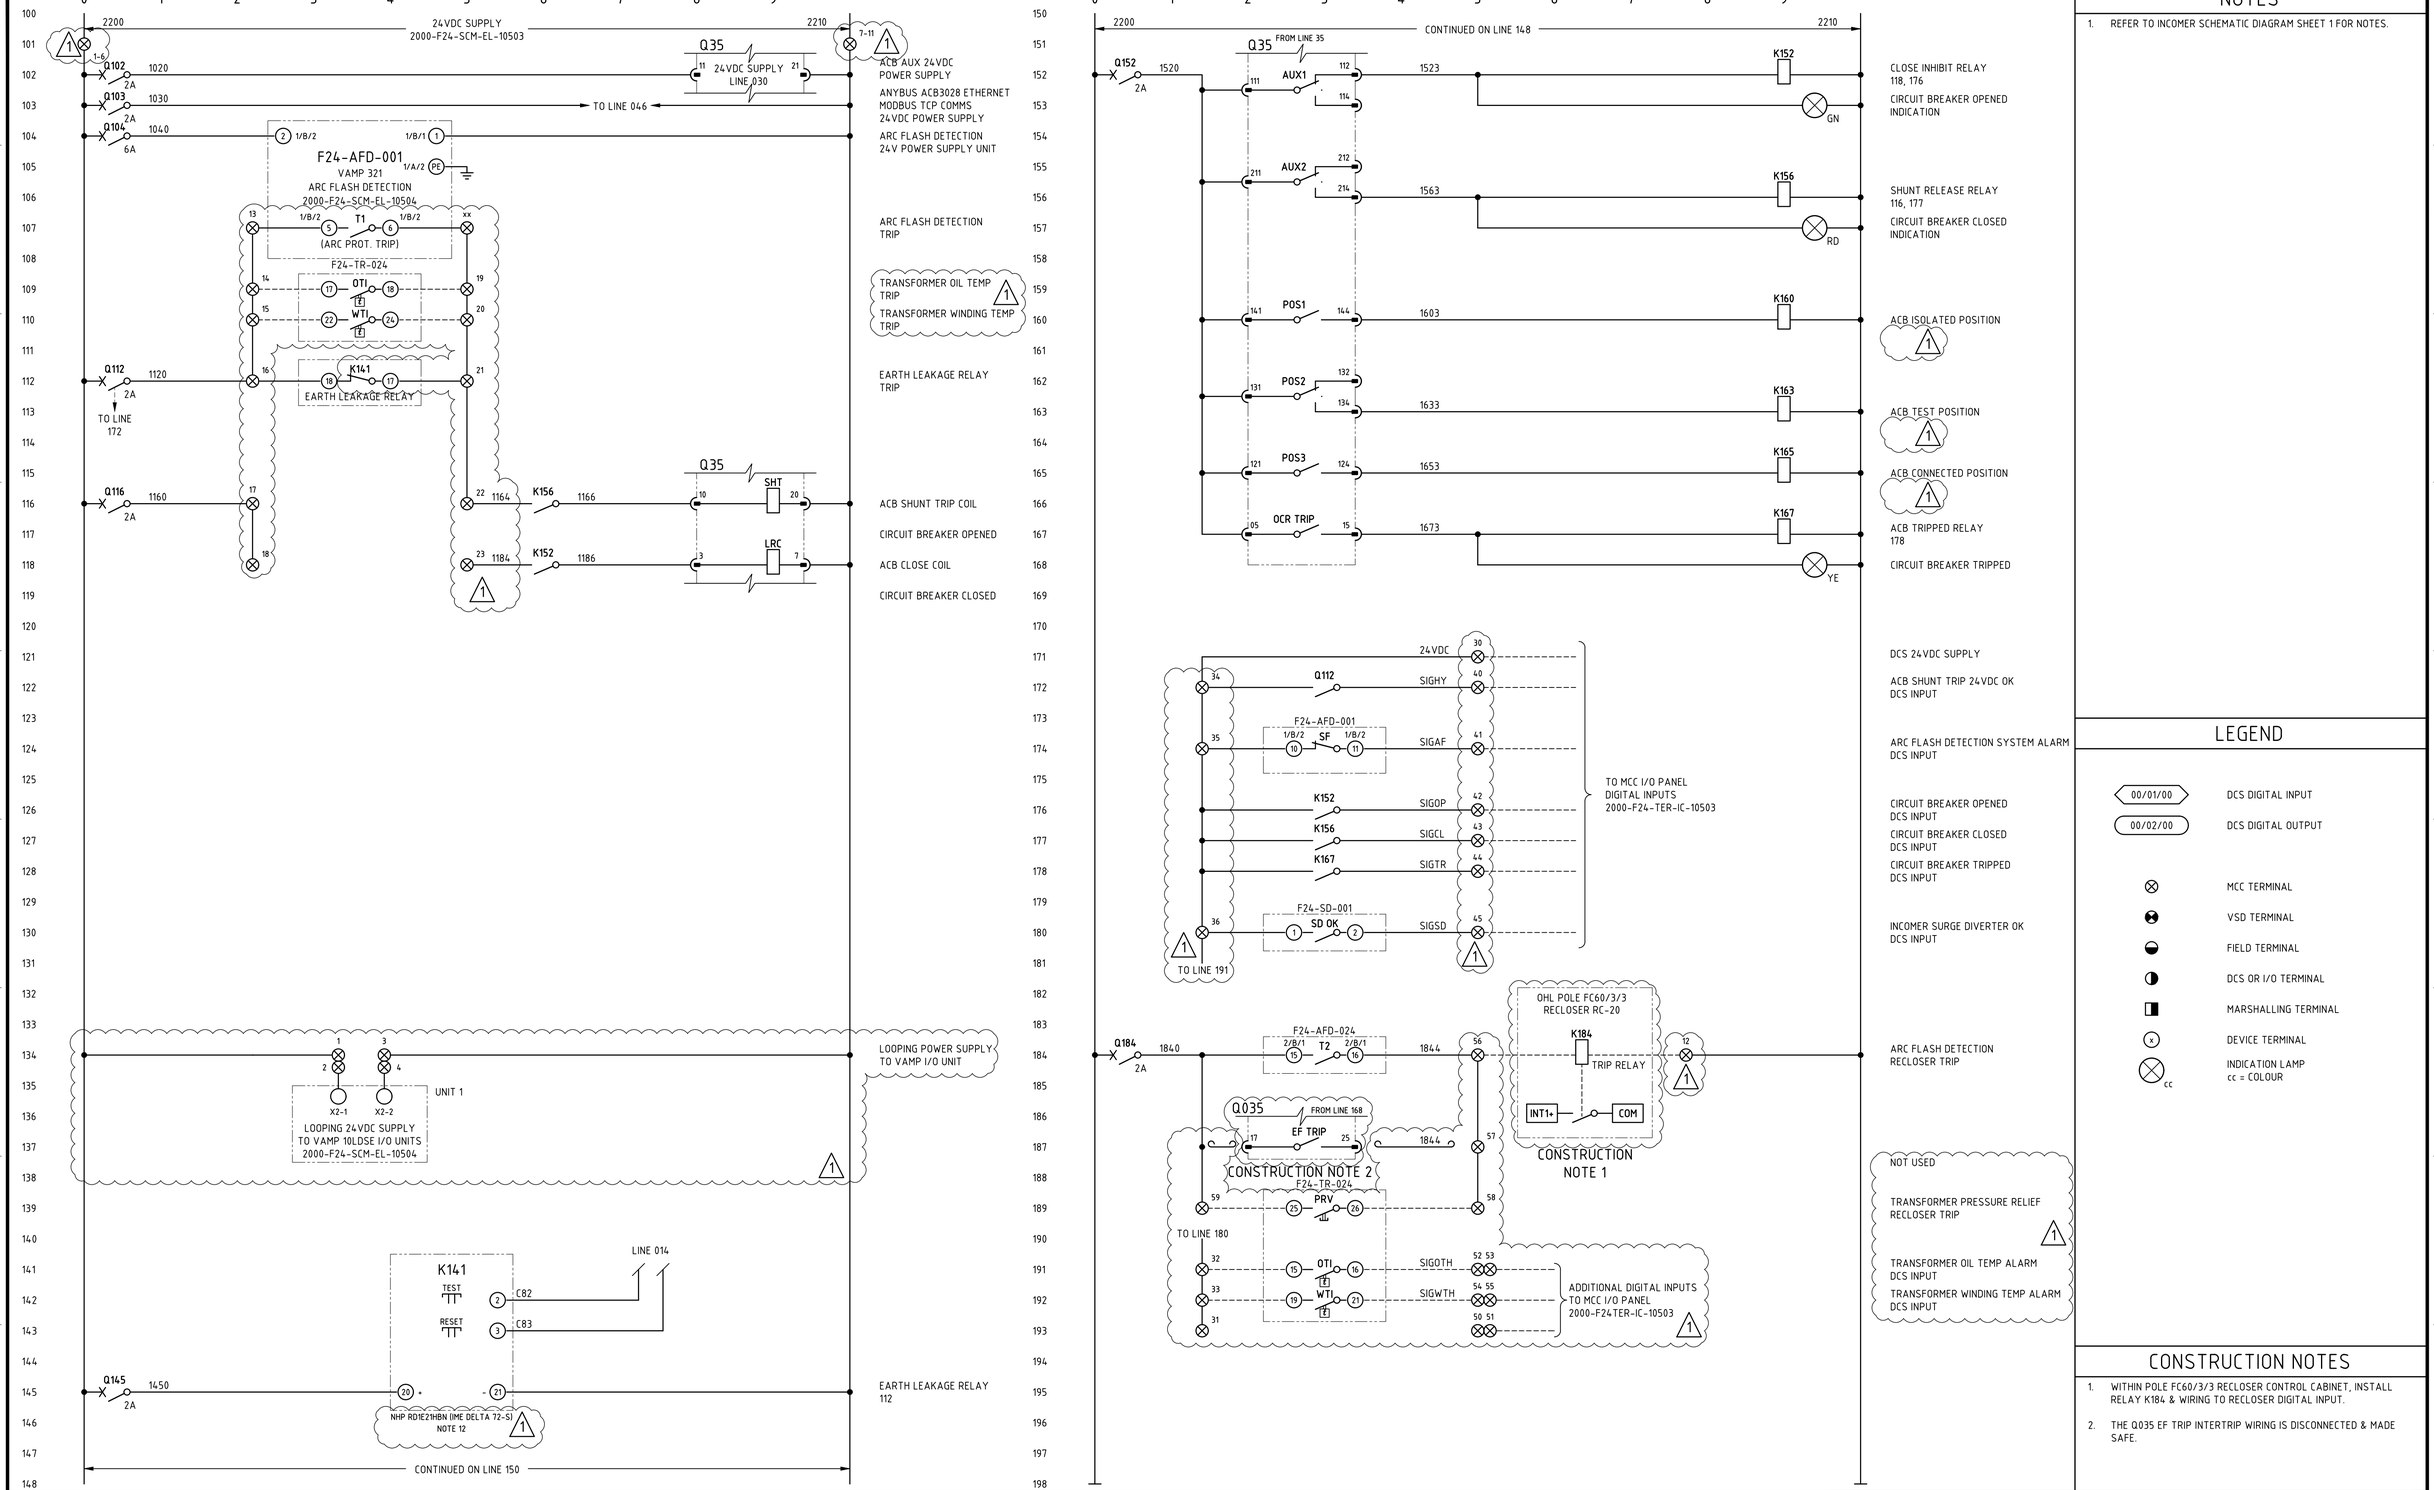


NOTES

1. REFER TO INCOMER SCHEMATIC DIAGRAM SHEET 1 FOR NOTES.

LEGEND

- 00/01/00 — DCS DIGITAL INPUT
- 00/02/00 — DCS DIGITAL OUTPUT
- MCC TERMINAL
- VSD TERMINAL
- FIELD TERMINAL
- DCS OR I/O TERMINAL
- MARSHALLING TERMINAL
- DEVICE TERMINAL
- INDICATION LAMP (cc = COLOUR)

CONSTRUCTION NOTES

1. WITHIN POLE FC60/3/3 RECLOSER CONTROL CABINET, INSTALL RELAY K184 & WIRING TO RECLOSER DIGITAL INPUT.
2. THE Q035 EF TRIP INTERTRIP WIRING IS DISCONNECTED & MADE SAFE.

2000-F24-SCM-EL-10502_Rev1

F24-SW-024 F24-SW-024 incomer schematic diagram sheet 2