
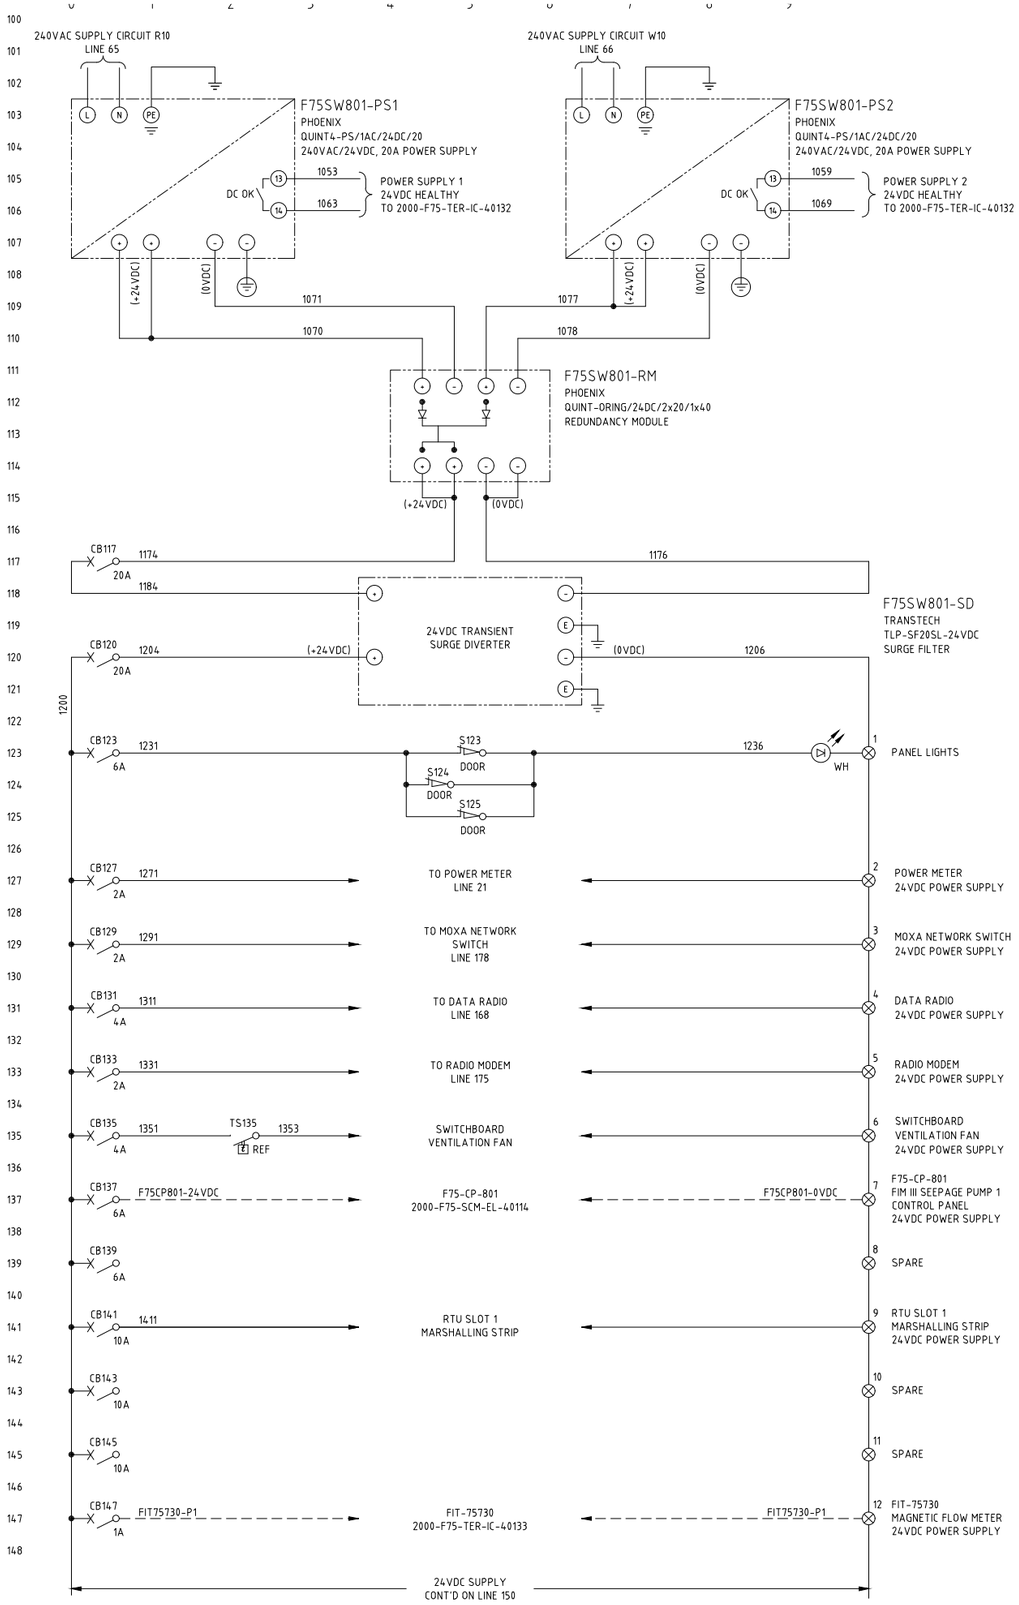


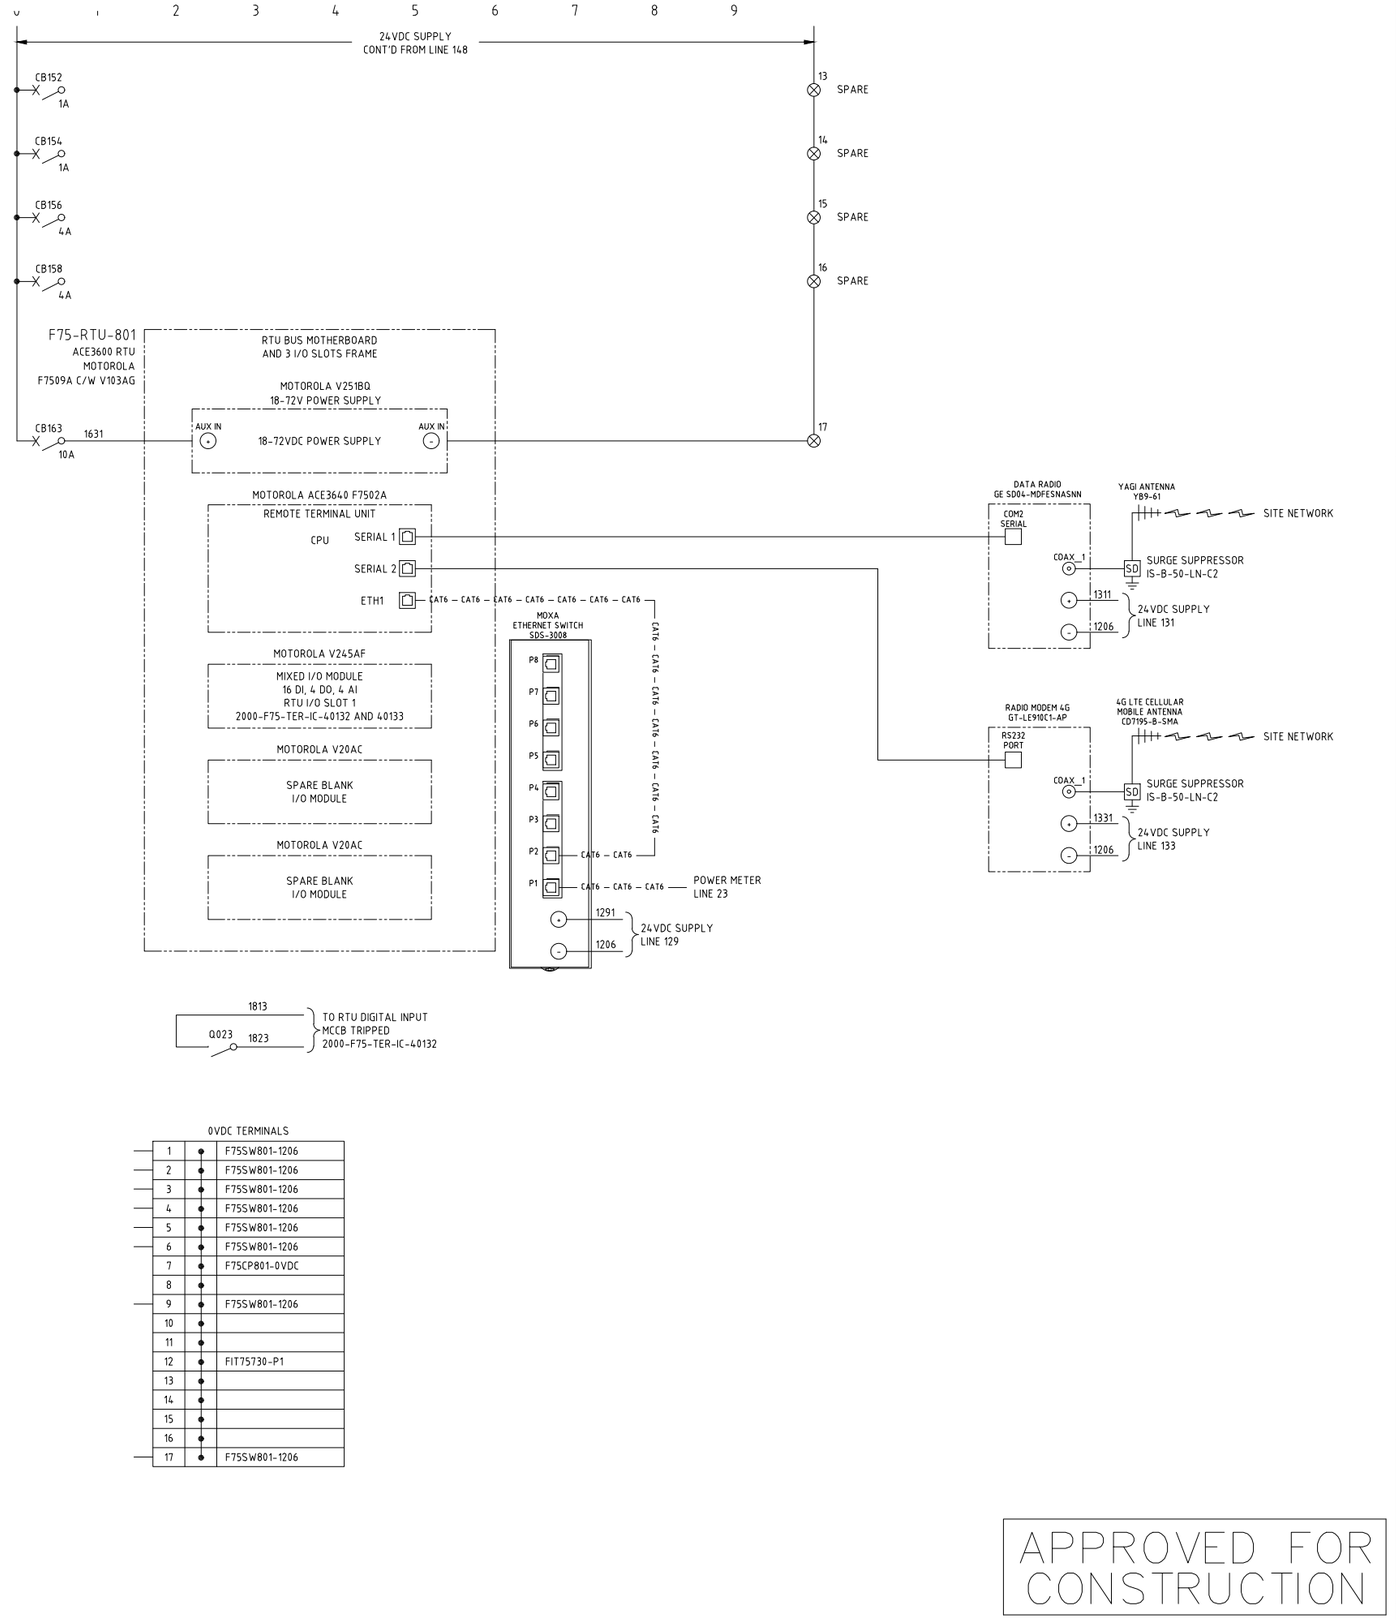

0VDC TERMINALS

1	•	F75SW801-1206
2	•	F75SW801-1206
3	•	F75SW801-1206
4	•	F75SW801-1206
5	•	F75SW801-1206
6	•	F75SW801-1206
7	•	F75CP801-0VDC
8	•	
9	•	F75SW801-1206
10	•	
11	•	
12	•	FIT75730-P1
13	•	
14	•	
15	•	
16	•	
17	•	F75SW801-1206

APPROVED FOR CONSTRUCTION

2000-F75-SCM-EL-40123_Rev0

FIM III tailings dam F75-SW-801 FIM III TSF switchboard 3 schematic diagram sheet 2