


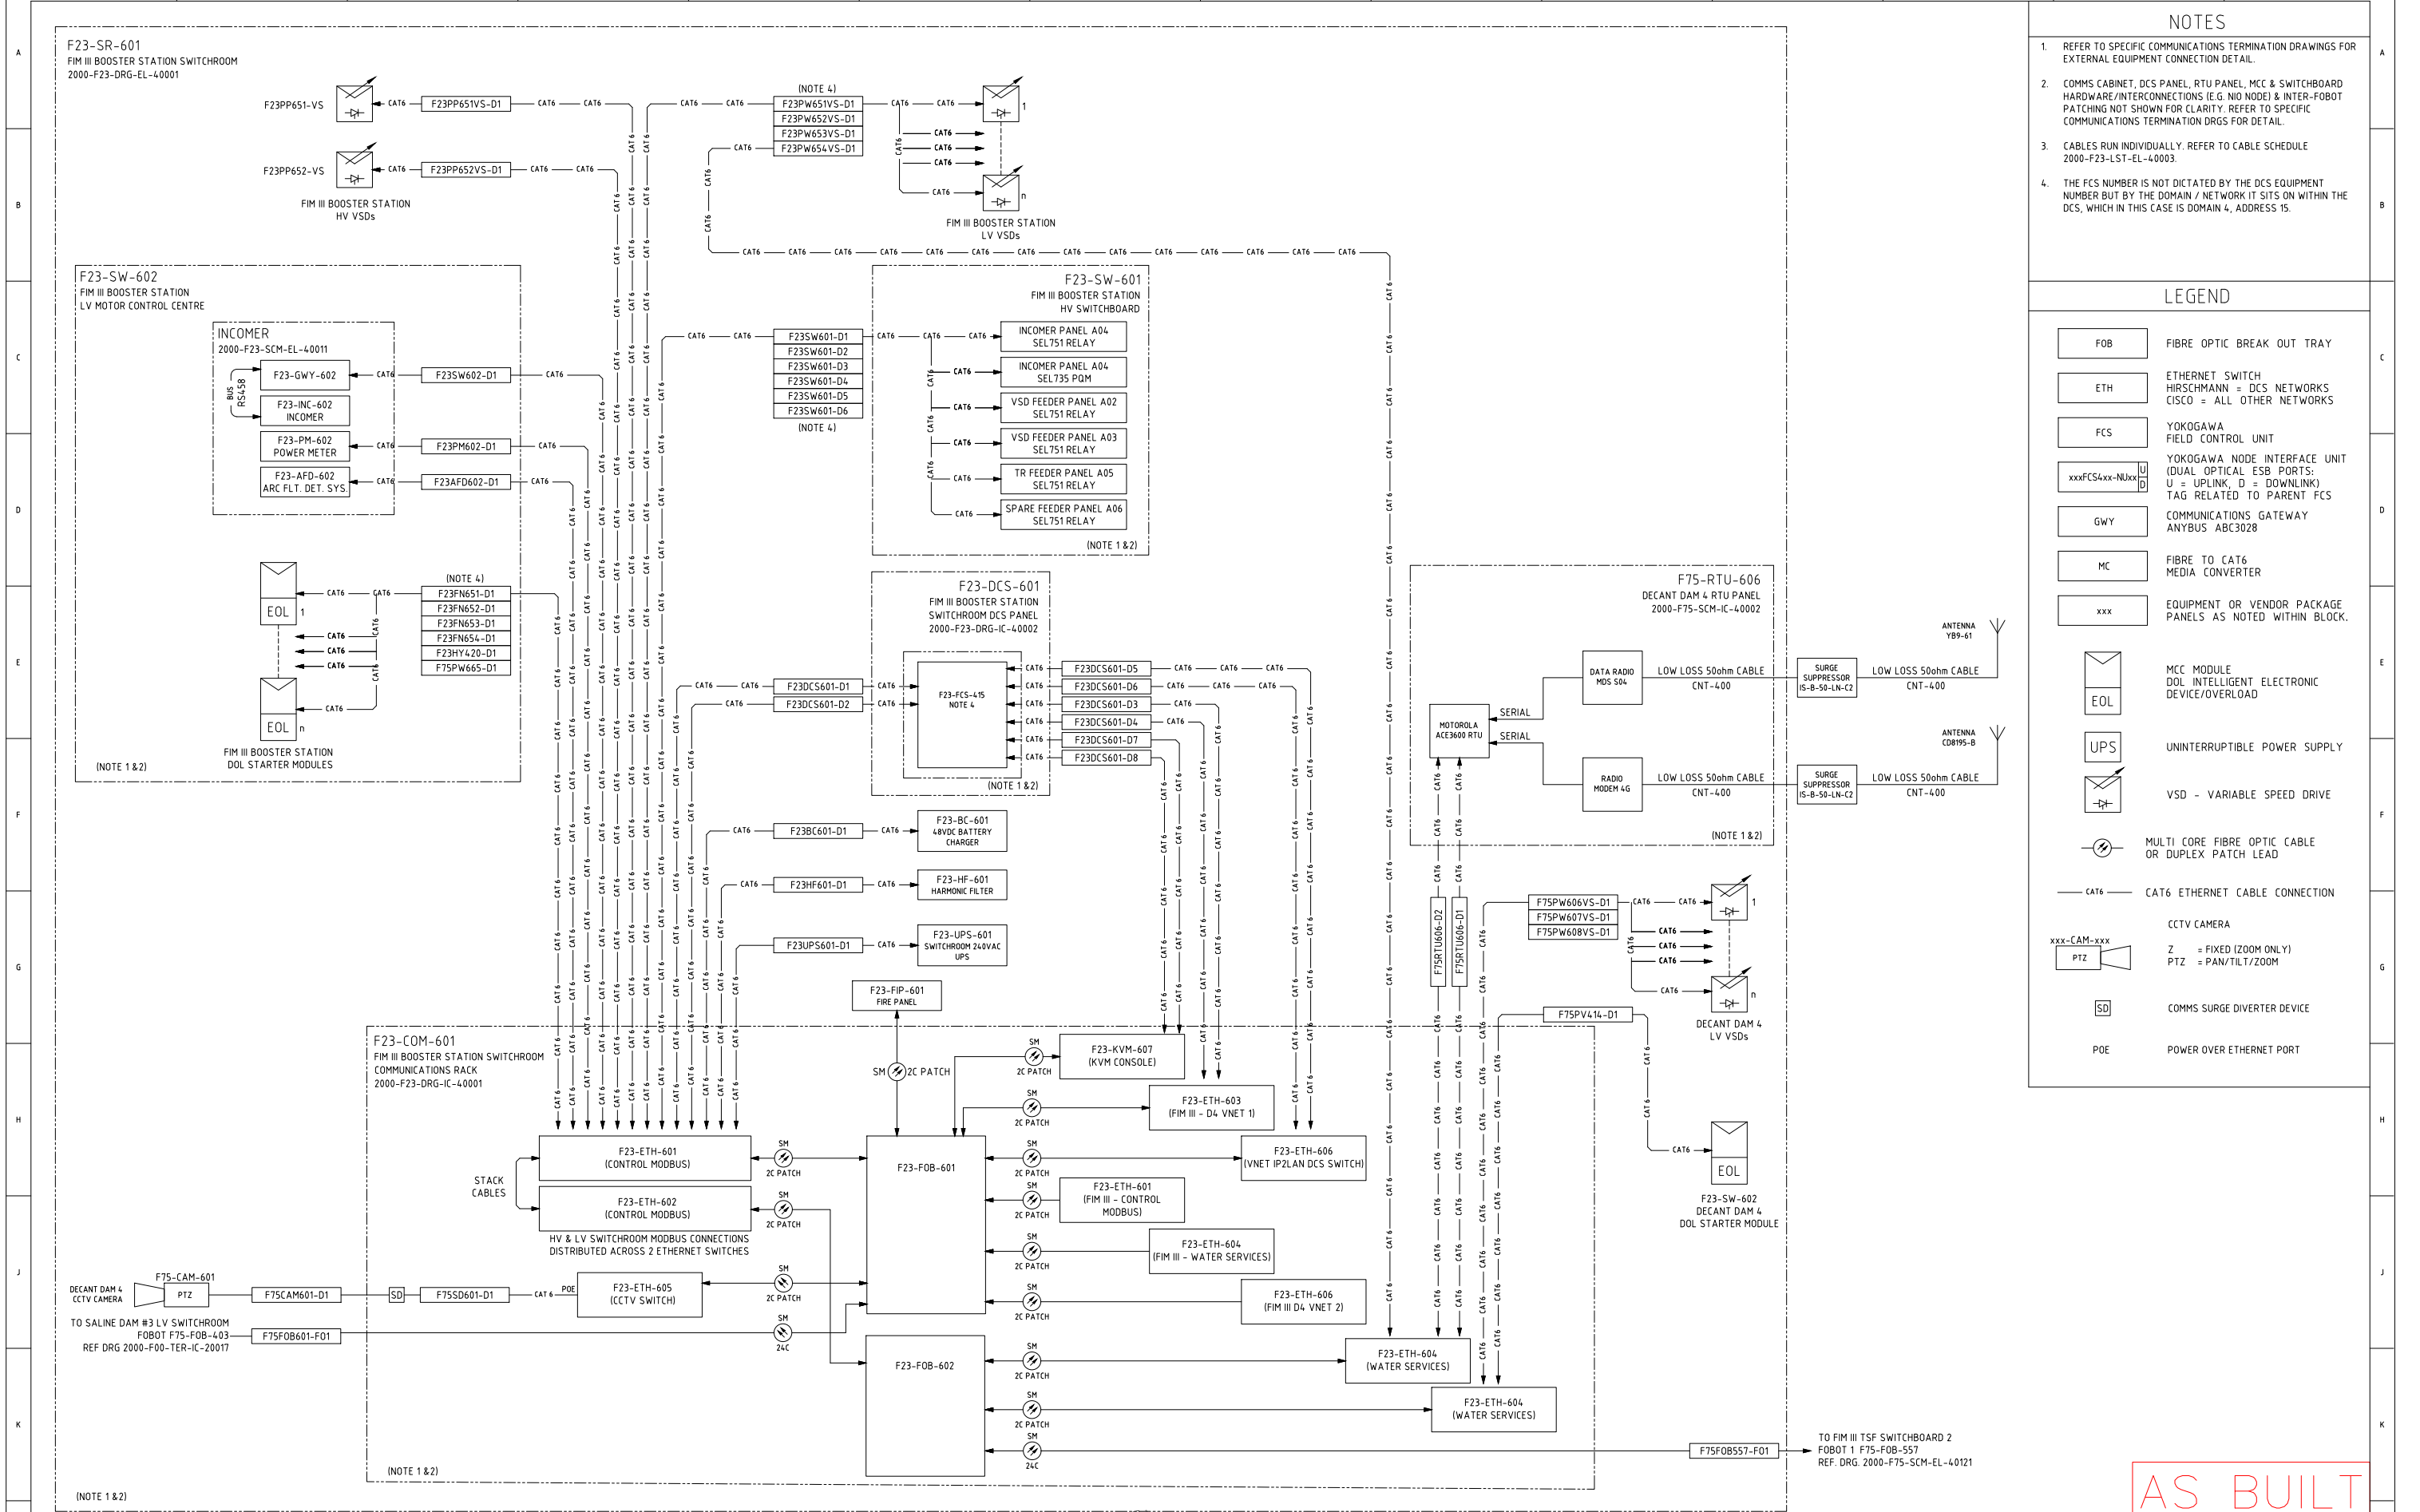

				6 13.MAR.26 AS FOR III TSF		ME JA MC MB		 NORTHERN STAR RESOURCES LIMITED  DRA PACIFIC (PTY) LIMITED		J. 06.DEC.2024		PROJECT: KCGM FIM TSF PROJECT			
				5 11.DEC.25 RE-APPROVED FOR CONSTRUCTION		ET MC KV TH				C. 06.DEC.2024					
				4 11.NOV.25 RE-APPROVED FOR CONSTRUCTION		MT				J. 06.DEC.2024		TITLE: FIM III BOOSTER STATION F23-SR-601 SWITCHROOM COMMUNICATIONS BLOCK DIAGRAM			
				3 09.OCT.25 RE-APPROVED FOR CONSTRUCTION		E				K. 14.APR.2025					
				2 08.AUG.25 RE-APPROVED FOR CONSTRUCTION		KVN				T. 21.MAY.2025		SCALE			
				1 10.JUL.25 RE-APPROVED FOR CONSTRUCTION		TECH APP				CLIENT APP		A 1			
GENERAL NOTES AND STANDARD DRAWINGS INDEX				2000-F00-STD-EL-10001		O 21.MAY.25 APP FOR CONSTRUCTION				NTS		DRG No. 2000-F23-BLK-IC-40001		REV 6	
REFERENCES				DWG No		REVISION									
1		2		3		4		5		6		7		8	
10		11		12		13		14							