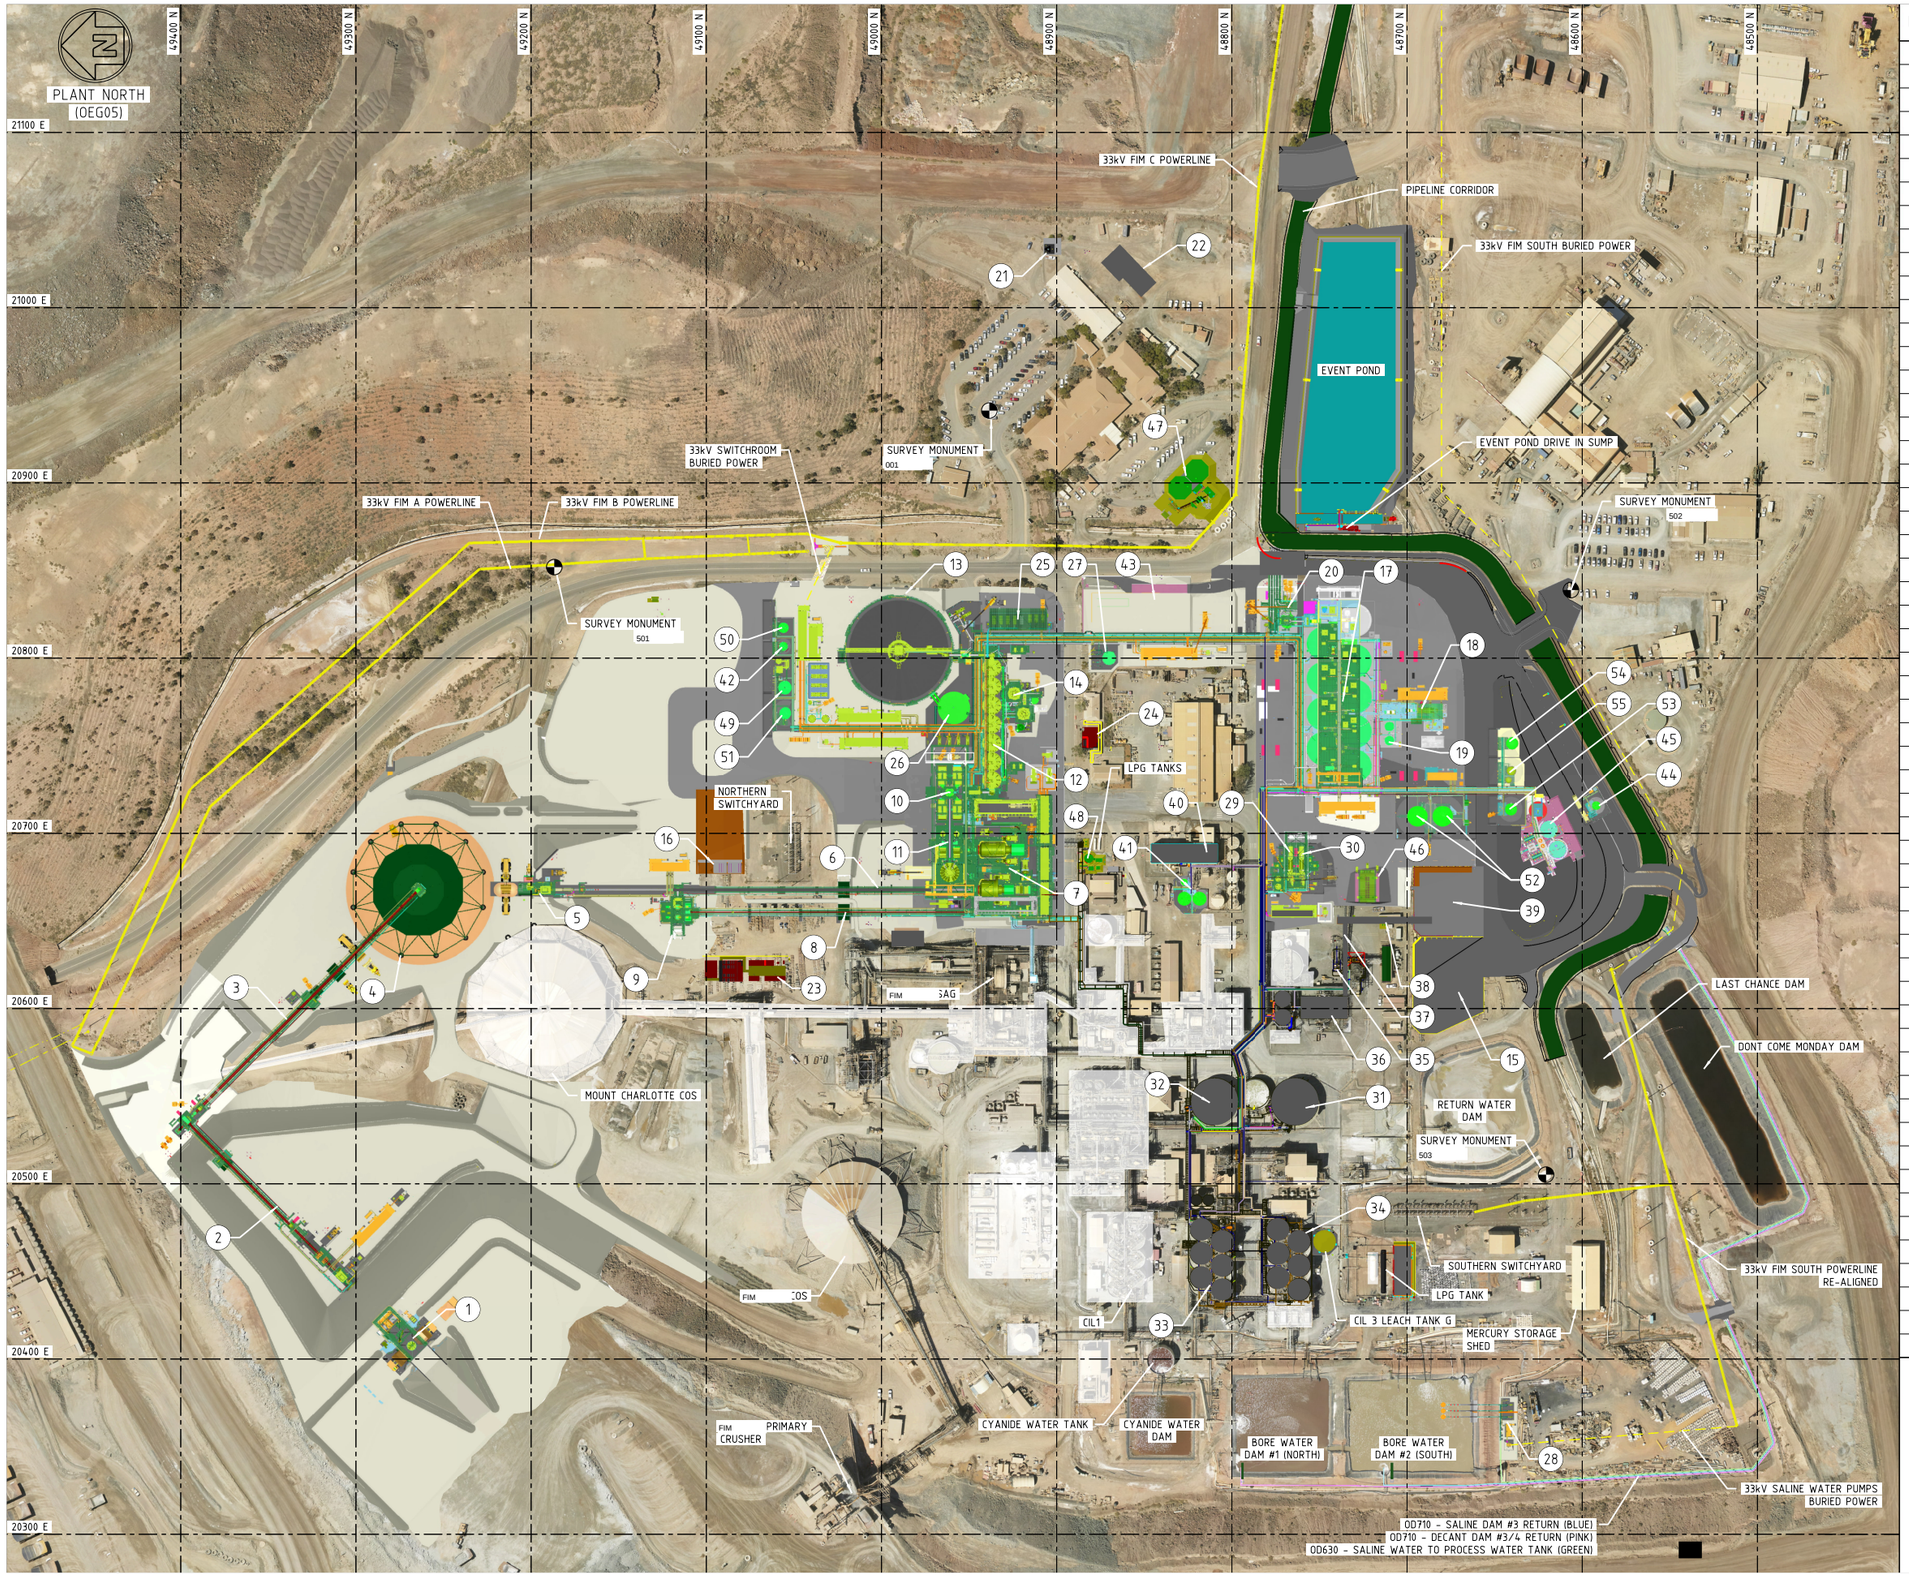

ITEM	AREA	DESCRIPTION
1	F12	PRIMARY CRUSHING
2	F12	CV-401 - PRIMARY CRUSHING DISCHARGE CONVEYOR
3	F12	CV-402 - STOCKPILE FEED CONVEYOR
4	F12	CRUSHED ORE STOCKPILE
5	F13	STOCKPILE RECLAIM
6	F13	CV-403 - SAG MILL FEED CONVEYOR
7	F13	MILLING AND CLASSIFICATION
8	F13	CV-405 RECYCLE CRUSHING FEED CONVEYOR 2
9	F13	RECYCLE CRUSHING
10	F13	TRASH SCREENING
11	F14	GRAVITY CIRCUIT AND INTENSIVE LEACHING
12	F16	ROUGHER AND SCAVENGER FLOTATION
13	F17	FLOTATION TAILINGS PRE-LEACH THICKENING
14	F18	CLEANER AND CLEANER SCAVENGER FLOTATION
15	F35	CONCENTRATE HANDLING AND FILTRATION - EXTENSION UNLOADING PAD
16	F19	MILLING & CLASSIFICATION - BALL BUNKER
17	F21	FLOTATION TAILINGS CIL 4 (STAGE 2)
18	F22	CIL4 - CARBON TREATMENT (STAGE 2)
19	F22	CIL4 - ELUTION (STAGE 2)
20	F23	FINAL TAILINGS HANDLING AND STORAGE
21	N00	NON-PROCESS INFRASTRUCTURE - TELSTRA TOWER
22	N00	NON-PROCESS INFRASTRUCTURE - SITE SERVICES WORKSHOP
23	N03	ON-SITE INFRASTRUCTURE - PLANT SHUTDOWN CRIB ROOM
24	N03	ON-SITE INFRASTRUCTURE - PLANT PRE-START ROOM
25	F24	AIR AND WATER SERVICES - AIR COMPRESSORS AND FLOTATION BLOWERS
26	F24	AIR AND WATER SERVICES - PROCESS WATER
27	F24	AIR AND WATER SERVICES - RAW WATER
28	F24	AIR AND WATER SERVICES - SALINE WATER PUMPS
29	F28	ULTRA FINE GRINDING 2
30	F28	ULTRA FINE GRINDING 3 (STAGE 2)
31	F30	CONCENTRATE THICKENING (F30-TH-61)
32	F30	CONCENTRATE PRE-LEACH THICKENING (F30-TH-31) (STAGE 2)
33	F30	CIL 2 - EXISTING
34	F30	CIL 3 - EXISTING
35	F34	ULTRA FINE GRINDING 1 - EXISTING
36	F35	CONCENTRATE HANDLING AND FILTRATION
37	F35	CONCENTRATE HANDLING AND FILTRATION - CV17
38	F35	CONCENTRATE HANDLING AND FILTRATION - CV18
39	F35	CONCENTRATE HANDLING AND FILTRATION - UNLOADING PAD
40	F66	ELECTROWINNING AND GOLDROOM
41	F66	GRAVITY AND CIL4 ELUATE CIRCULATION TANK AREA
42	F72	REAGENTS - FROTHER (STAGE 1)
43	F72	REAGENTS - OXYGEN PLANT (STAGE 2)
44	F72	REAGENTS - HYDROGEN PEROXIDE (STAGE 1)
45	F72	REAGENTS - LIME SLAKING (STAGE 2)
46	F72	REAGENTS - GRINDING MEDIA AND ANTI-SCALANT STORAGE
47	F75	WATER SERVICES - FIRE WATER & SCHEME WATER
48	F75	WATER SERVICES - POTABLE WATER
49	F72	REAGENTS - FLOCCULANT (STAGE 1)
50	F72	REAGENTS - COPPER SULPHATE (STAGE 1)
51	F72	REAGENTS - PAX (STAGE 1)
52	F72	REAGENTS - CYANIDE (STAGE 2)
53	F72	REAGENTS - CAUSTIC (STAGE 2)
54	F72	REAGENTS - LEAD NITRATE (STAGE 2)
55	F72	REAGENTS - HYDROCHLORIC ACID (STAGE 2)

NOTES

1. FADE[illegible] AREA OF PROCESS PLANT REPRESENTS PROCESS EQUIPMENT MADE