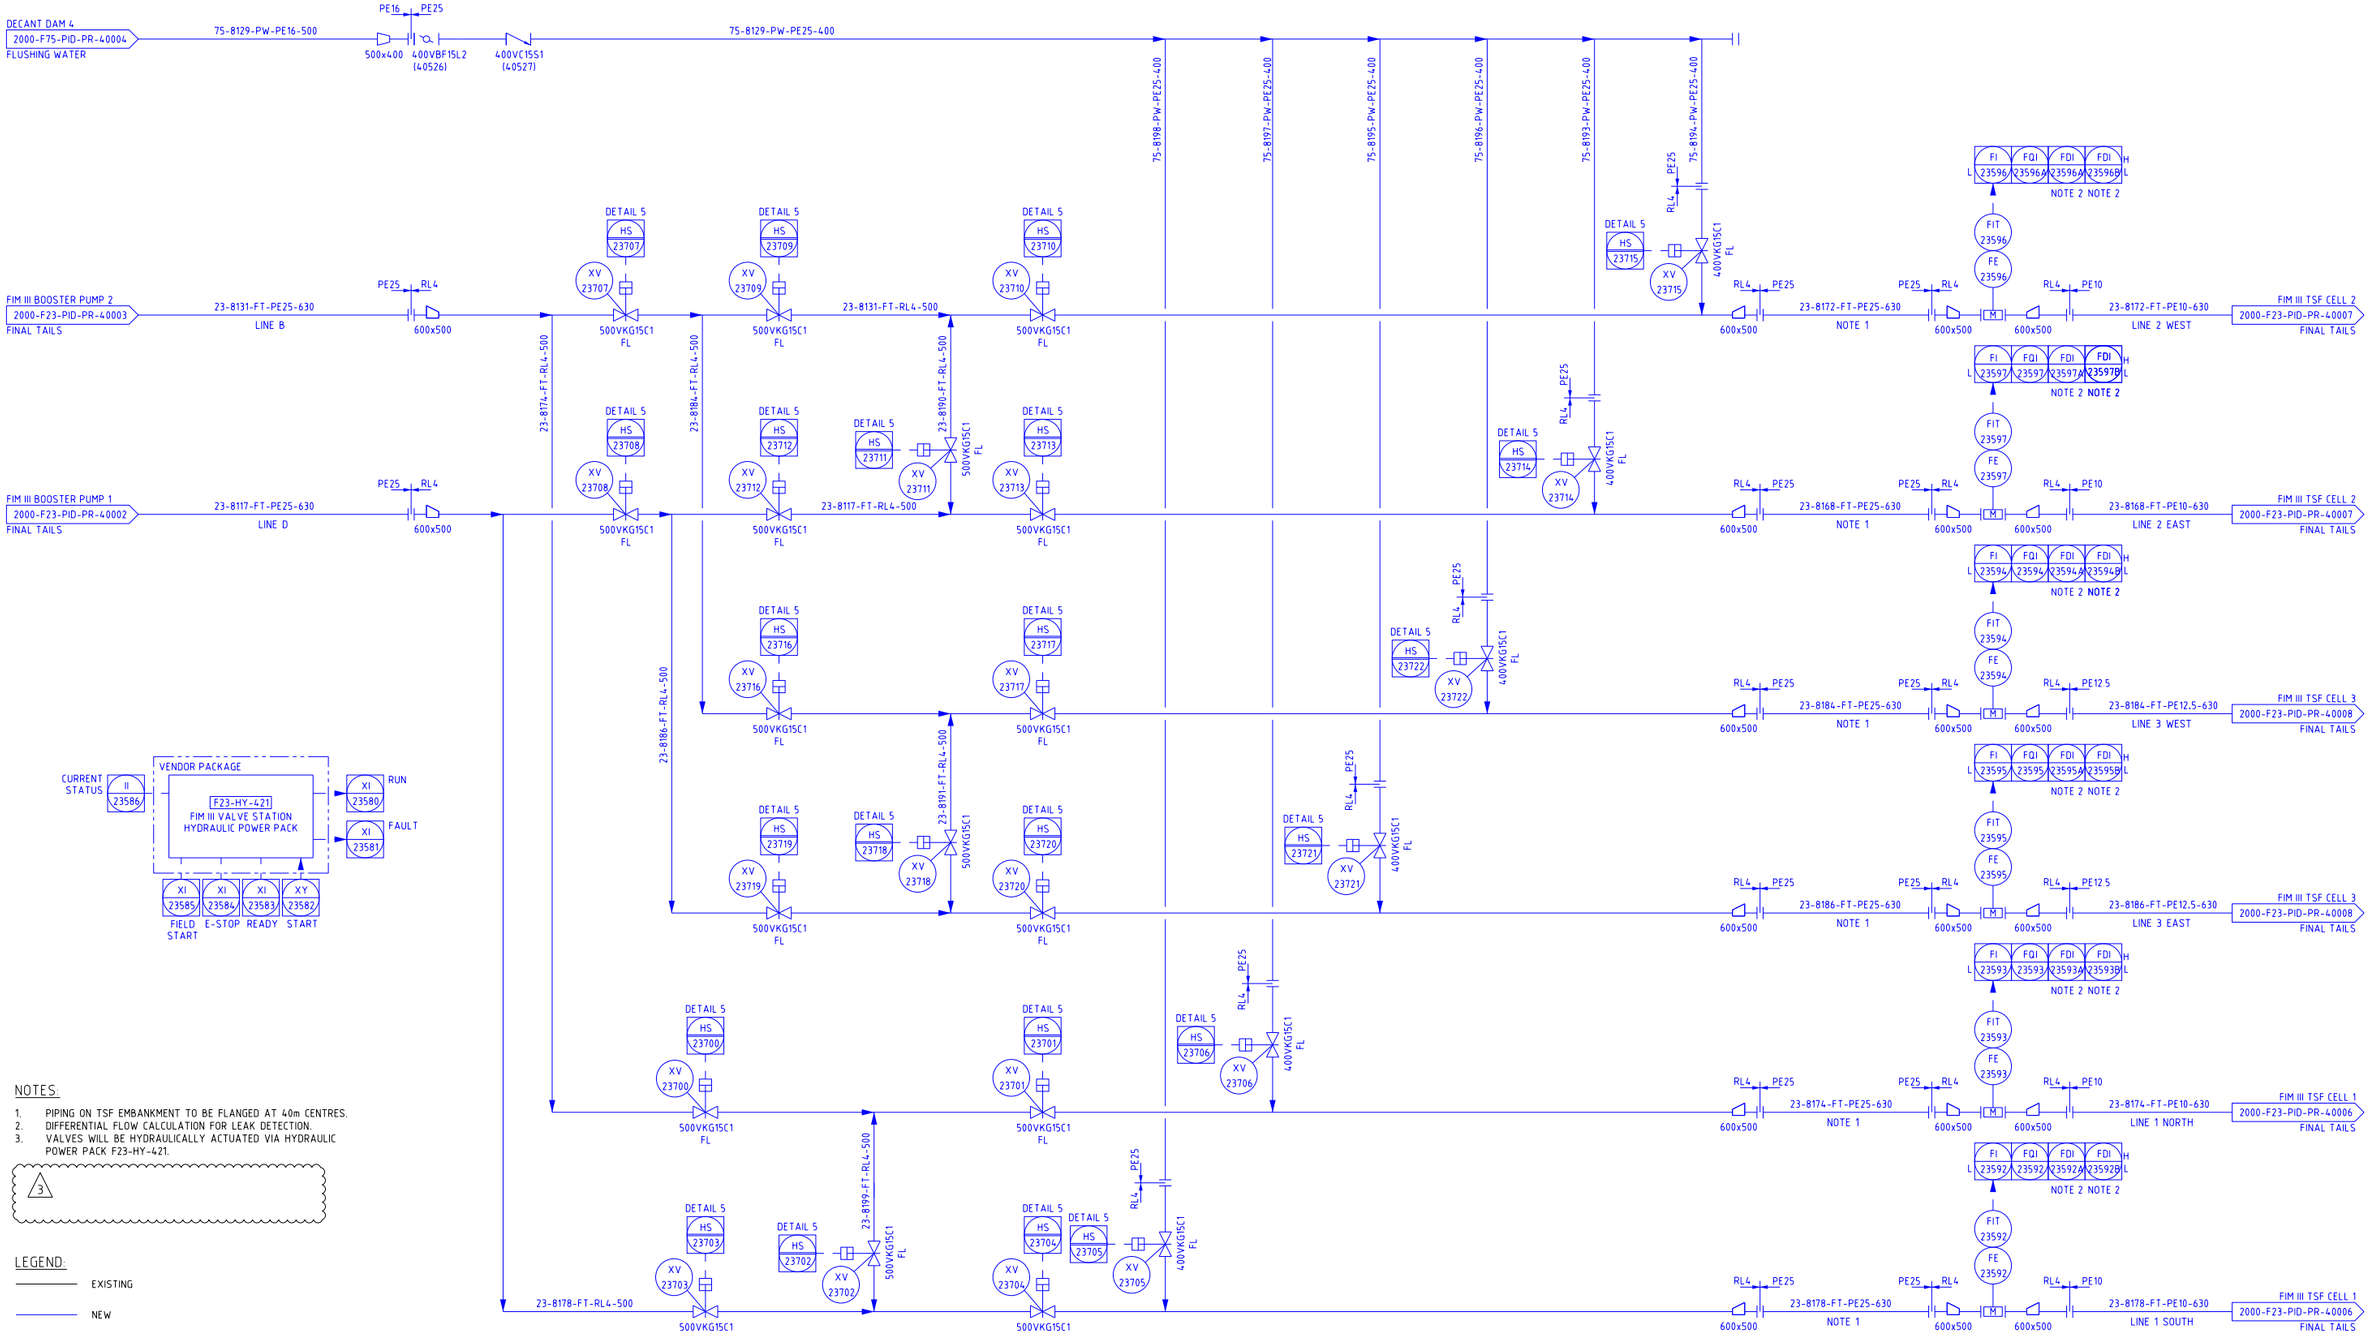


APPROVED FOR CONSTRUCTION