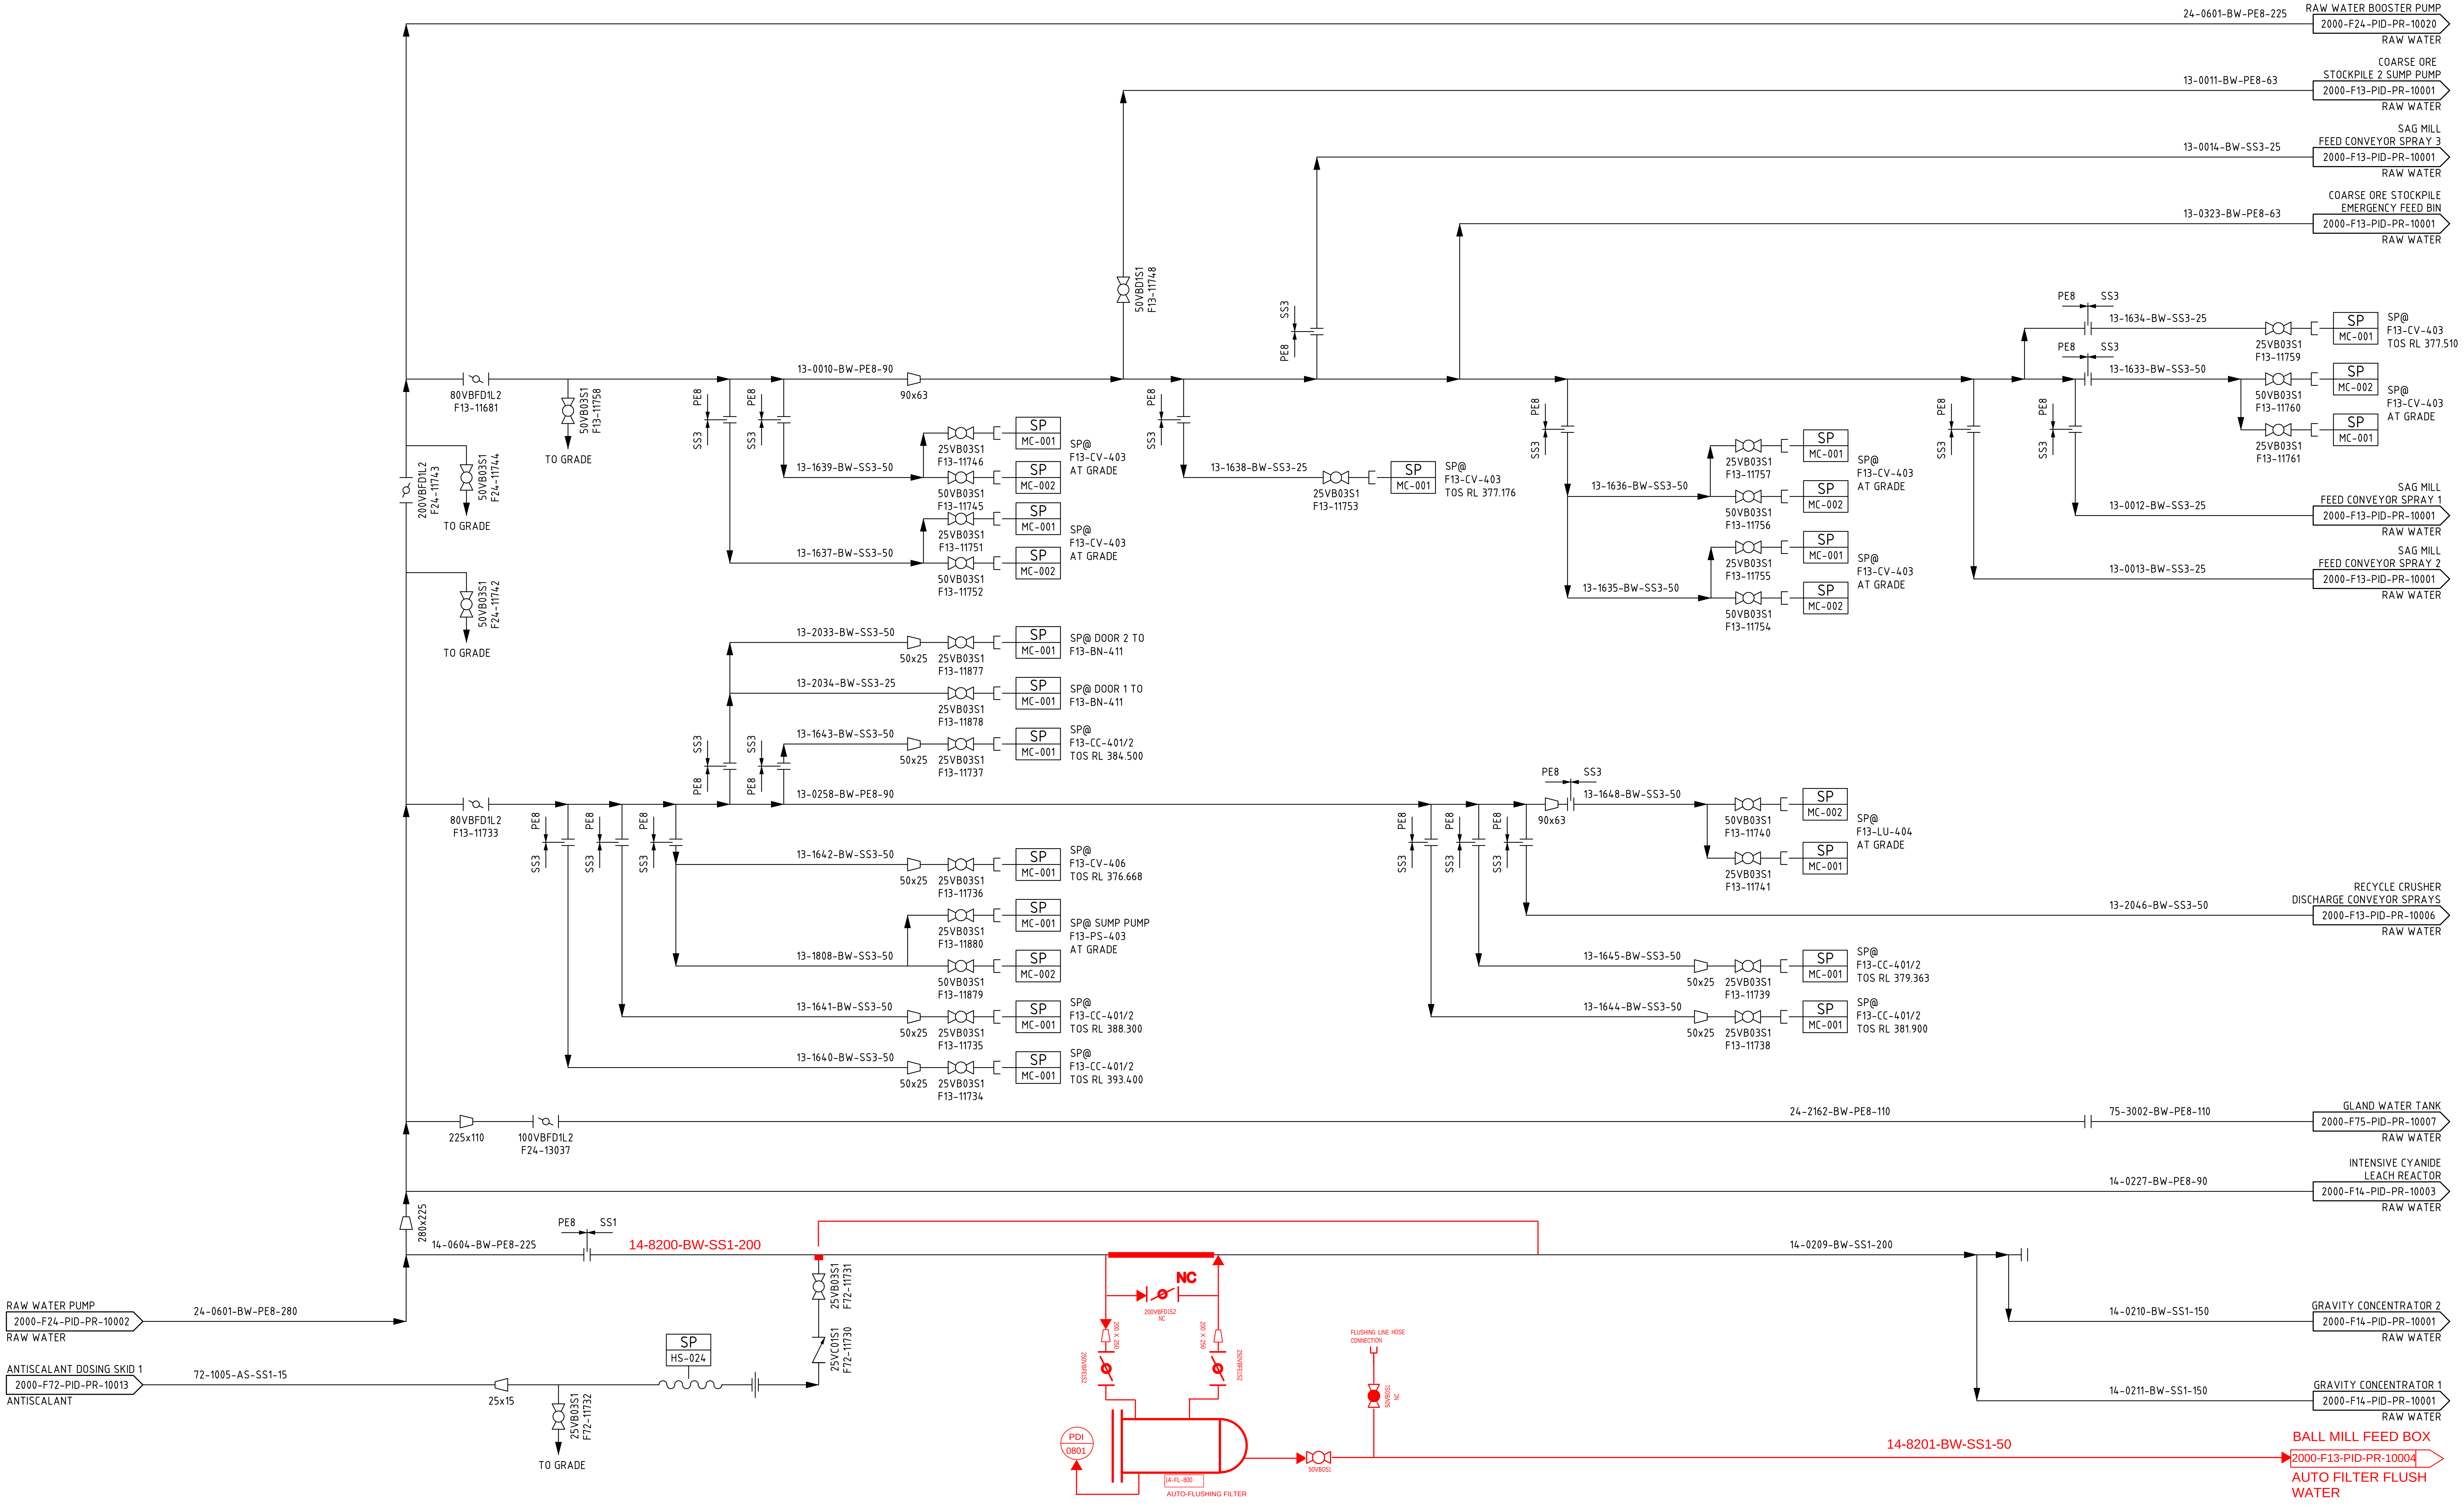
24-0601-BW-PE8-225
RAW WATER BOOSTER PUMP
2000-F24-PID-PR-10020
RAW WATER
13-0011-BW-PE8-63
COARSE ORE STOCKPILE 2 SUMP PUMP
2000-F13-PID-PR-10001
RAW WATER
13-0014-BW-SS3-25
SAG MILL FEED CONVEYOR SPRAY 3
2000-F13-PID-PR-10001
RAW WATER
13-0323-BW-PE8-63
COARSE ORE STOCKPILE EMERGENCY FEED BIN
2000-F13-PID-PR-10001
RAW WATER
50VBD1S1
F13-11748
80VBFD1L2
F13-11681
50VB03S1
F13-11758
TO GRADE
200VBFD1L2
F24-11743
50VB03S1
F24-11744
TO GRADE
50VB03S1
F24-11742
TO GRADE
13-0010-BW-PE8-90
90x63
PE8
SS3
13-1639-BW-SS3-50
25VB03S1
F13-11746
50VB03S1
F13-11745
SP
MC-001
SP
MC-002
SP@
F13-CV-403
AT GRADE
13-1637-BW-SS3-50
25VB03S1
F13-11751
50VB03S1
F13-11752
SP
MC-001
SP
MC-002
SP@
F13-CV-403
AT GRADE
13-1638-BW-SS3-25
25VB03S1
F13-11753
SP
MC-001
SP@
F13-CV-403
TOS RL 377.176
13-1636-BW-SS3-50
25VB03S1
F13-11757
50VB03S1
F13-11756
SP
MC-001
SP
MC-002
SP@
F13-CV-403
AT GRADE
13-1635-BW-SS3-50
25VB03S1
F13-11755
50VB03S1
F13-11754
SP
MC-001
SP
MC-002
SP@
F13-CV-403
AT GRADE
PE8
SS3
13-1634-BW-SS3-25
25VB03S1
F13-11759
SP
MC-001
SP@
F13-CV-403
TOS RL 377.510
13-1633-BW-SS3-50
50VB03S1
F13-11760
25VB03S1
F13-11761
SP
MC-002
SP
MC-001
SP@
F13-CV-403
AT GRADE
13-0012-BW-SS3-25
SAG MILL FEED CONVEYOR SPRAY 1
2000-F13-PID-PR-10001
RAW WATER
13-0013-BW-SS3-25
SAG MILL FEED CONVEYOR SPRAY 2
2000-F13-PID-PR-10001
RAW WATER
13-2033-BW-SS3-50
50x25
25VB03S1
F13-11877
SP
MC-001
SP@ DOOR 2 TO
F13-BN-411
13-2034-BW-SS3-25
25VB03S1
F13-11878
SP
MC-001
SP@ DOOR 1 TO
F13-BN-411
13-1643-BW-SS3-50
50x25
25VB03S1
F13-11737
SP
MC-001
SP@
F13-CC-401/2
TOS RL 384.500
80VBFD1L2
F13-11733
13-0258-BW-PE8-90
PE8
SS3
90x63
13-1648-BW-SS3-50
50VB03S1
F13-11740
25VB03S1
F13-11741
SP
MC-002
SP
MC-001
SP@
F13-LU-404
AT GRADE
13-1642-BW-SS3-50
50x25
25VB03S1
F13-11736
SP
MC-001
SP@
F13-CV-406
TOS RL 376.668
25VB03S1
F13-11880
SP
MC-001
SP@ SUMP PUMP
F13-PS-403
AT GRADE
13-1808-BW-SS3-50
50VB03S1
F13-11879
SP
MC-002
13-1641-BW-SS3-50
50x25
25VB03S1
F13-11735
SP
MC-001
SP@
F13-CC-401/2
TOS RL 388.300
13-1640-BW-SS3-50
50x25
25VB03S1
F13-11734
SP
MC-001
SP@
F13-CC-401/2
TOS RL 393.400
13-2046-BW-SS3-50
RECYCLE CRUSHER DISCHARGE CONVEYOR SPRAYS
2000-F13-PID-PR-10006
RAW WATER
13-1645-BW-SS3-50
50x25
25VB03S1
F13-11739
SP
MC-001
SP@
F13-CC-401/2
TOS RL 379.363
13-1644-BW-SS3-50
50x25
25VB03S1
F13-11738
SP
MC-001
SP@
F13-CC-401/2
TOS RL 381.900
225x110
100VBFD1L2
F24-13037
24-2162-BW-PE8-110
75-3002-BW-PE8-110
GLAND WATER TANK
2000-F75-PID-PR-10007
RAW WATER
14-0227-BW-PE8-90
INTENSIVE CYANIDE LEACH REACTOR
2000-F14-PID-PR-10003
RAW WATER
280x225
14-0604-BW-PE8-225
PE8
SS1
14-8200-BW-SS1-200
14-0209-BW-SS1-200
25VB03S1
F72-11731
25VC01S1
F72-11730
SP
HS-024
RAW WATER PUMP
2000-F24-PID-PR-10002
RAW WATER
24-0601-BW-PE8-280
ANTISCALANT DOSING SKID 1
2000-F72-PID-PR-10013
ANTISCALANT
72-1005-AS-SS1-15
25x15
25VB03S1
F72-11732
TO GRADE
NC
200VBFD1S2
NC
200 X 250
200 X 250
250VBFE1S2
250VBFE1S2
FLUSHING LINE HOSE CONNECTION
50VBOS1
NC
PDI
0801
14-FL-800
AUTO-FLUSHING FILTER
50VBOS1
14-8201-BW-SS1-50
14-0210-BW-SS1-150
GRAVITY CONCENTRATOR 2
2000-F14-PID-PR-10001
RAW WATER
14-0211-BW-SS1-150
GRAVITY CONCENTRATOR 1
2000-F14-PID-PR-10001
RAW WATER
BALL MILL FEED BOX
2000-F13-PID-PR-10004
AUTO FILTER FLUSH WATER