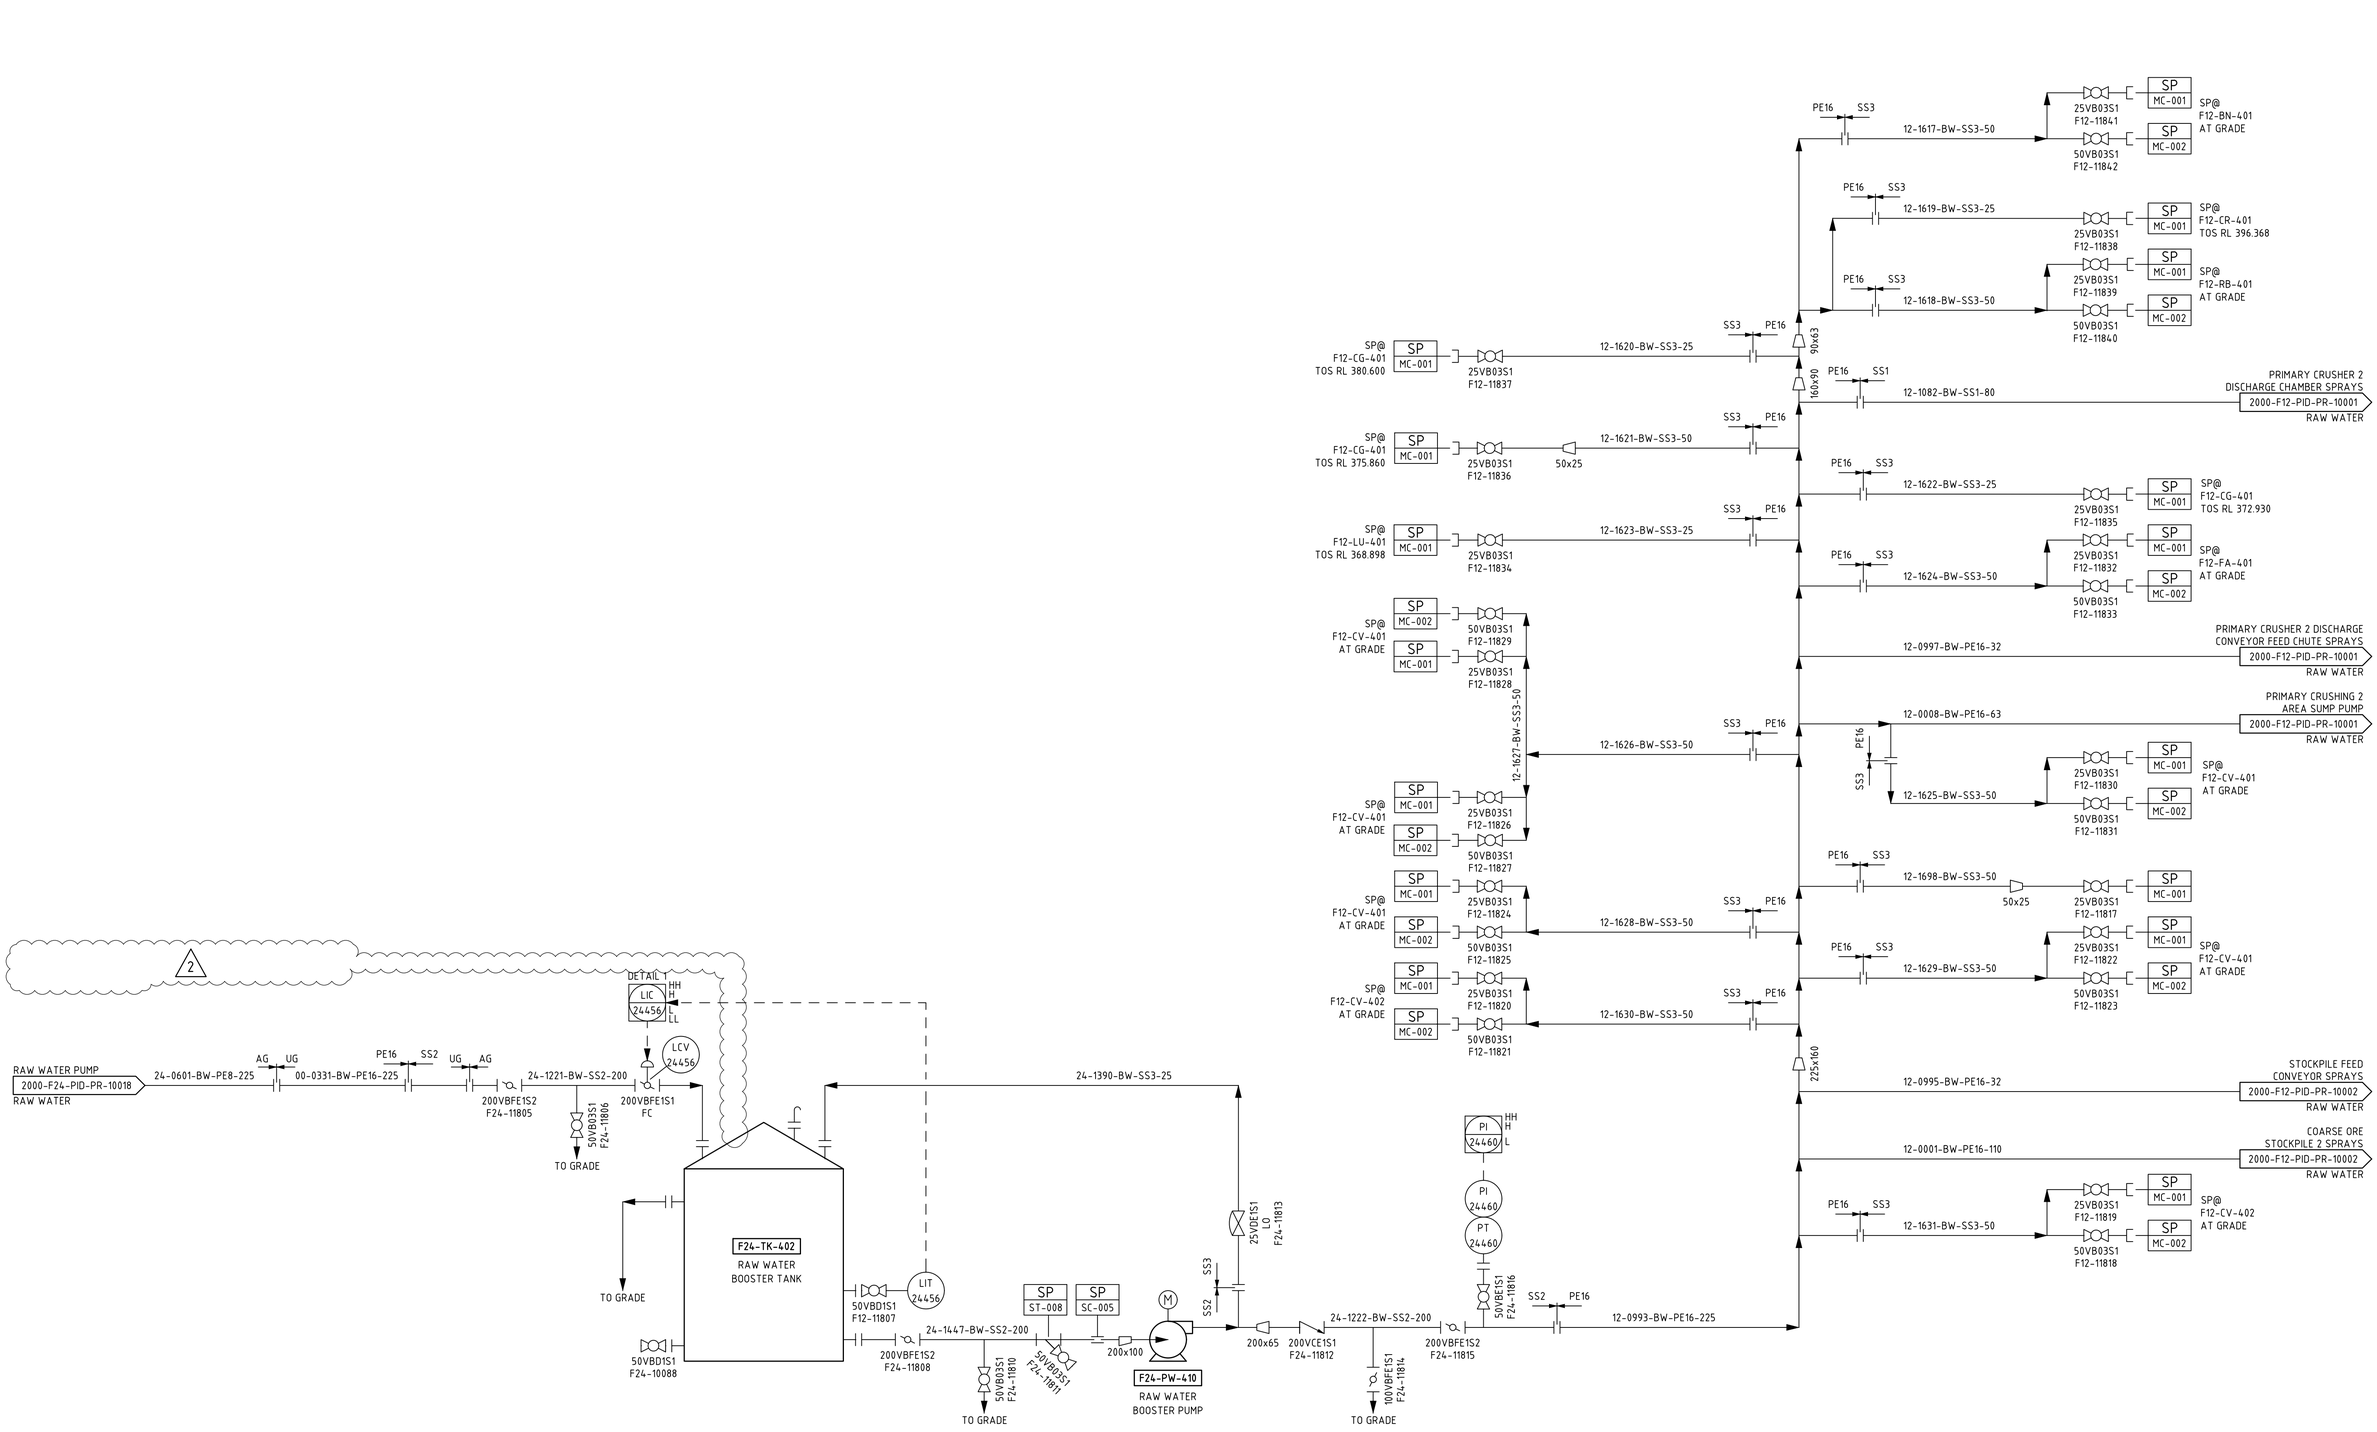

2
DETAIL 1
LIC 24456
HH
H
L
LL
LCV 24456
RAW WATER PUMP
2000-F24-PID-PR-10018
RAW WATER
24-0601-BW-PE8-225
AG
UG
00-0331-BW-PE16-225
PE16
SS2
UG
AG
24-1221-BW-SS2-200
200VBFE1S2 F24-11805
200VBFE1S1 FC
50VBD3S1 F24-11806
TO GRADE
24-1390-BW-SS3-25
F24-TK-402
RAW WATER BOOSTER TANK
TO GRADE
50VBD1S1 F24-10088
50VBD1S1 F12-11807
LIT 24456
200VBFE1S2 F24-11808
24-1447-BW-SS2-200
SP ST-008
SP SC-005
50VBD3S1 F24-11810
50VBD3S1 F24-11811
TO GRADE
M
200x100
F24-PW-410
RAW WATER BOOSTER PUMP
SS3
SS2
25VDE1S1 LO F24-11813
200x65
200VCE1S1 F24-11812
24-1222-BW-SS2-200
100VBFE1S1 F24-11814
TO GRADE
PI 24460
HH
H
L
PI 24460
PT 24460
50VBE1S1 F24-11816
200VBFE1S2 F24-11815
SS2
PE16
12-0993-BW-PE16-225
225x160
12-0995-BW-PE16-32
STOCKPILE FEED CONVEYOR SPRAYS
2000-F12-PID-PR-10002
RAW WATER
12-0001-BW-PE16-110
COARSE ORE STOCKPILE 2 SPRAYS
2000-F12-PID-PR-10002
RAW WATER
12-1627-BW-SS3-50
12-1626-BW-SS3-50
SP@ F12-CV-401 AT GRADE
SP MC-001
SP MC-002
50VB03S1 F12-11826
50VB03S1 F12-11827
25VB03S1 F12-11824
50VB03S1 F12-11825
25VB03S1 F12-11820
50VB03S1 F12-11821
12-1628-BW-SS3-50
12-1630-BW-SS3-50
SS3
PE16
12-1620-BW-SS3-25
SP@ F12-CG-401 TOS RL 380.600
25VB03S1 F12-11837
12-1621-BW-SS3-50
SP@ F12-CG-401 TOS RL 375.860
25VB03S1 F12-11836
50x25
12-1623-BW-SS3-25
SP@ F12-LU-401 TOS RL 368.898
25VB03S1 F12-11834
50VB03S1 F12-11829
25VB03S1 F12-11828
SP@ F12-CV-401 AT GRADE
90x63
160x90
SS1
12-1082-BW-SS1-80
PRIMARY CRUSHER 2 DISCHARGE CHAMBER SPRAYS
2000-F12-PID-PR-10001
RAW WATER
12-1617-BW-SS3-50
25VB03S1 F12-11841
50VB03S1 F12-11842
SP@ F12-BN-401 AT GRADE
12-1619-BW-SS3-25
25VB03S1 F12-11838
SP@ F12-CR-401 TOS RL 396.368
12-1618-BW-SS3-50
25VB03S1 F12-11839
50VB03S1 F12-11840
SP@ F12-RB-401 AT GRADE
12-1622-BW-SS3-25
25VB03S1 F12-11835
SP@ F12-CG-401 TOS RL 372.930
12-1624-BW-SS3-50
25VB03S1 F12-11832
50VB03S1 F12-11833
SP@ F12-FA-401 AT GRADE
12-0997-BW-PE16-32
PRIMARY CRUSHER 2 DISCHARGE CONVEYOR FEED CHUTE SPRAYS
2000-F12-PID-PR-10001
RAW WATER
12-0008-BW-PE16-63
PRIMARY CRUSHING 2 AREA SUMP PUMP
2000-F12-PID-PR-10001
RAW WATER
12-1625-BW-SS3-50
25VB03S1 F12-11830
50VB03S1 F12-11831
SP@ F12-CV-401 AT GRADE
12-1698-BW-SS3-50
50x25
25VB03S1 F12-11817
12-1629-BW-SS3-50
25VB03S1 F12-11822
50VB03S1 F12-11823
SP@ F12-CV-401 AT GRADE
12-1631-BW-SS3-50
25VB03S1 F12-11819
50VB03S1 F12-11818
SP@ F12-CV-402 AT GRADE