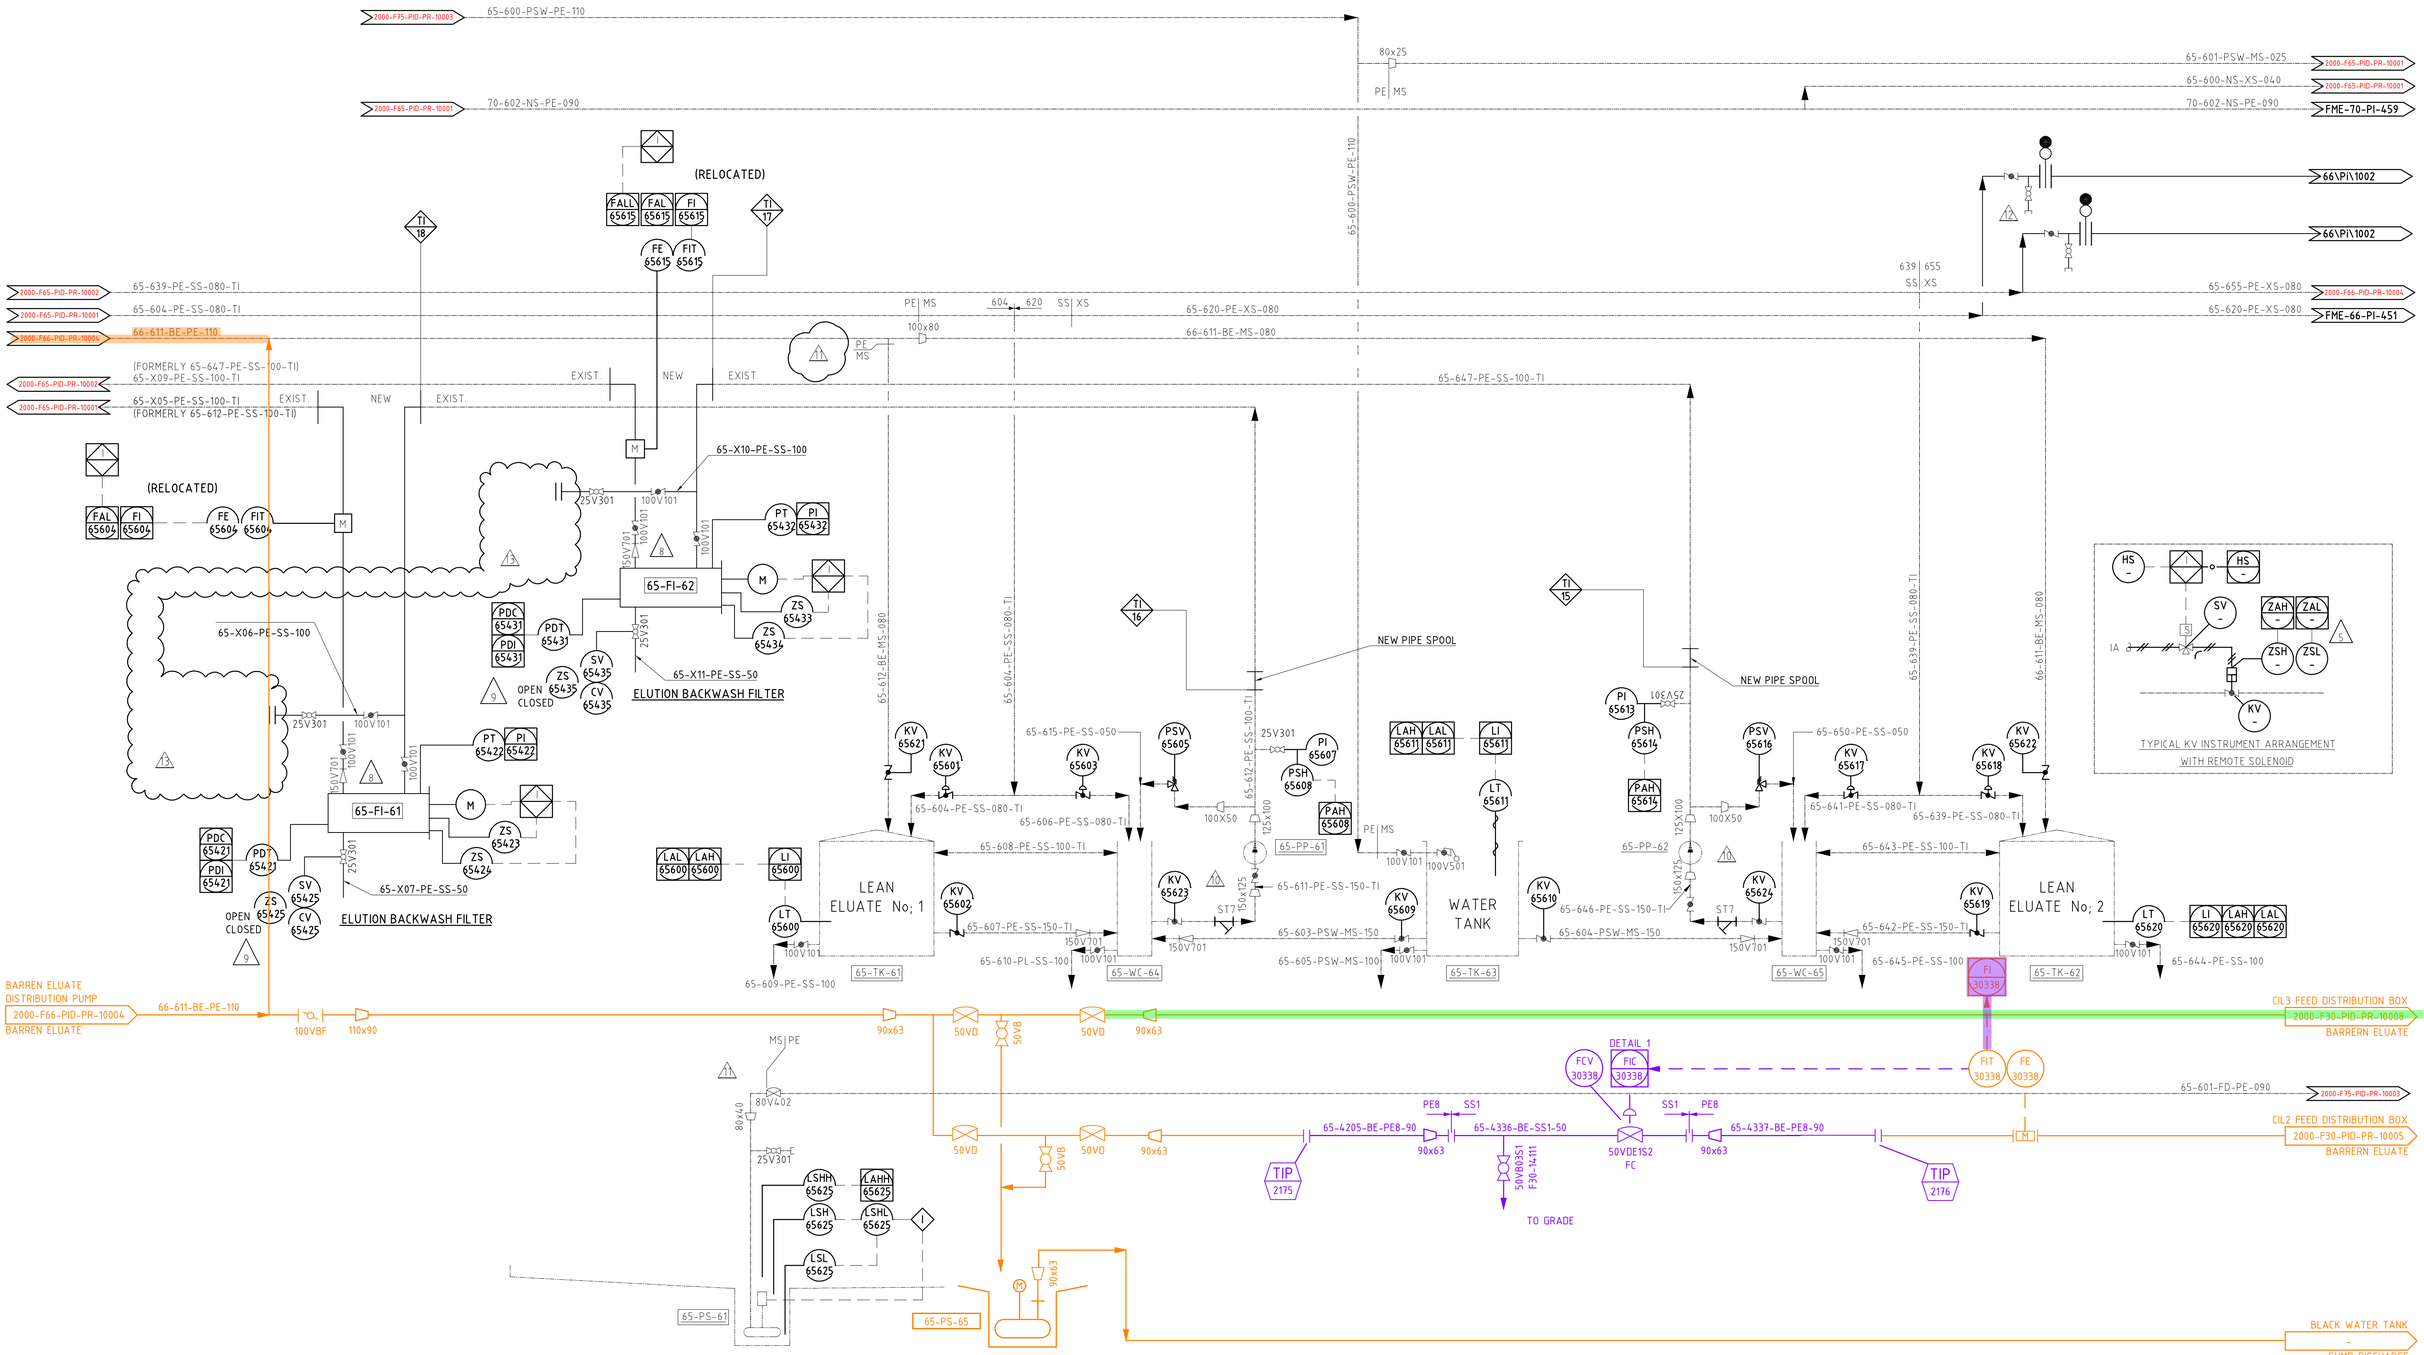


NOTES:

1. FOR "WW" "CA" & "IA" REFER FME-81-PI-0467

65-TK-61	LEAN ELUATE TANK No 1
65-PP-61	ELUTION CIRCUIT No 1 WATER PUMP
65-WC-64	ELUTION CIRCUIT No 1 RECYCLE STAND PIPE
65-PS-61	ELUTION AREA WASHDOWN PUMP
65-PS-65	CARBON TRANSFER AREA SUMP PUMP

65-FI-61	ELUTION BACKWASH FILTER No 1
65-FI-62	ELUTION BACKWASH FILTER No 2
65-TK-63	ELUTION WATER TANK

65-PP-62	ELUTION CIRCUIT No 2 WATER PUMP
65-WC-65	ELUTION CIRCUIT No 2 RECYCLE STANDPIPE
65-TK-62	[redacted]ELUATE TANK No 2

LEGEND

- EXISTING
- NON-EXISTENT
- STAGE 1 - NEW
- STAGE 1 - REMOVE
- STAGE 1 - DECOMMISSIONED (OTHERS)
- STAGE 2 - NEW
- STAGE 2 - REMOVE
- STAGE 2 - DECOMMISSIONED (OTHERS)