NOTES:

1. INSTRUMENT NUMBERS PREFIXED BY THE AREA SHOWN ON P&ID FOR CLARITY, EG F75-PI-1015.


LEGENDS:

EXISTING

EXISTING TO BE MADE REDUNDANT DURING STAGE 1

NEW

FUTURE

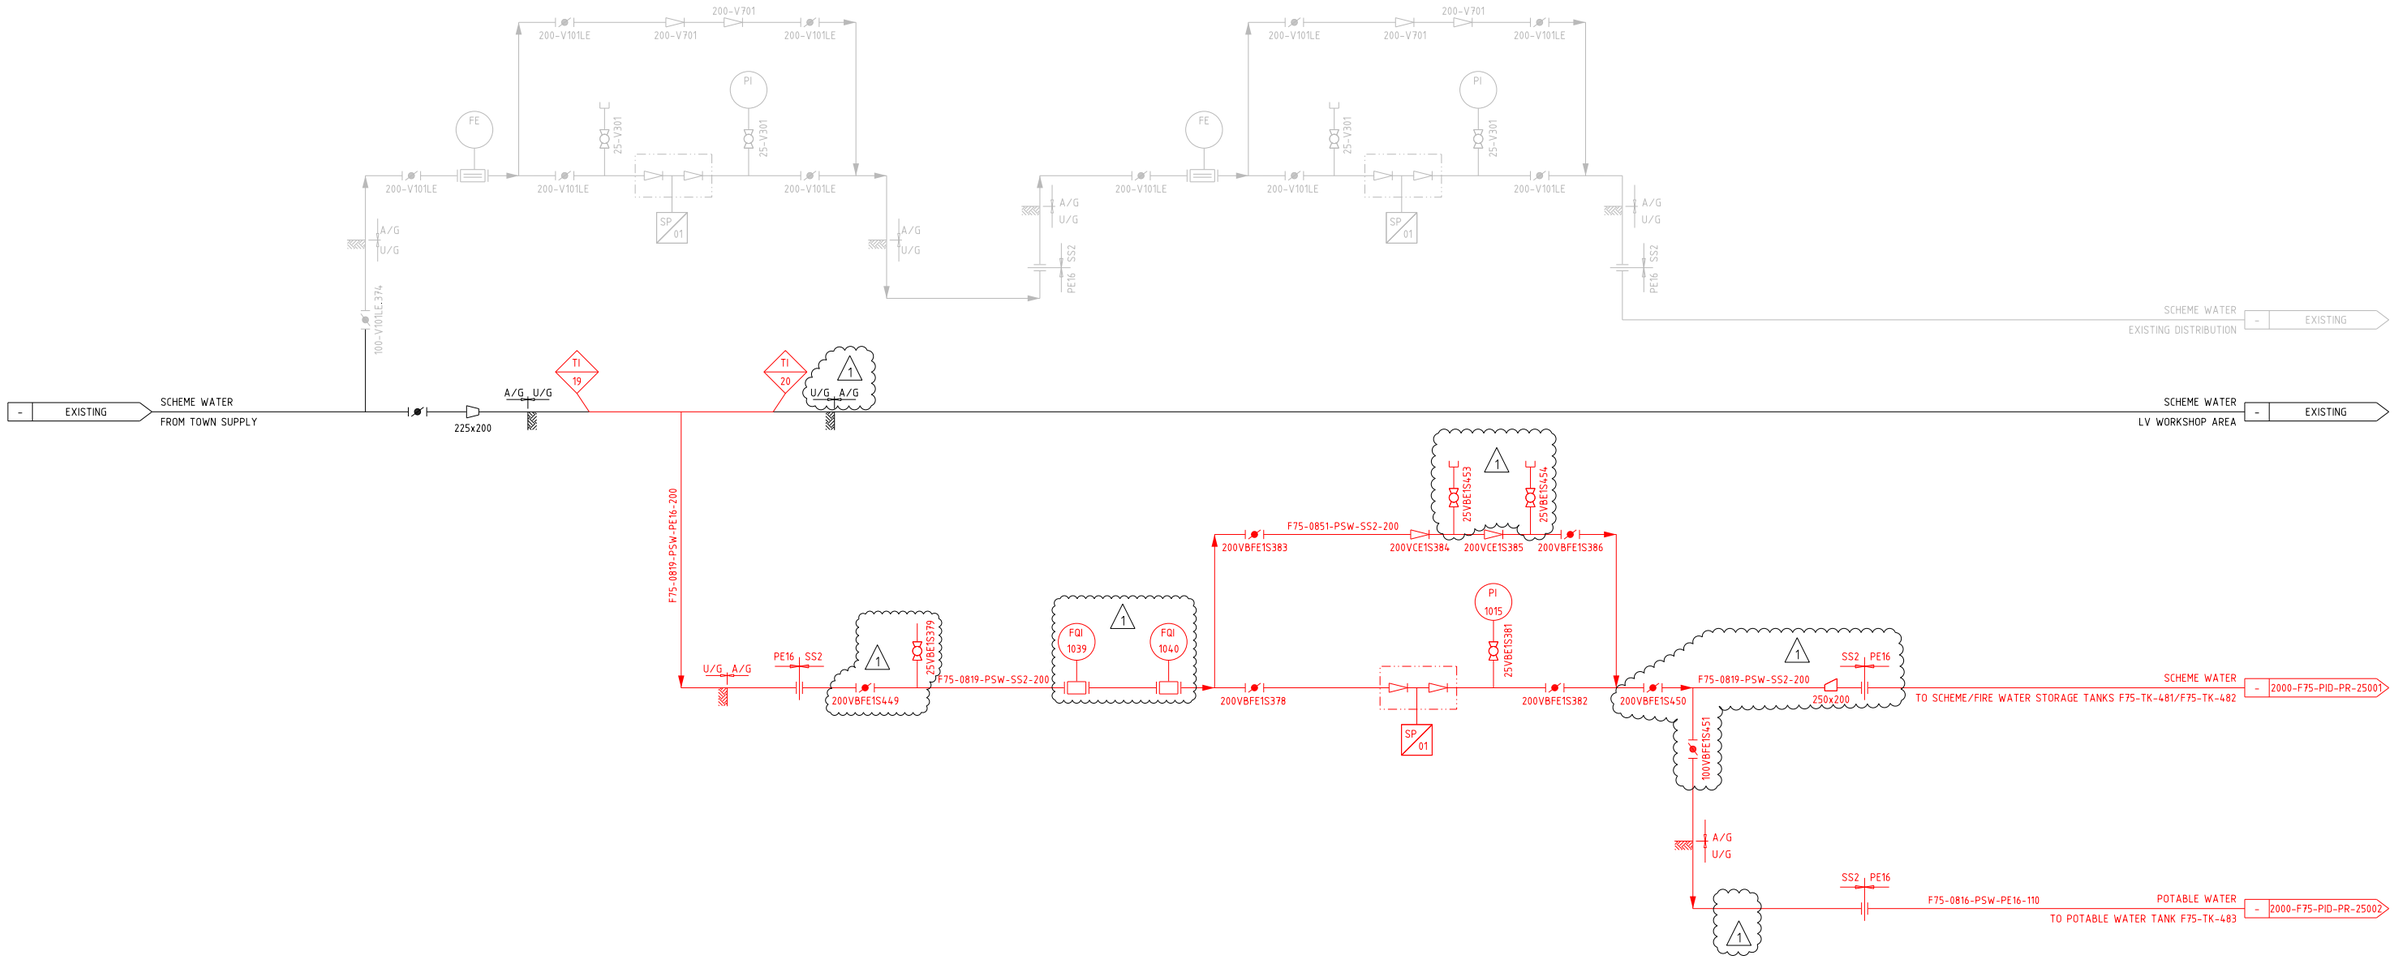

APPROVED FOR CONSTRUCTION