LEGEND:

- EXISTING
- NEW
- FUTURE
- DECOMMISSIONED

NOTES:

1. PIPE ON TOP OF TSF TO BE FLANGED EVERY 40m.
2. VALVE TO BE INSTALLED WITHOUT A HANDLE.

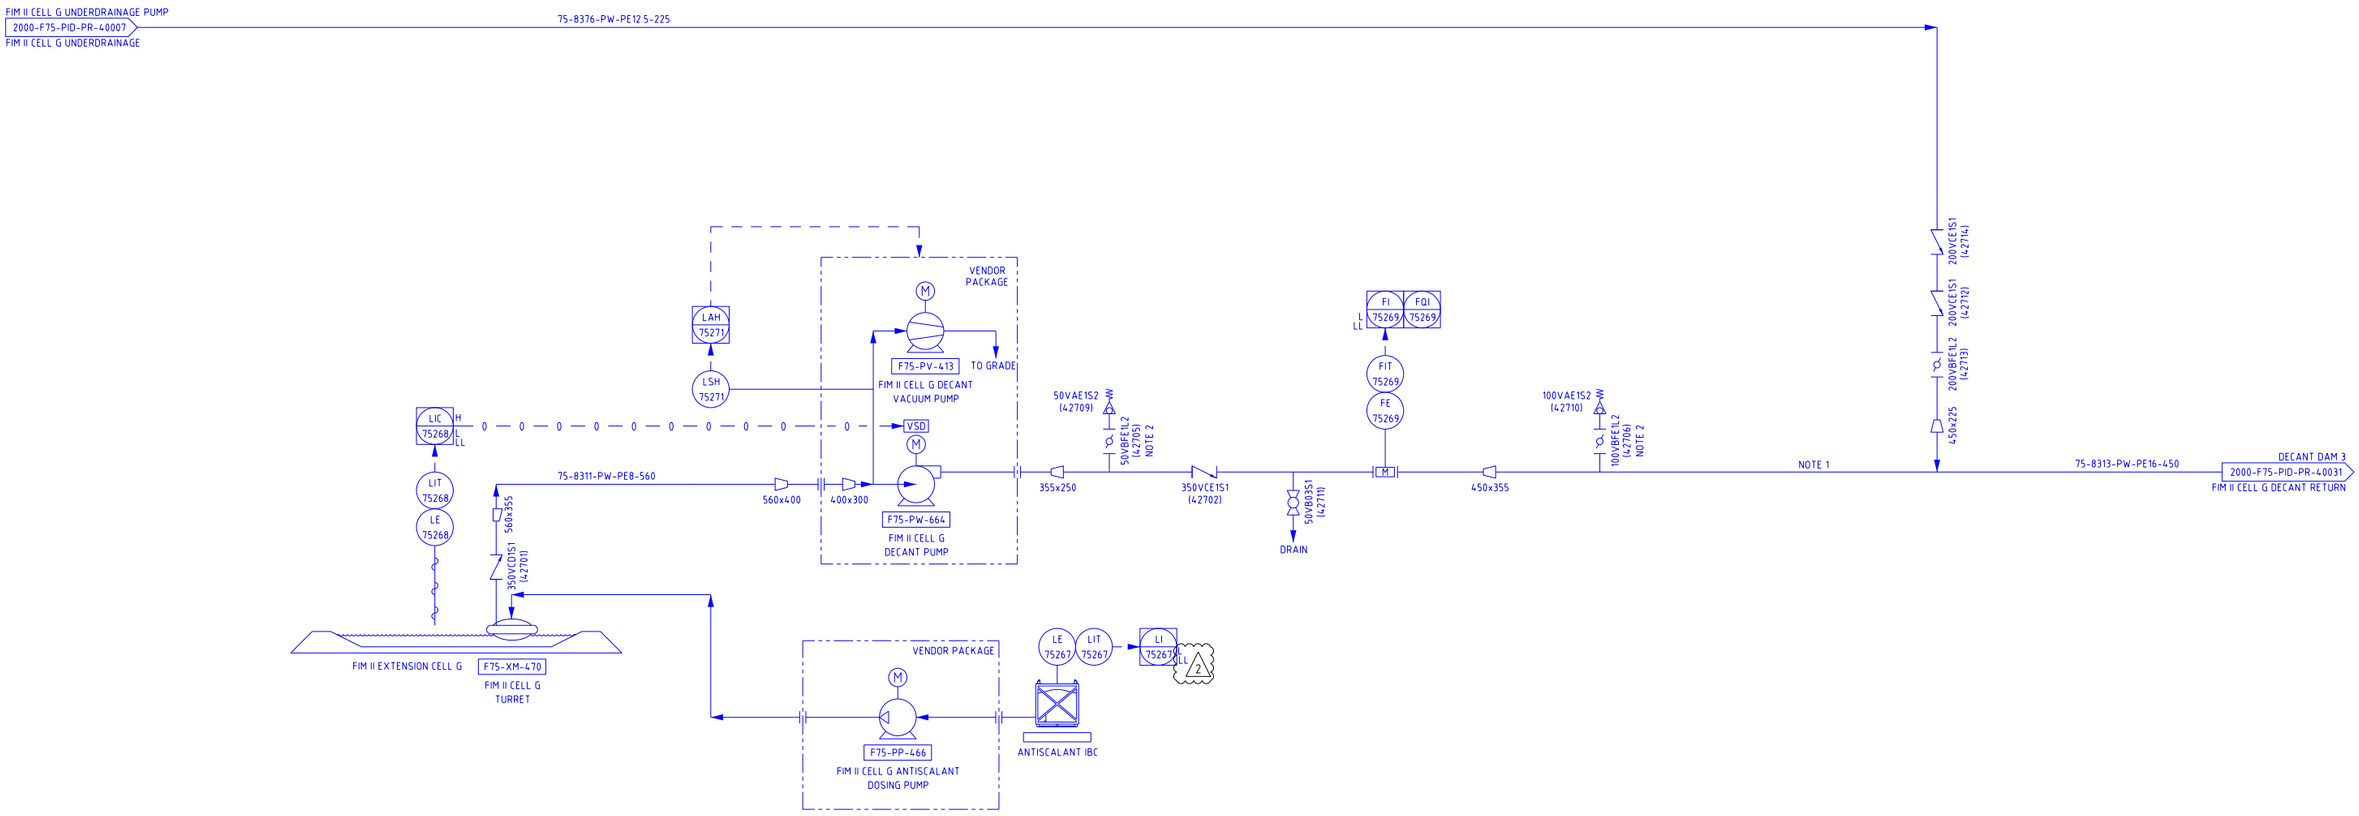

APPROVED FOR CONSTRUCTION