
LEGEND:

- EXISTING
- NEW
- FUTURE
- DECOMMISSIONED

NOTES:

1. VALVE TO BE INSTALLED WITHOUT A HANDLE.
2. MANUAL OPERATED VALVE WITH PROXIMITY SWITCHES.

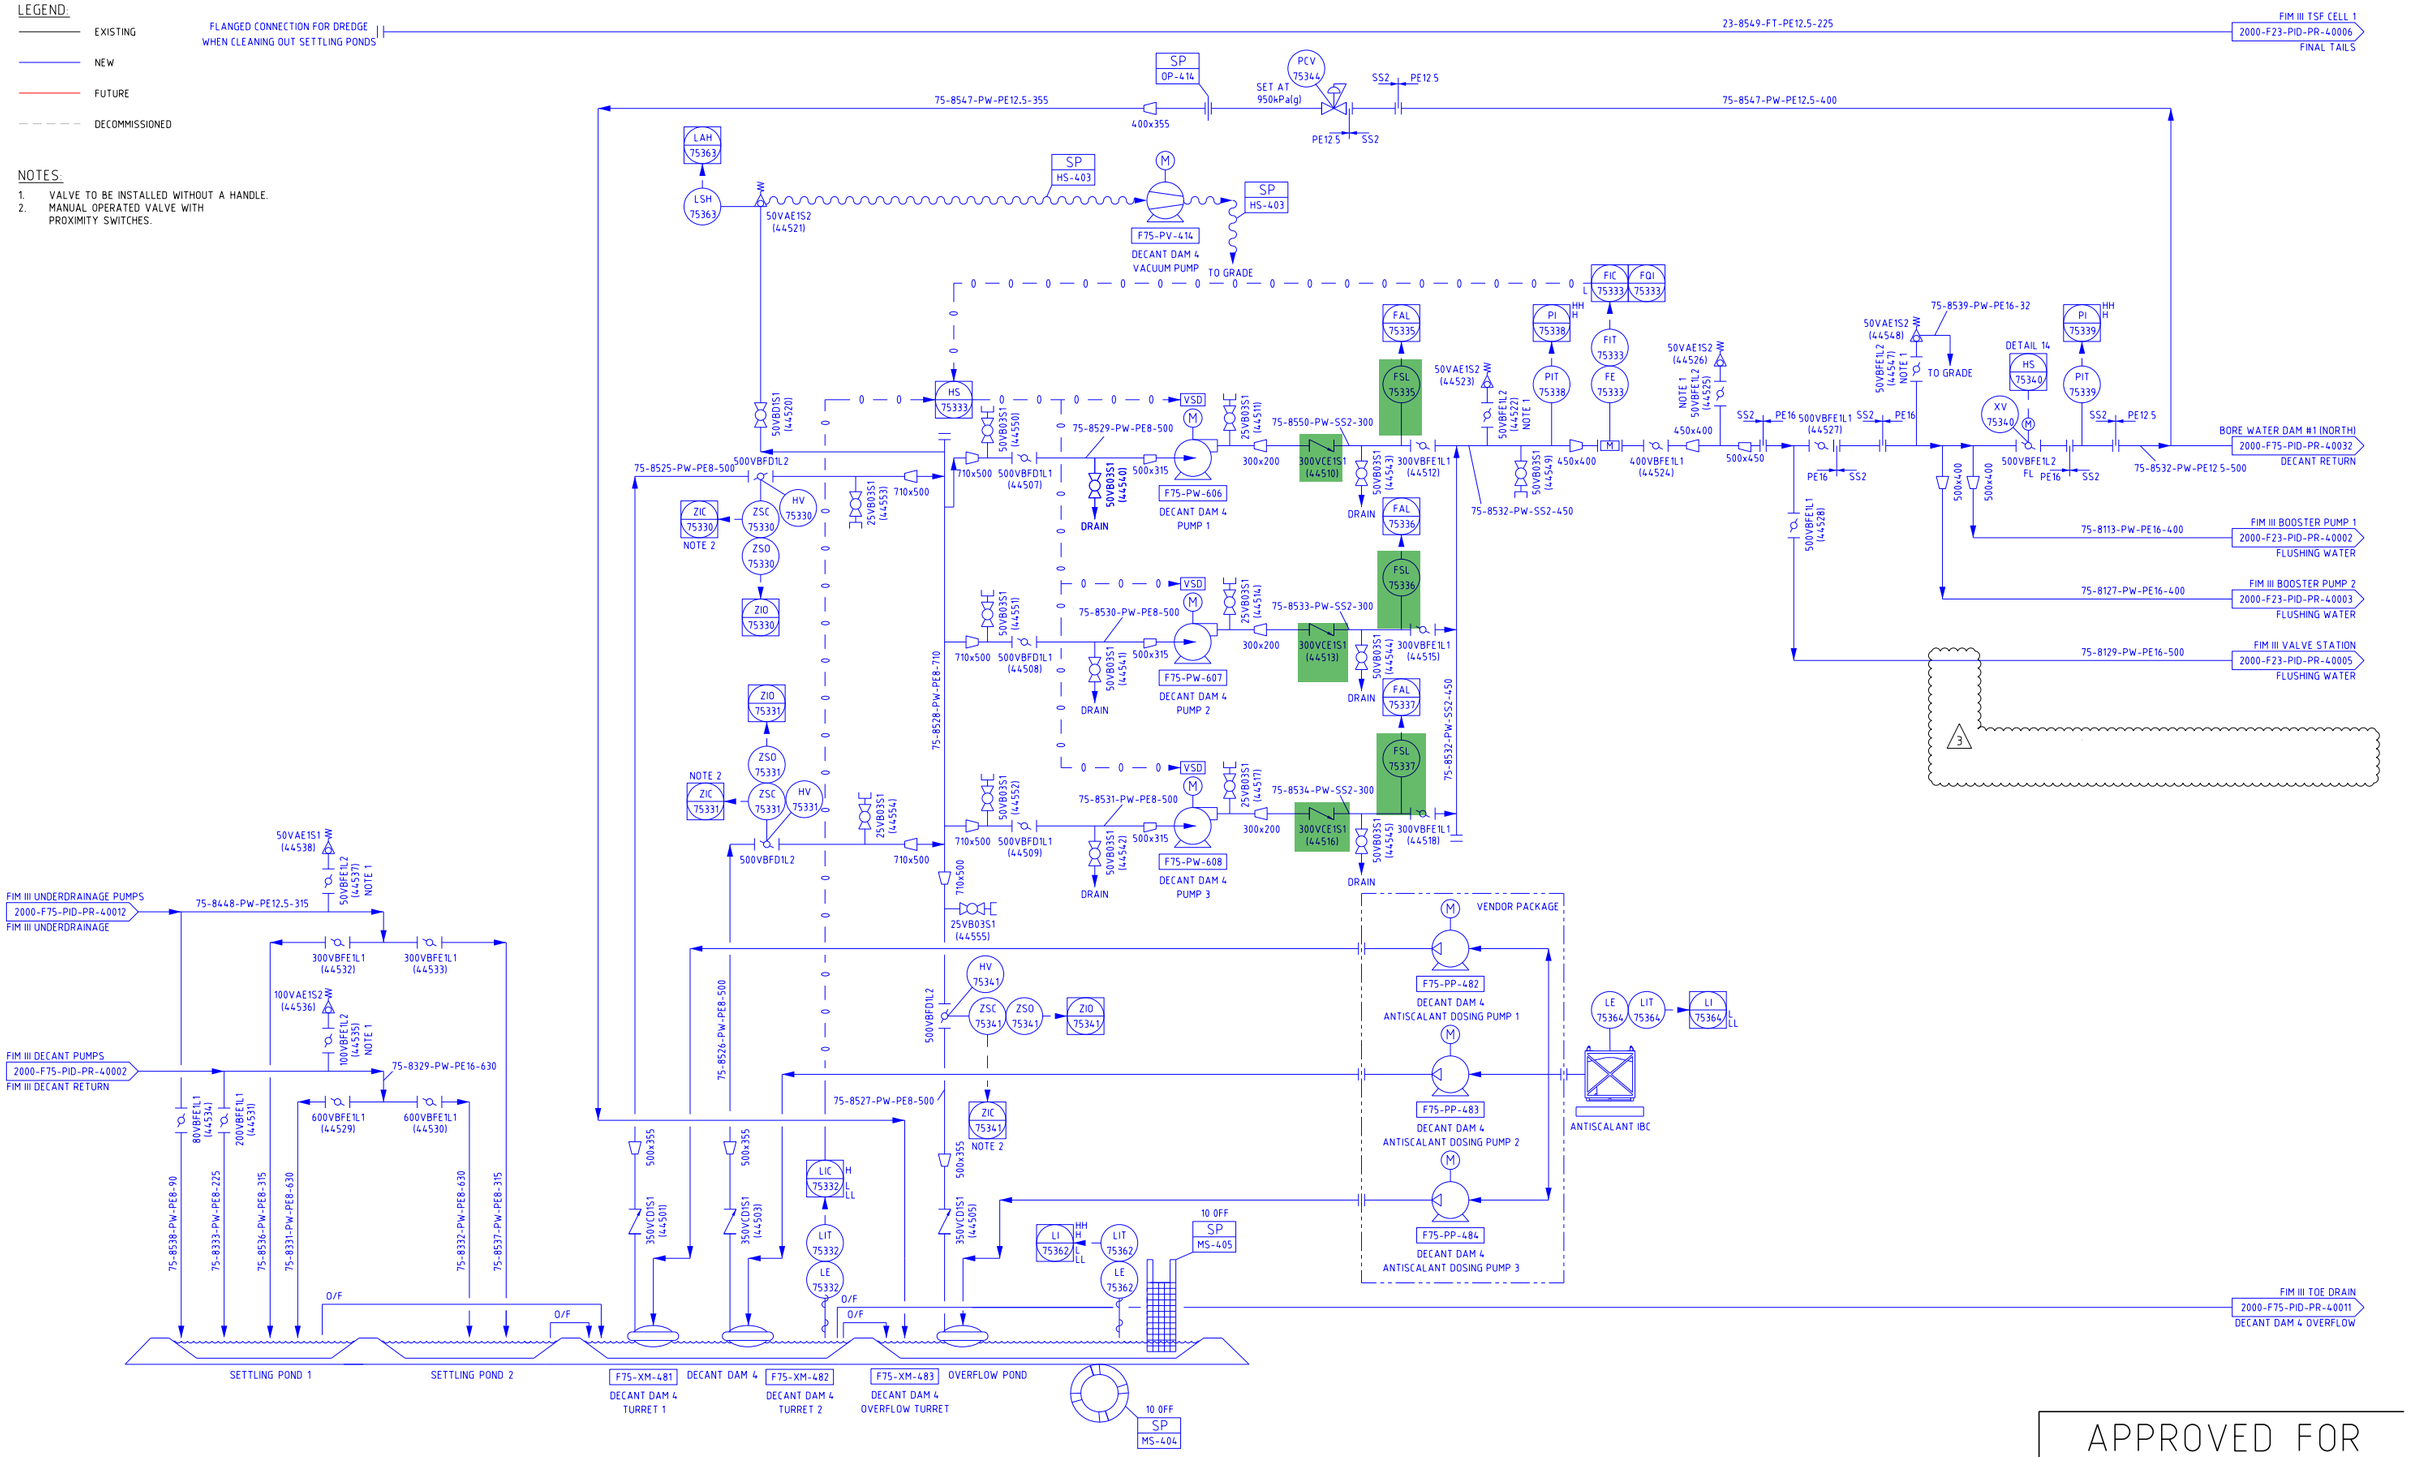

APPROVED FOR CONSTRUCTION