
F13-SR-002
415V BALL MILL SWITCHROOM

F13-SW-003
BALL MILL 415V MOTOR CONTROL CENTRE

CONTINUED ON SHT 4
2000-F13-SLD-EL-10904

CONTINUED ON SHT 6
2000-F13-SLD-EL-10906

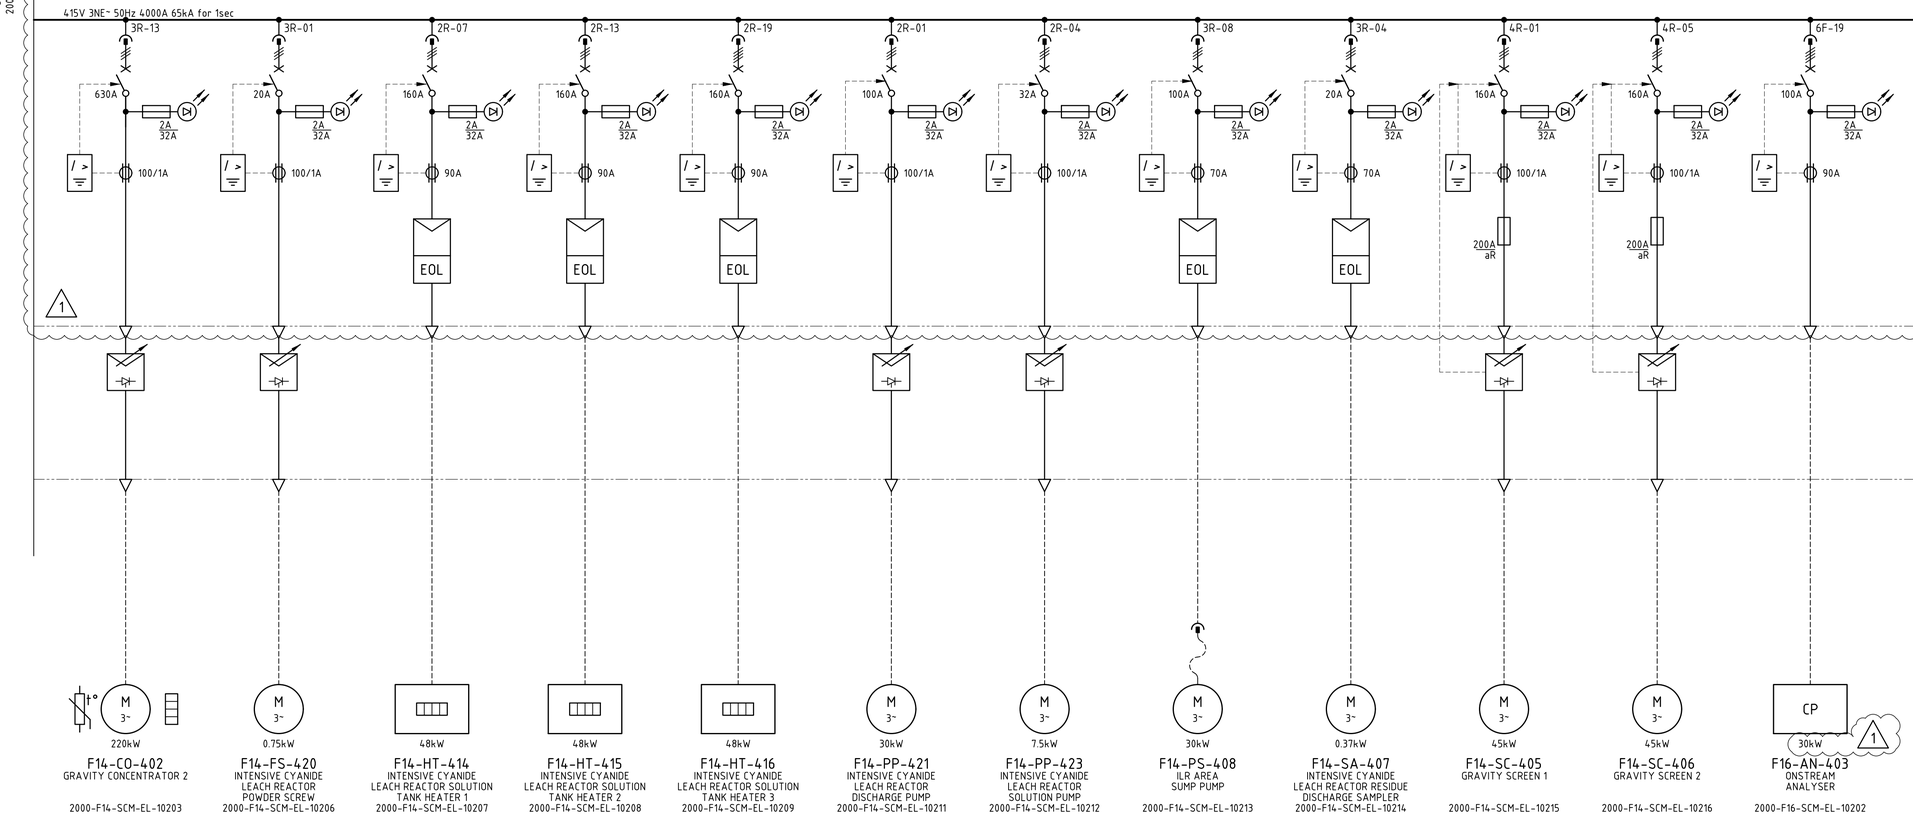

NOTES

1. REFER TO SHEET 1.

LEGEND

1. REFER TO SHEET 1.

Approved	X
Approved as Noted	
Not Approved	
For Information Only	

Signed [redacted] Date 09/10/2025

ACCEPTANCE DOES NOT RELIEVE THE SUPPLIER / CONTRACTOR OF ITS RESPONSIBILITY OR LIABILITIES UNDER THE PURCHASE ORDER / CONTRACT

2000-F13-SLD-EL-10905_Rev1

Ball mill F13-SW-003 415V MCC single line diagram sheet 5

0:\CAD PROJECTS\235 NORTHERN STAR RESOURCES LTD\235177 KCGM GROWTH PROJECT\03 DELIVERABLES\ELV\F13 - MILLING & CLASSIFICATION\2000-F13-SLD-EL-10905.DWG 25SEP25 12:52PM HOTSEAT04