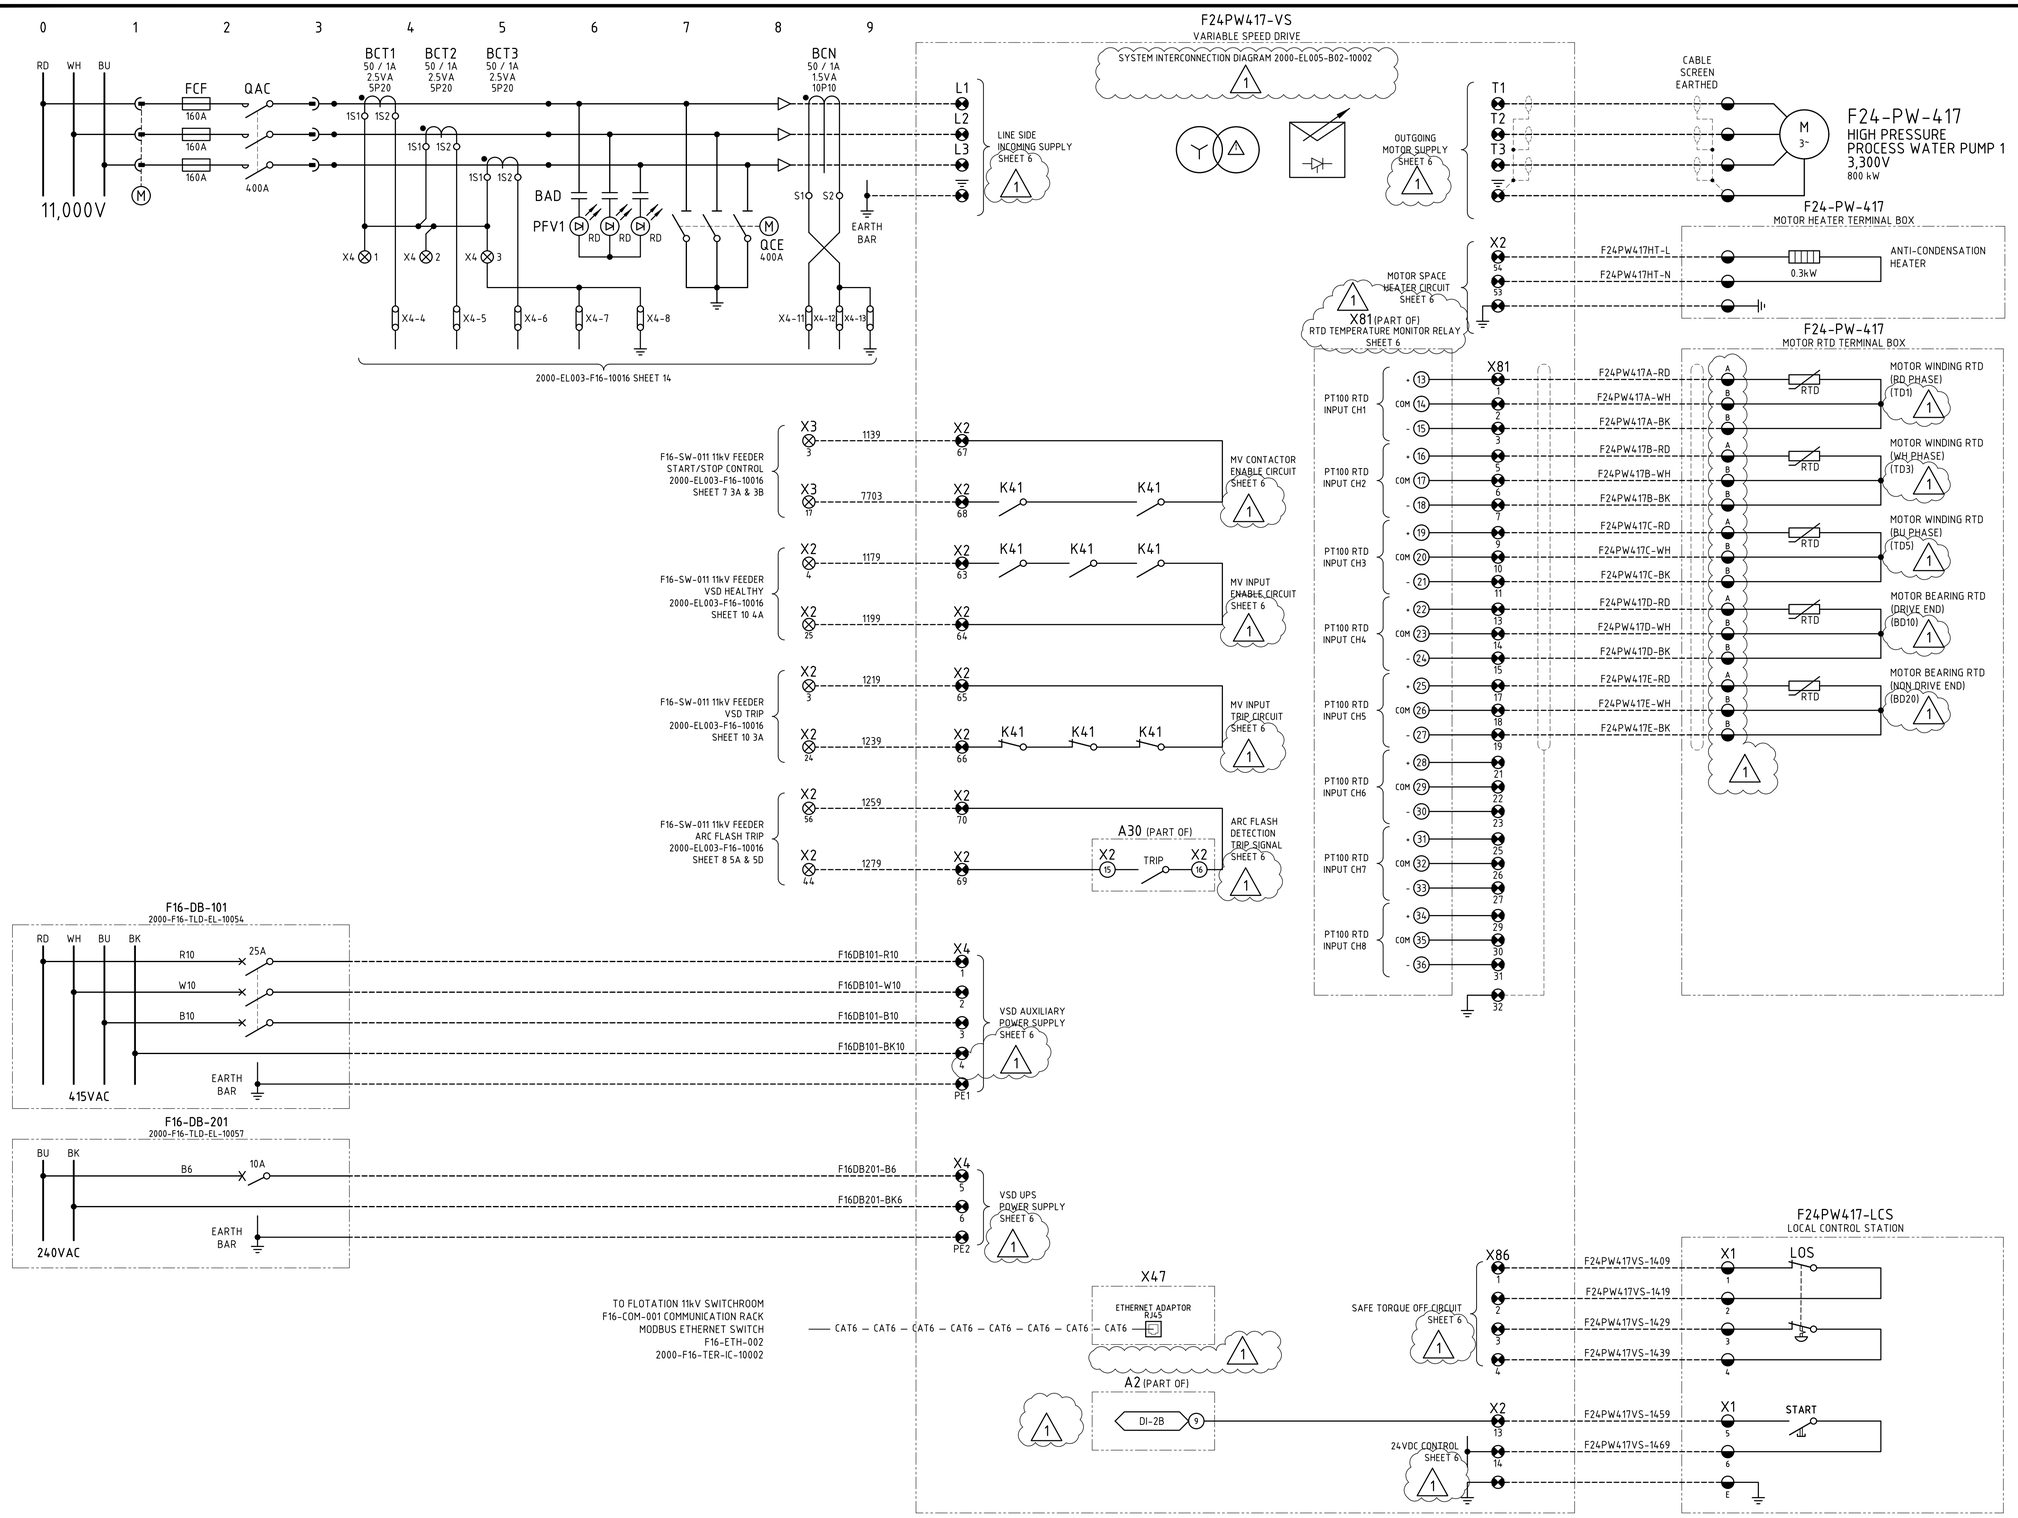



## NOTES

1. WIRE NUMBER FERRULES ON TERMINAL STRIP SHALL BE PREFIXED WITH EQUIPMENT NUMBER e.g. F24PW417-1200, UNLESS OTHERWISE NOTED.
2. EACH WIRE SHALL BE IDENTIFIED AT BOTH ENDS WITH FERRULES.

## LEGEND

- 11kV SWITCHBOARD TERMINAL
- VSD TERMINAL
- FIELD TERMINAL
- DCS OR I/O TERMINAL
- MARSHALLING TERMINAL
- DEVICE TERMINAL

PANEL A16

# 2000-F16-SCM-EL-10131_Rev1

Rougher & scavenger flotation F16-SW-011
F24-PW-417 hp process water pump 1 VSD feeder schematic diagram

D:\CAD PROJECTS\235 NORTHERN STAR RESOURCES LTD\23517 KCGM GROWTH PROJECT\03 DELIVERABLES\E\LVF16 - ROUGHER & SCAVENGER FLOTATION\2000-F16-SCM-EL-10131.DWG 09SEP25 6:43AM HOTSEAT04