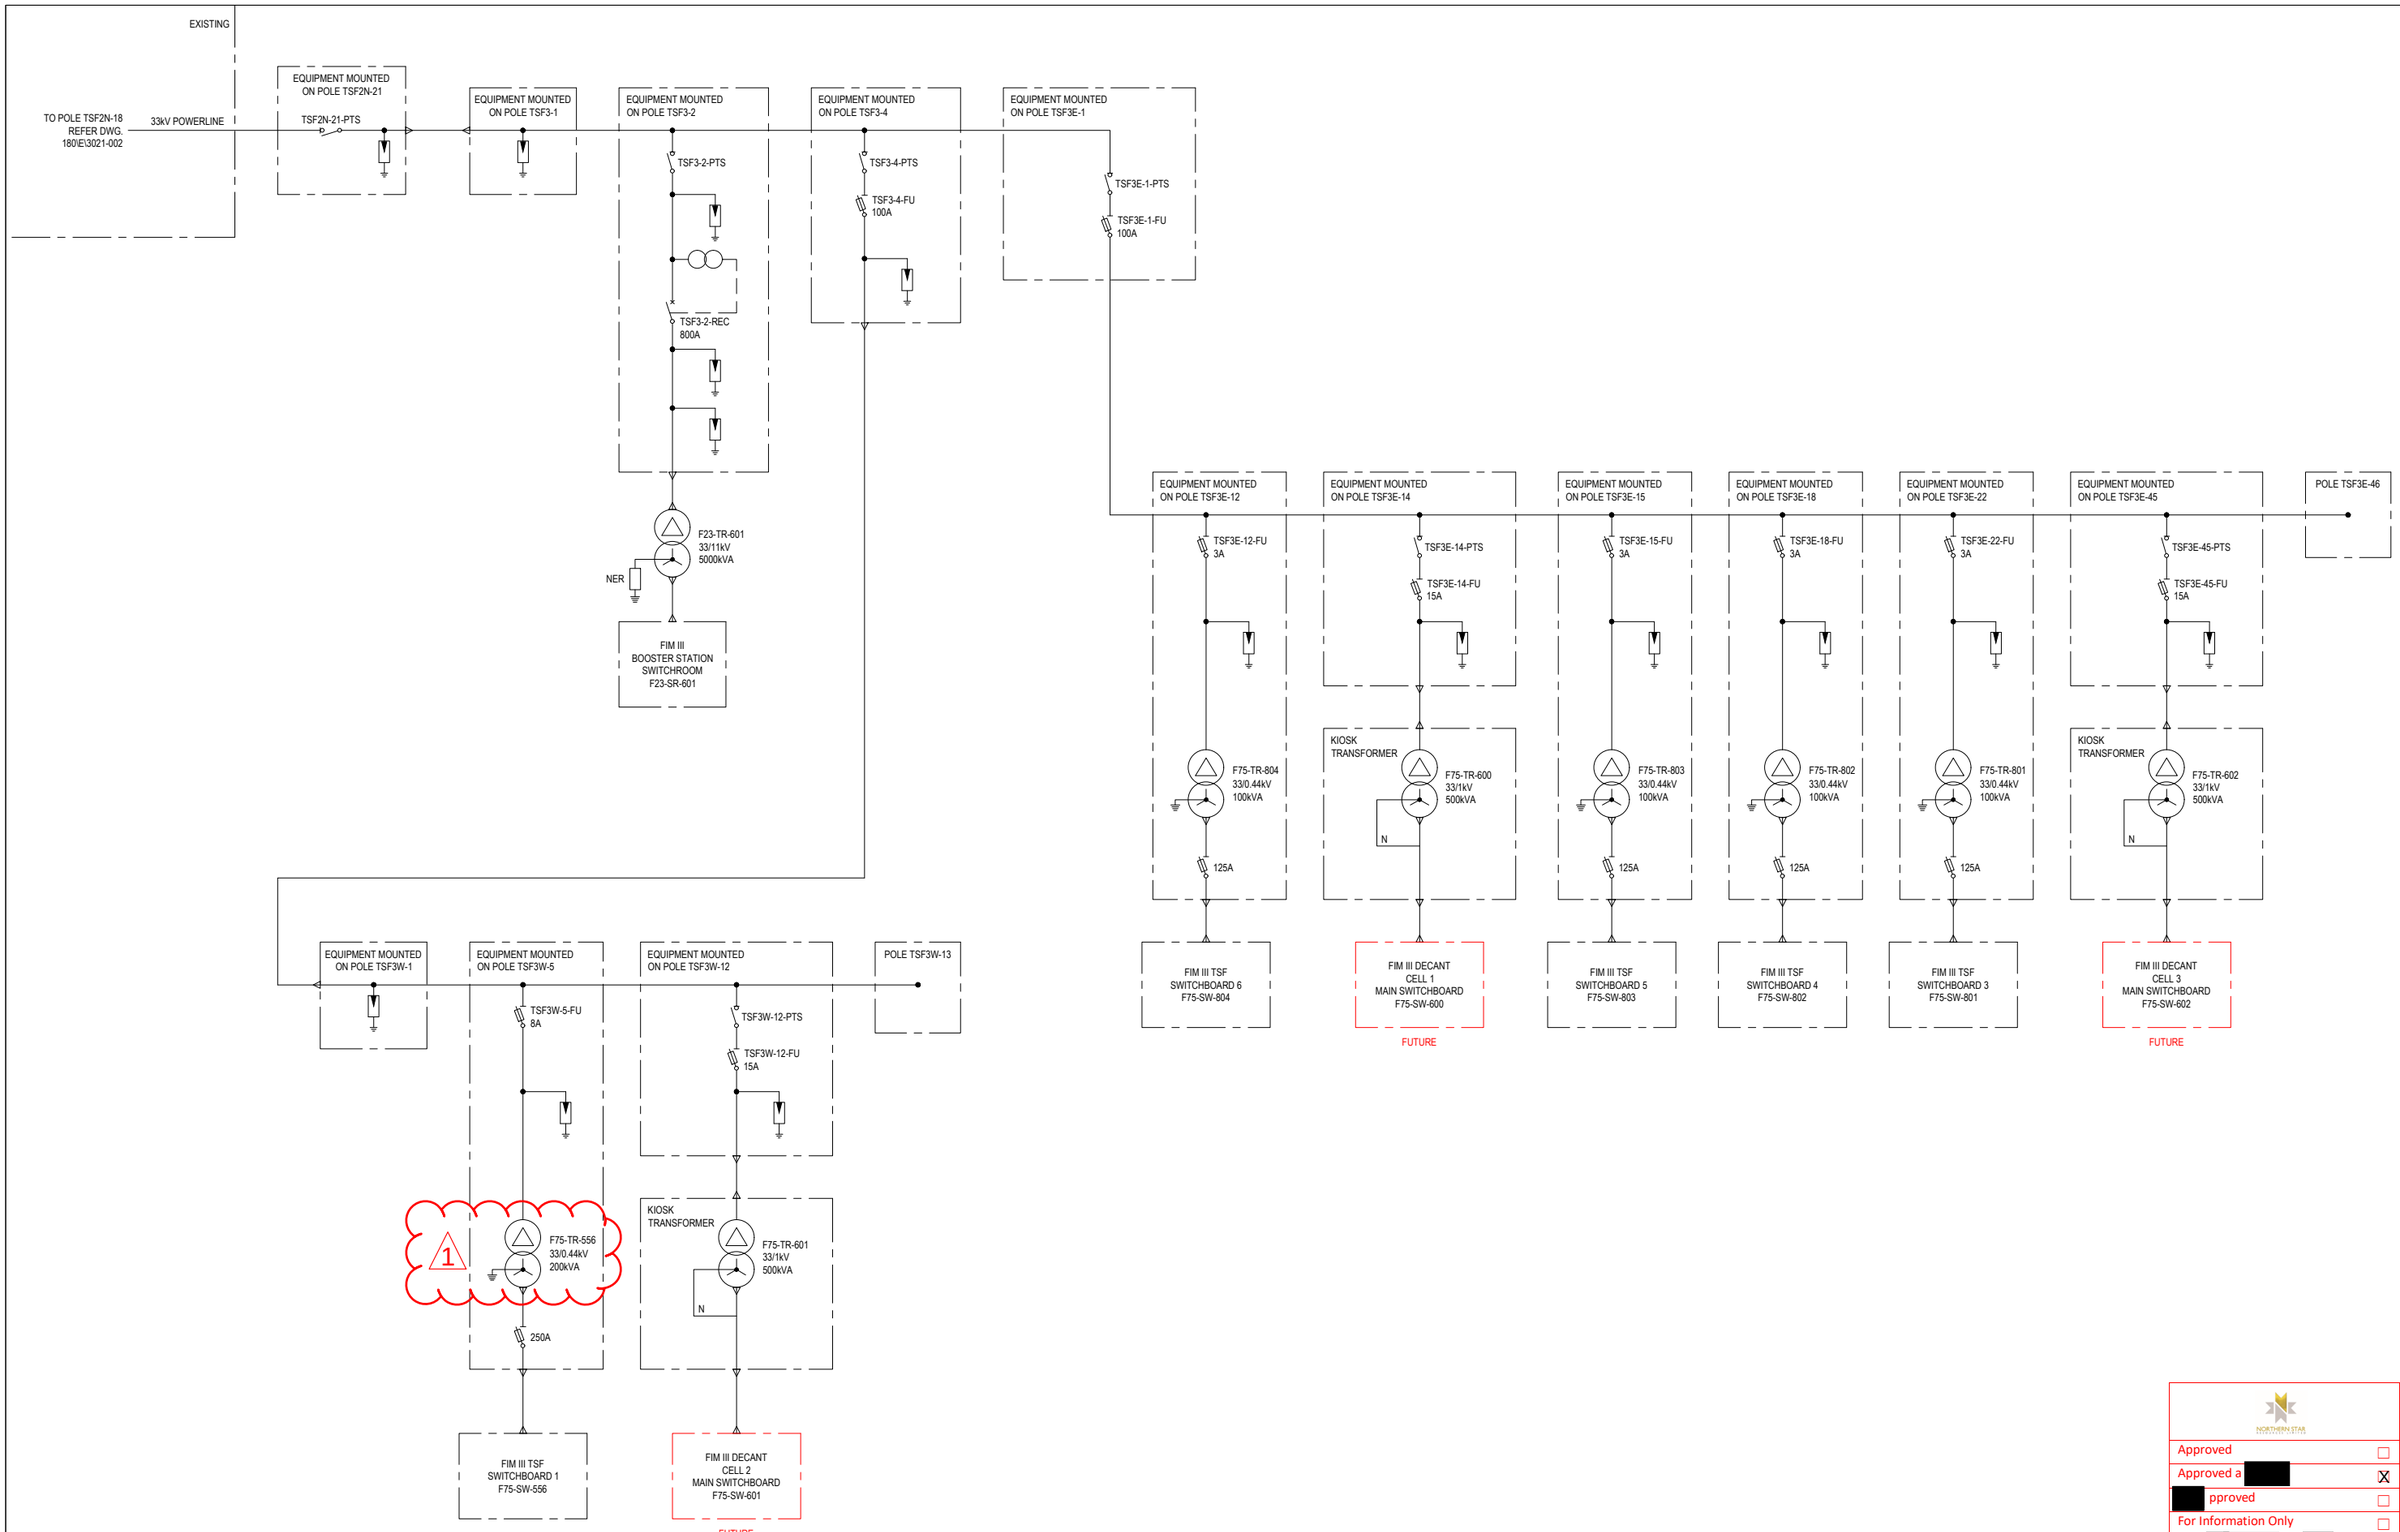


Approved ☐
Approved a[redacted] X
[redacted]pproved ☐
For Information Only ☐
Signed [redacted] 3/08/25
ACCEPTANC[redacted] OT RELIEVE THE SUPPLIER / CONTRACTOR [redacted]ESPONSIBILITY OR LIABILITIES UNDER THE PURCHASE ORDER / CONTRACT

COPYRIGHT ©
This drawing remains the property of Northern Star Resources and may not be copied in any way without prior written approval from this company.

NORTHERN STAR RESOURCES LIMITED

MK	DATE	REVISION	BY	APP
1	04.08.25	TRANSFORMER ON POLE TSF3W-5 RENAMED	[redacted]	
0	21.02.25	ISSUED FOR CONSTRUCTION		

REFERENCE DRAWINGS
DWG NO.

SCALE	NTS	
DRAWN	[redacted]	02.10.24
DESIGNED		21.02.2025
CHECKED		21.02.2025
APPROVED	R. DI FILIPPO	21.02.2025
PROJ.APP		
PROJ. FILE #.		

SITEWIDE POWER & COMMUNICATIONS
HIGH VOLTAGE DISTRIBUTION
FIM III TSF
SINGLE LINE DIAGRAM

SIZE	DRAWING NUMBER	REV
A1	2000-T03-SLD-EL-41001	1

KALGOORLIE CONSOLIDATED GOLD MINES OPERATIONS