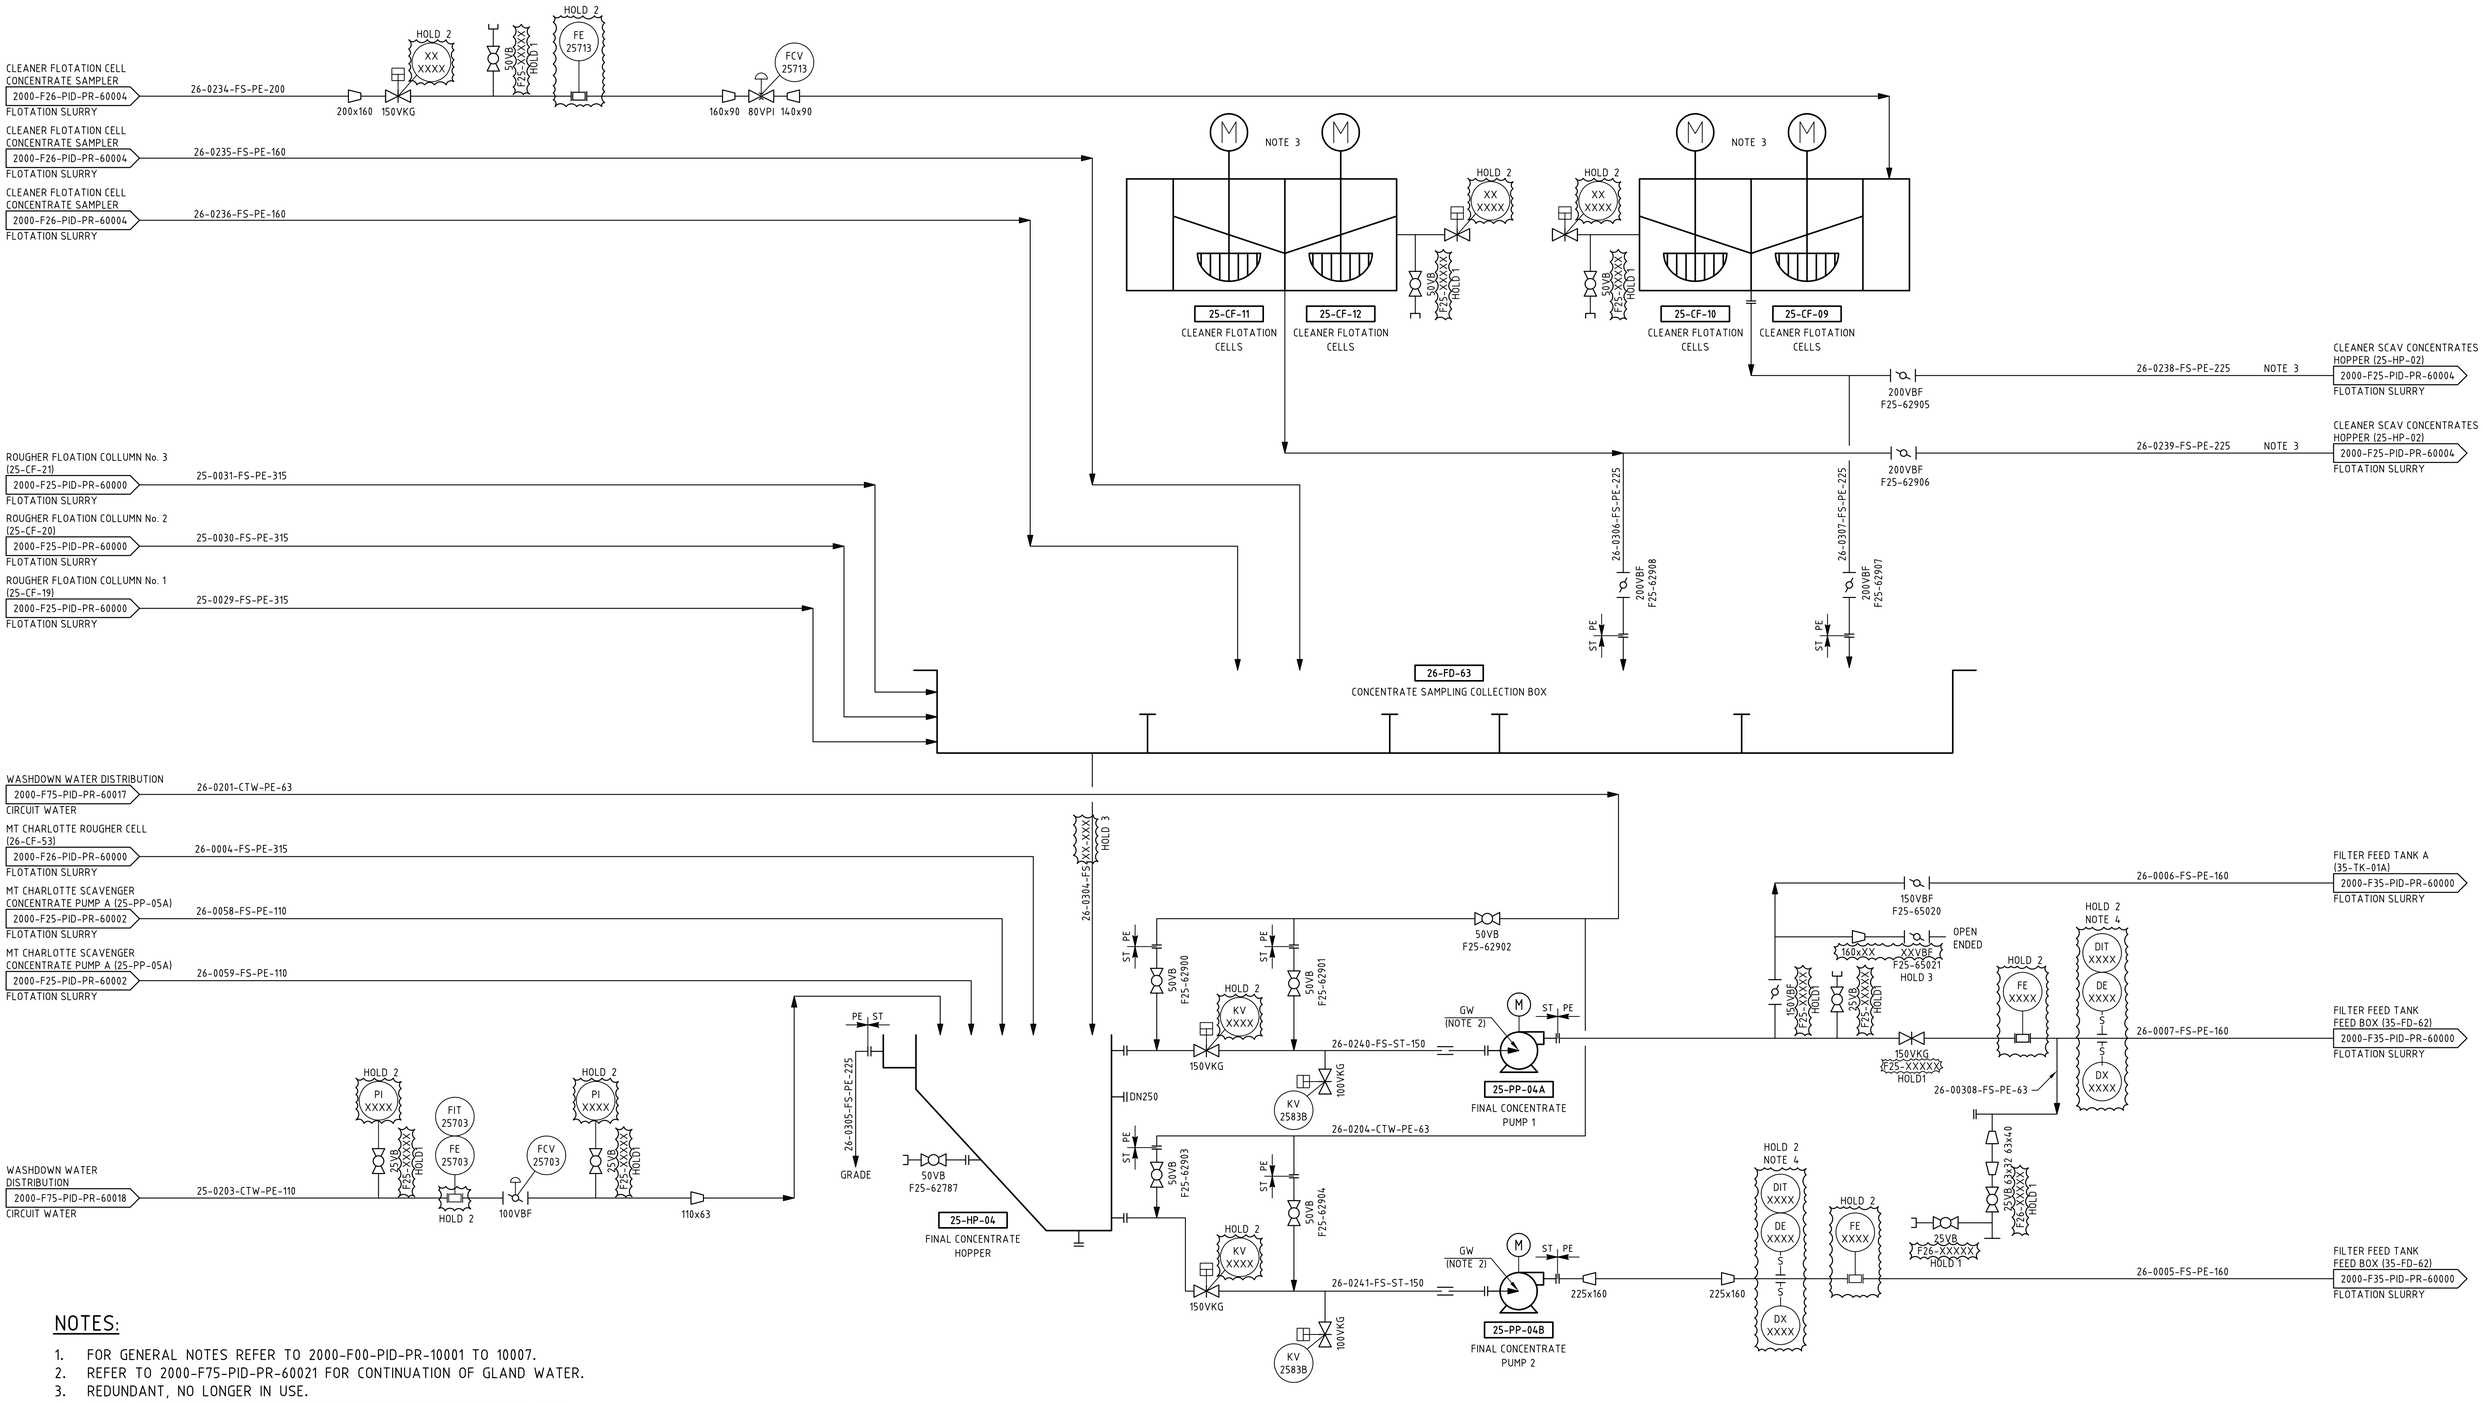


NOTES:

1. FOR GENERAL NOTES REFER TO 2000-F00-PID-PR-10001 TO 10007.
2. REFER TO 2000-F75-PID-PR-60021 FOR CONTINUATION OF GLAND WATER.
3. REDUNDANT, NO LONGER IN USE.
4. THESE DENSITY METERS ARE PHYSICALLY LOCATED IN AREA 35, BUT SHOWN HERE FOR P&ID CLARITY.
5. PROCESS CONTROL SYSTEM CONNECTIONS NOT SHOWN, OR WHERE SHOWN NOT CONFIRMED.

HOLDS:

1. PENDING VALVE TAGGING.
2. CLIENT TO CONFIRM INSTRUMENT TYPE AND/OR TAG NUMBER. NOT SIGHTED IN THE FIELD.
3. DETAILS NOT CONFIRMED DURING AS BUILT WALK. TBC AT SITE.

ORIGINAL DRAWING: 26-PI-0015