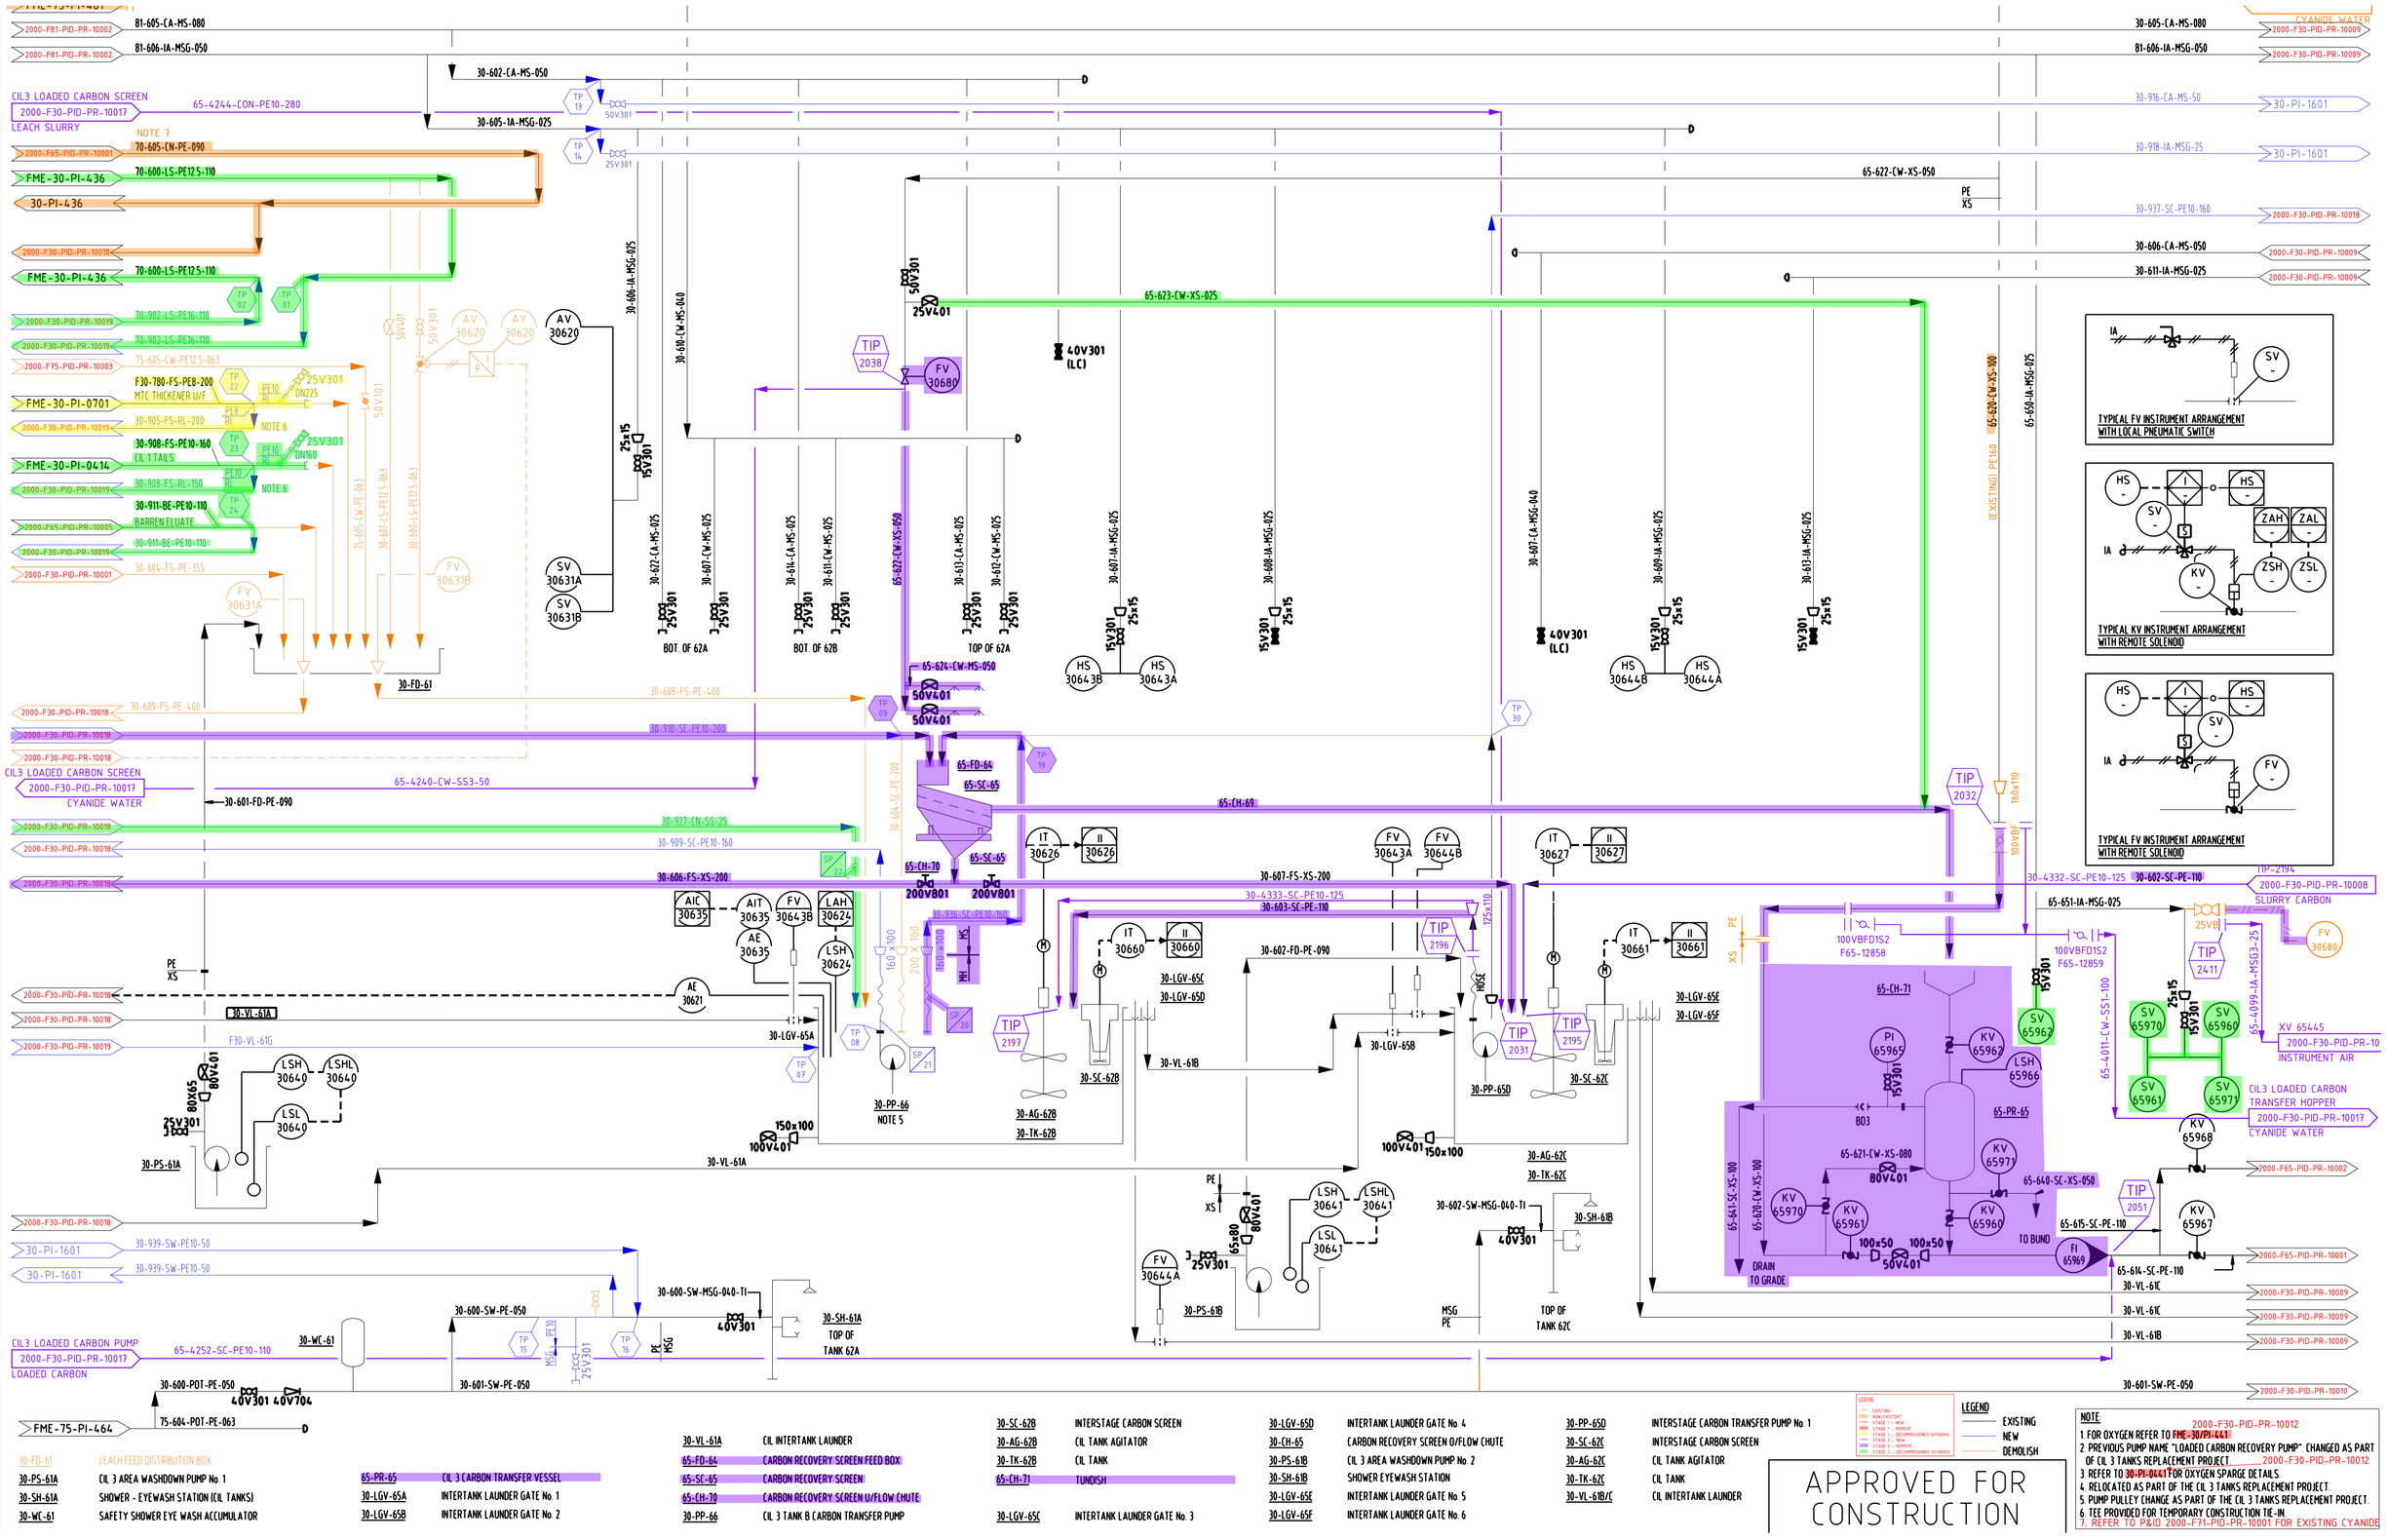


30-FD-61	LEACH FEED DISTRIBUTION BOX	30-VL-61A	CIL INTERTANK LAUNDER	30-SC-62B	INTERSTAGE CARBON SCREEN	30-LGV-65D	INTERTANK LAUNDER GATE No. 4
30-PS-61A	CIL 3 AREA WASHDOWN PUMP No. 1	65-FD-64	CARBON RECOVERY SCREEN FEED BOX	30-AG-62B	CIL TANK AGITATOR	30-CH-65	CARBON RECOVERY SCREEN D/FLOW CHUTE
30-SH-61A	SHOWER - EYEWASH STATION (CIL TANKS)	65-SC-65	CARBON RECOVERY SCREEN	30-TK-62B	CIL TANK	30-PS-61B	CIL 3 AREA WASHDOWN PUMP No. 2
30-WC-61	SAFETY SHOWER EYE WASH ACCUMULATOR	65-CH-70	CARBON RECOVERY SCREEN U/FLOW CHUTE	65-CH-71	TUNDISH	30-SH-61B	SHOWER EYEWASH STATION
65-PR-65	CIL 3 CARBON TRANSFER VESSEL	30-PP-66	CIL 3 TANK B CARBON TRANSFER PUMP			30-LGV-65E	INTERTANK LAUNDER GATE No. 5
30-LGV-65A	INTERTANK LAUNDER GATE No. 1			30-LGV-65C	INTERTANK LAUNDER GATE No. 3	30-LGV-65F	INTERTANK LAUNDER GATE No. 6
30-LGV-65B	INTERTANK LAUNDER GATE No. 2						

30-PP-65D	INTERSTAGE CARBON TRANSFER PUMP No. 1	LEGEND	
30-SC-62C	INTERSTAGE CARBON SCREEN		EXISTING
30-AG-62C	CIL TANK AGITATOR		NEW
30-TK-62C	CIL TANK		DEMOLISH
30-VL-61B/C	CIL INTERTANK LAUNDER		

APPROVED FOR CONSTRUCTION

NOTE:
1. FOR OXYGEN REFER TO FME-30-PI-441
2. PREVIOUS PUMP NAME "LOADED CARBON RECOVERY PUMP" CHANGED AS PART OF CIL 3 TANKS REPLACEMENT PROJECT.
3. REFER TO 30-PI-0441 FOR OXYGEN SPARGE DETAILS.
4. RELOCATED AS PART OF THE CIL 3 TANKS REPLACEMENT PROJECT.
5. PUMP PULLEY CHANGE AS PART OF THE CIL 3 TANKS REPLACEMENT PROJECT.
6. TEE PROVIDED FOR TEMPORARY CONSTRUCTION TIE-IN
7. REFER TO P&ID 2000-F71-PID-PR-10001 FOR EXISTING CYANIDE

2000-F30-PID-PR-10012