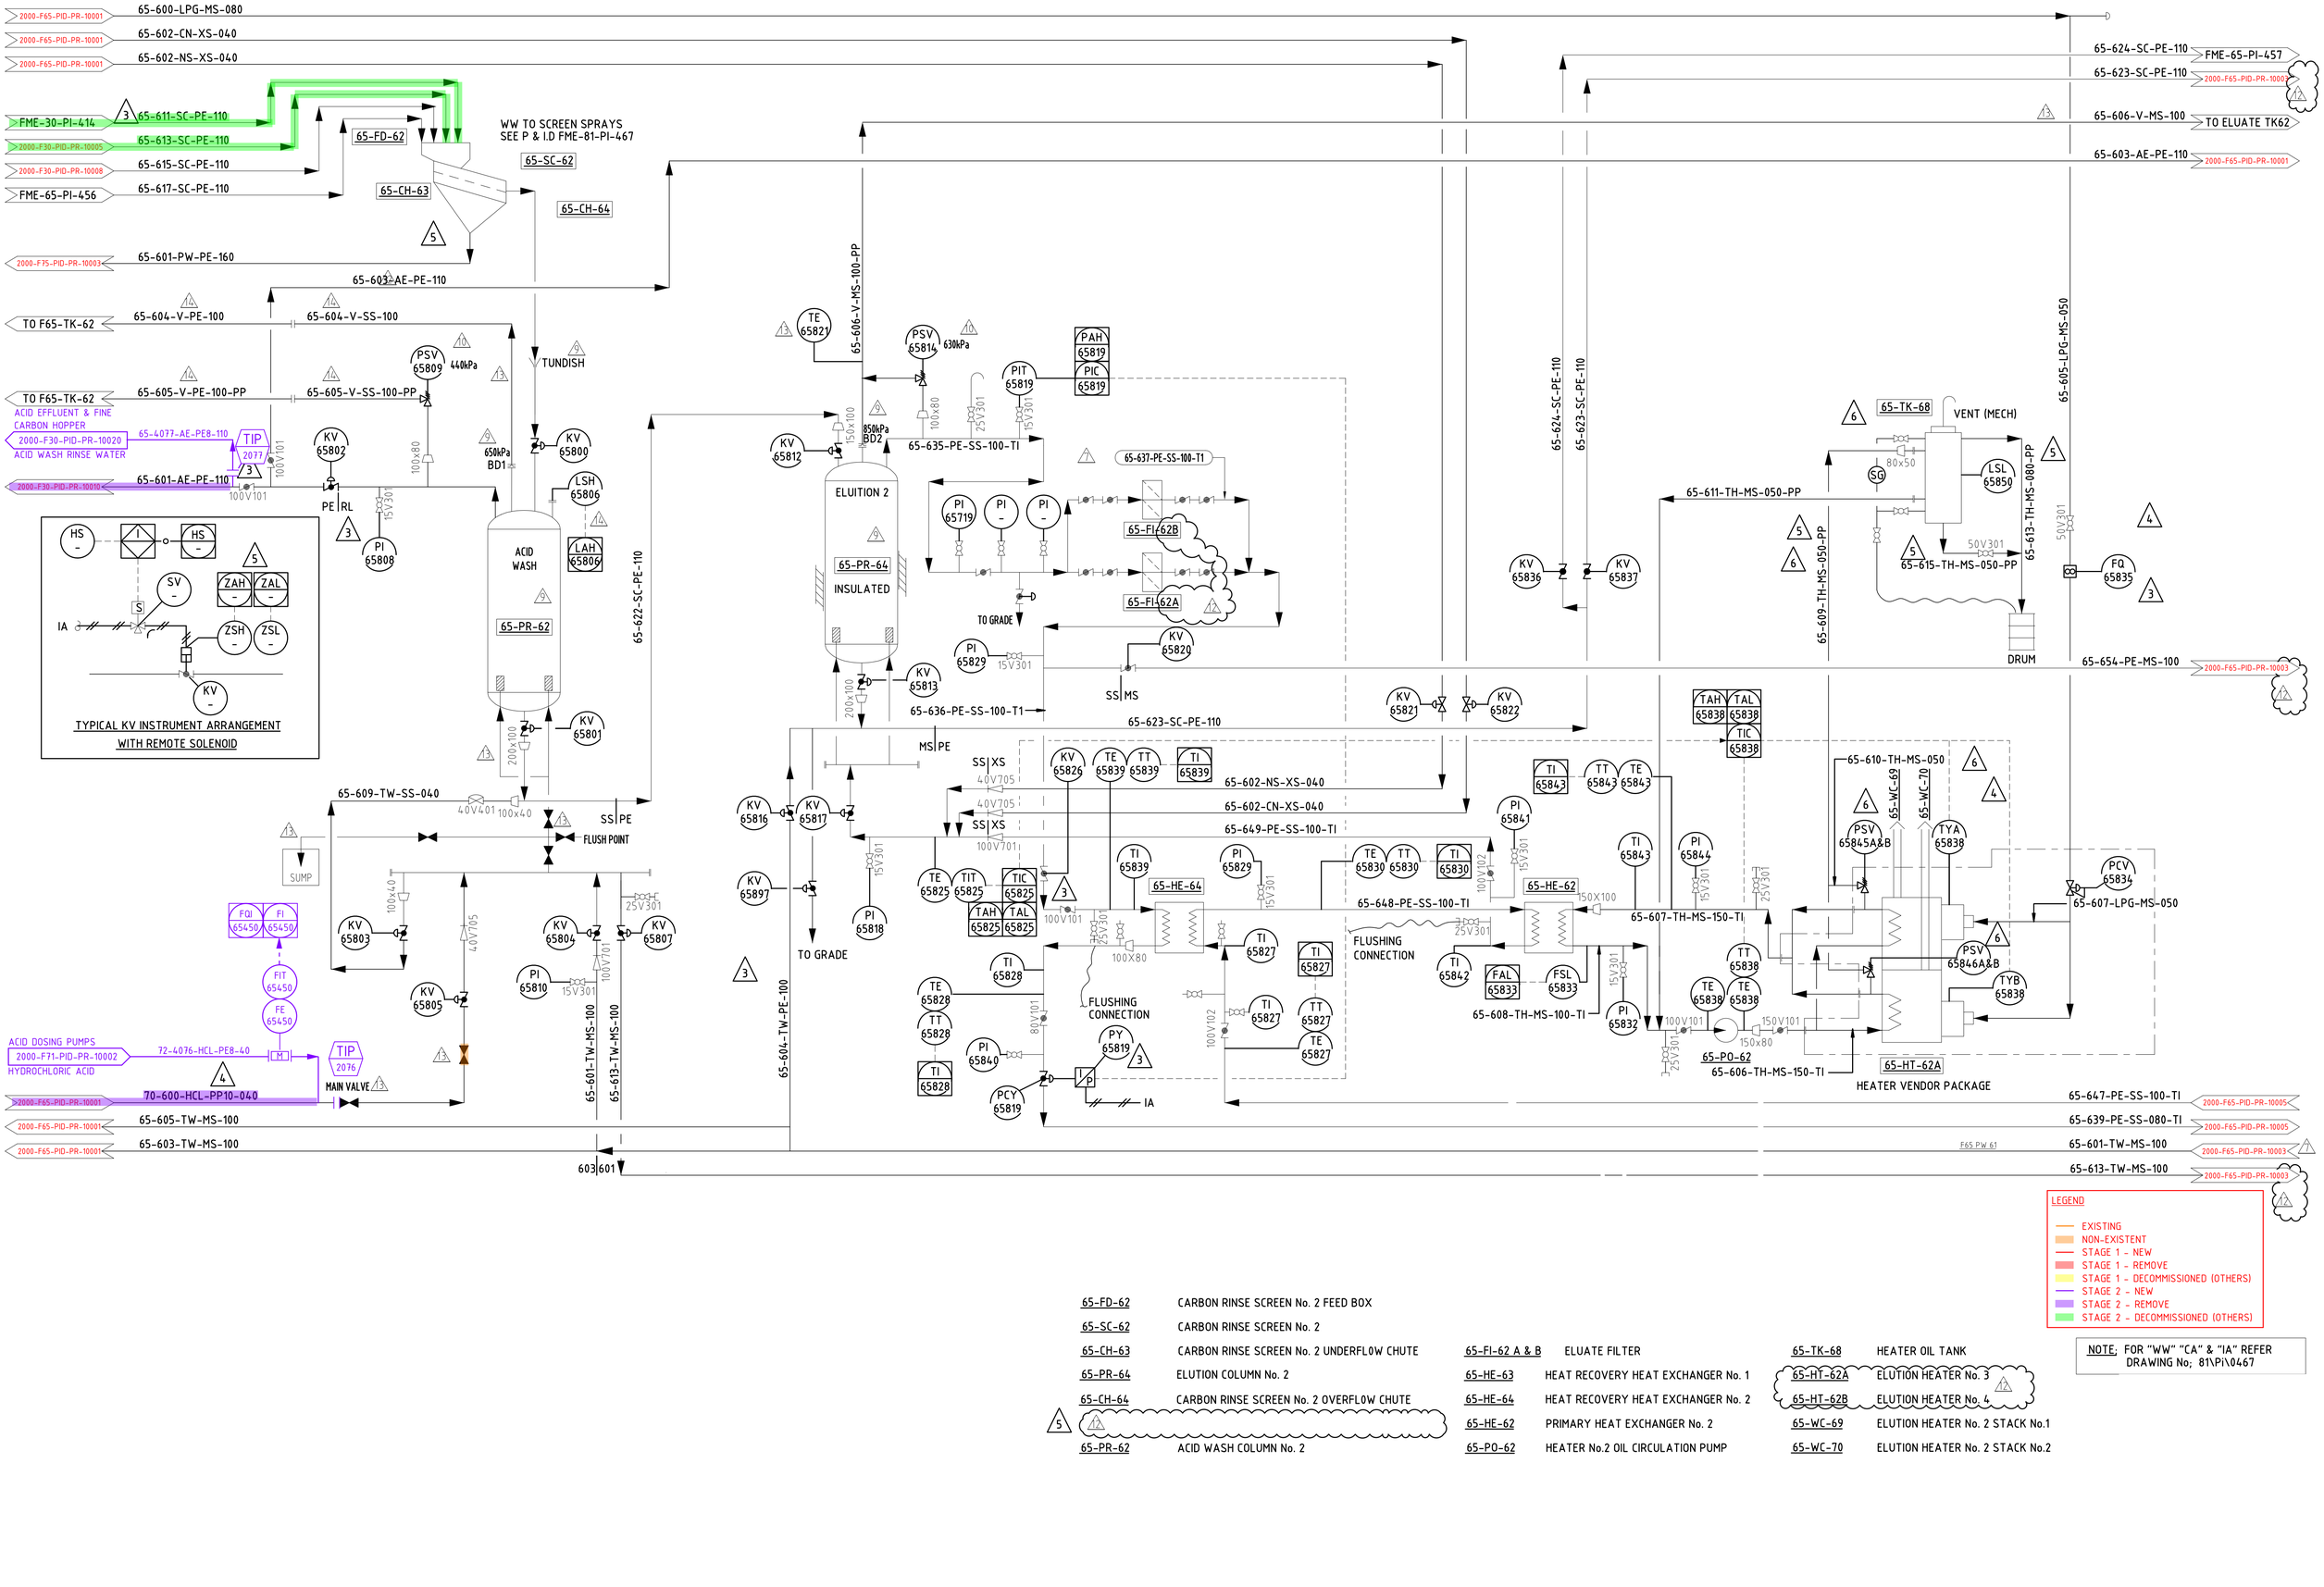


65-FD-62	CARBON RINSE SCREEN No. 2 FEED BOX	65-FI-62 A & B	ELUATE FILTER	65-TK-68	HEATER OIL TANK
65-SC-62	CARBON RINSE SCREEN No. 2	65-HE-63	HEAT RECOVERY HEAT EXCHANGER No. 1	65-HT-62A	ELUTION HEATER No. 3
65-CH-63	CARBON RINSE SCREEN No. 2 UNDERFLOW CHUTE	65-HE-64	HEAT RECOVERY HEAT EXCHANGER No. 2	65-HT-62B	ELUTION HEATER No. 4
65-PR-64	ELUTION COLUMN No. 2	65-HE-62	PRIMARY HEAT EXCHANGER No. 2	65-WC-69	ELUTION HEATER No. 2 STACK No.1
65-CH-64	CARBON RINSE SCREEN No. 2 OVERFLOW CHUTE	65-PO-62	HEATER No.2 OIL CIRCULATION PUMP	65-WC-70	ELUTION HEATER No. 2 STACK No.2
65-PR-62	ACID WASH COLUMN No. 2				

LEGEND
- EXISTING
- NON-EXISTENT
- STAGE 1 - NEW
- STAGE 1 - REMOVE
- STAGE 1 - DECOMMISSIONED (OTHERS)
- STAGE 2 - NEW
- STAGE 2 - REMOVE
- STAGE 2 - DECOMMISSIONED (OTHERS)

NOTE; FOR "WW" "CA" & "IA" REFER DRAWING No; 81\PI\0467