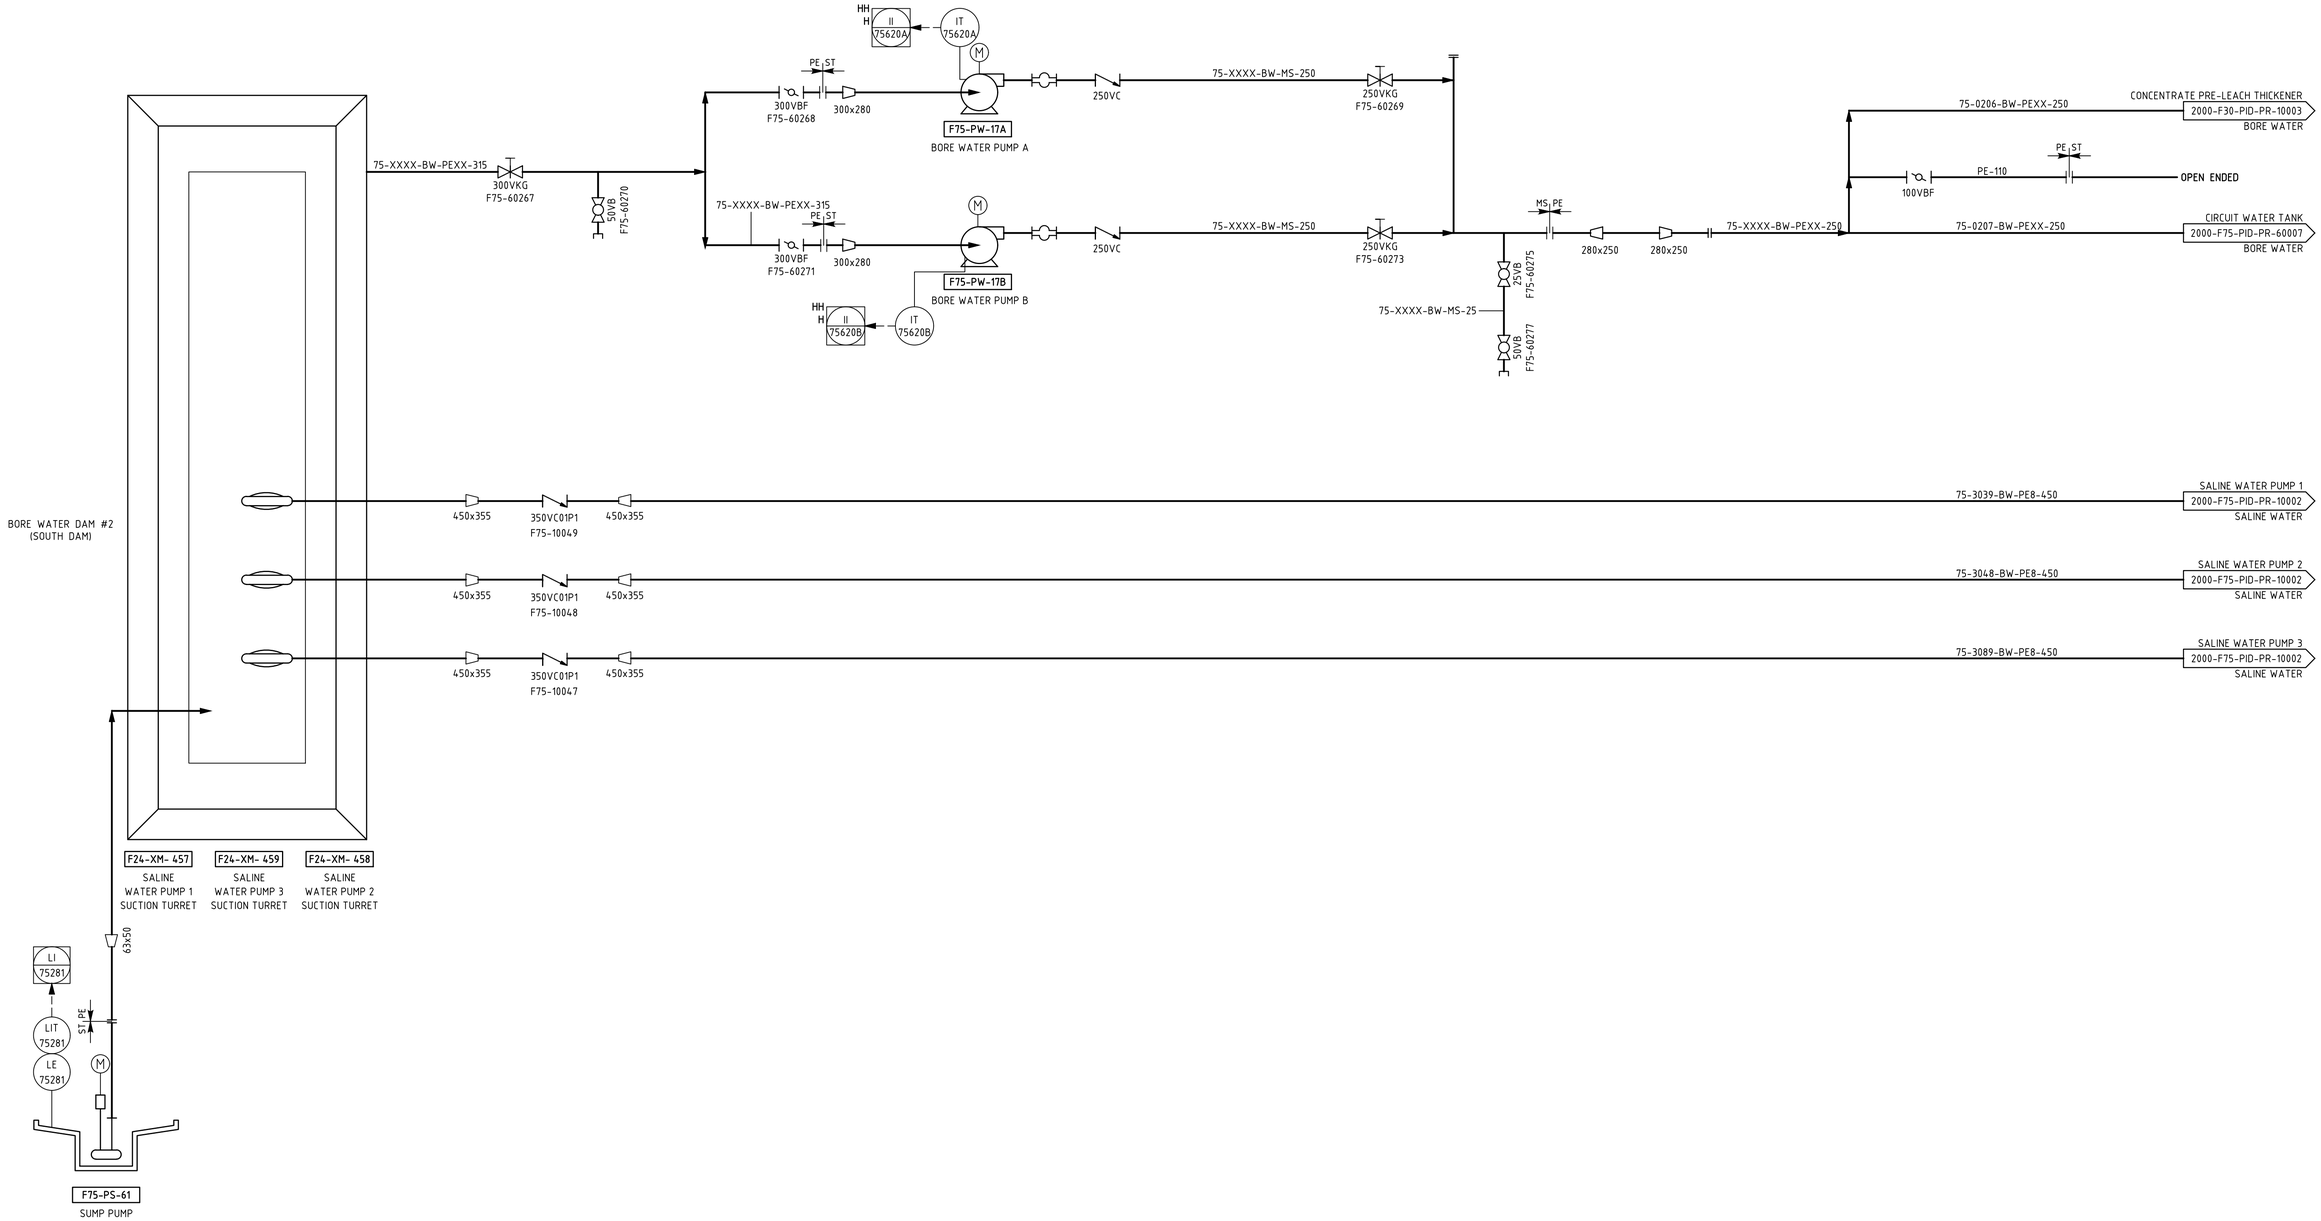

HH
H
II
75620A
IT
75620A
M
PE
ST
300VBF
F75-60268
300x280
F75-PW-17A
BORE WATER PUMP A
250VC
75-XXXX-BW-MS-250
250VKG
F75-60269
75-XXXX-BW-PEXX-315
300VKG
F75-60267
50VB
F75-60270
75-XXXX-BW-PEXX-315
300VBF
F75-60271
300x280
F75-PW-17B
BORE WATER PUMP B
250VC
75-XXXX-BW-MS-250
250VKG
F75-60273
MS
PE
280x250
280x250
75-XXXX-BW-PEXX-250
75-0206-BW-PEXX-250
CONCENTRATE PRE-LEACH THICKENER
2000-F30-PID-PR-10003
BORE WATER
PE-110
100VBF
OPEN ENDED
75-0207-BW-PEXX-250
CIRCUIT WATER TANK
2000-F75-PID-PR-60007
BORE WATER
25VB
F75-60275
75-XXXX-BW-MS-25
50VB
F75-60277
HH
H
II
75620B
IT
75620B
BORE WATER DAM #2
(SOUTH DAM)
450x355
350VC01P1
F75-10049
450x355
75-3039-BW-PE8-450
SALINE WATER PUMP 1
2000-F75-PID-PR-10002
SALINE WATER
450x355
350VC01P1
F75-10048
450x355
75-3048-BW-PE8-450
SALINE WATER PUMP 2
2000-F75-PID-PR-10002
SALINE WATER
450x355
350VC01P1
F75-10047
450x355
75-3089-BW-PE8-450
SALINE WATER PUMP 3
2000-F75-PID-PR-10002
SALINE WATER
F24-XM- 457
SALINE
WATER PUMP 1
SUCTION TURRET
F24-XM- 459
SALINE
WATER PUMP 3
SUCTION TURRET
F24-XM- 458
SALINE
WATER PUMP 2
SUCTION TURRET
63x50
LI
75281
LIT
75281
PE
ST
LE
75281
M
F75-PS-61
SUMP PUMP