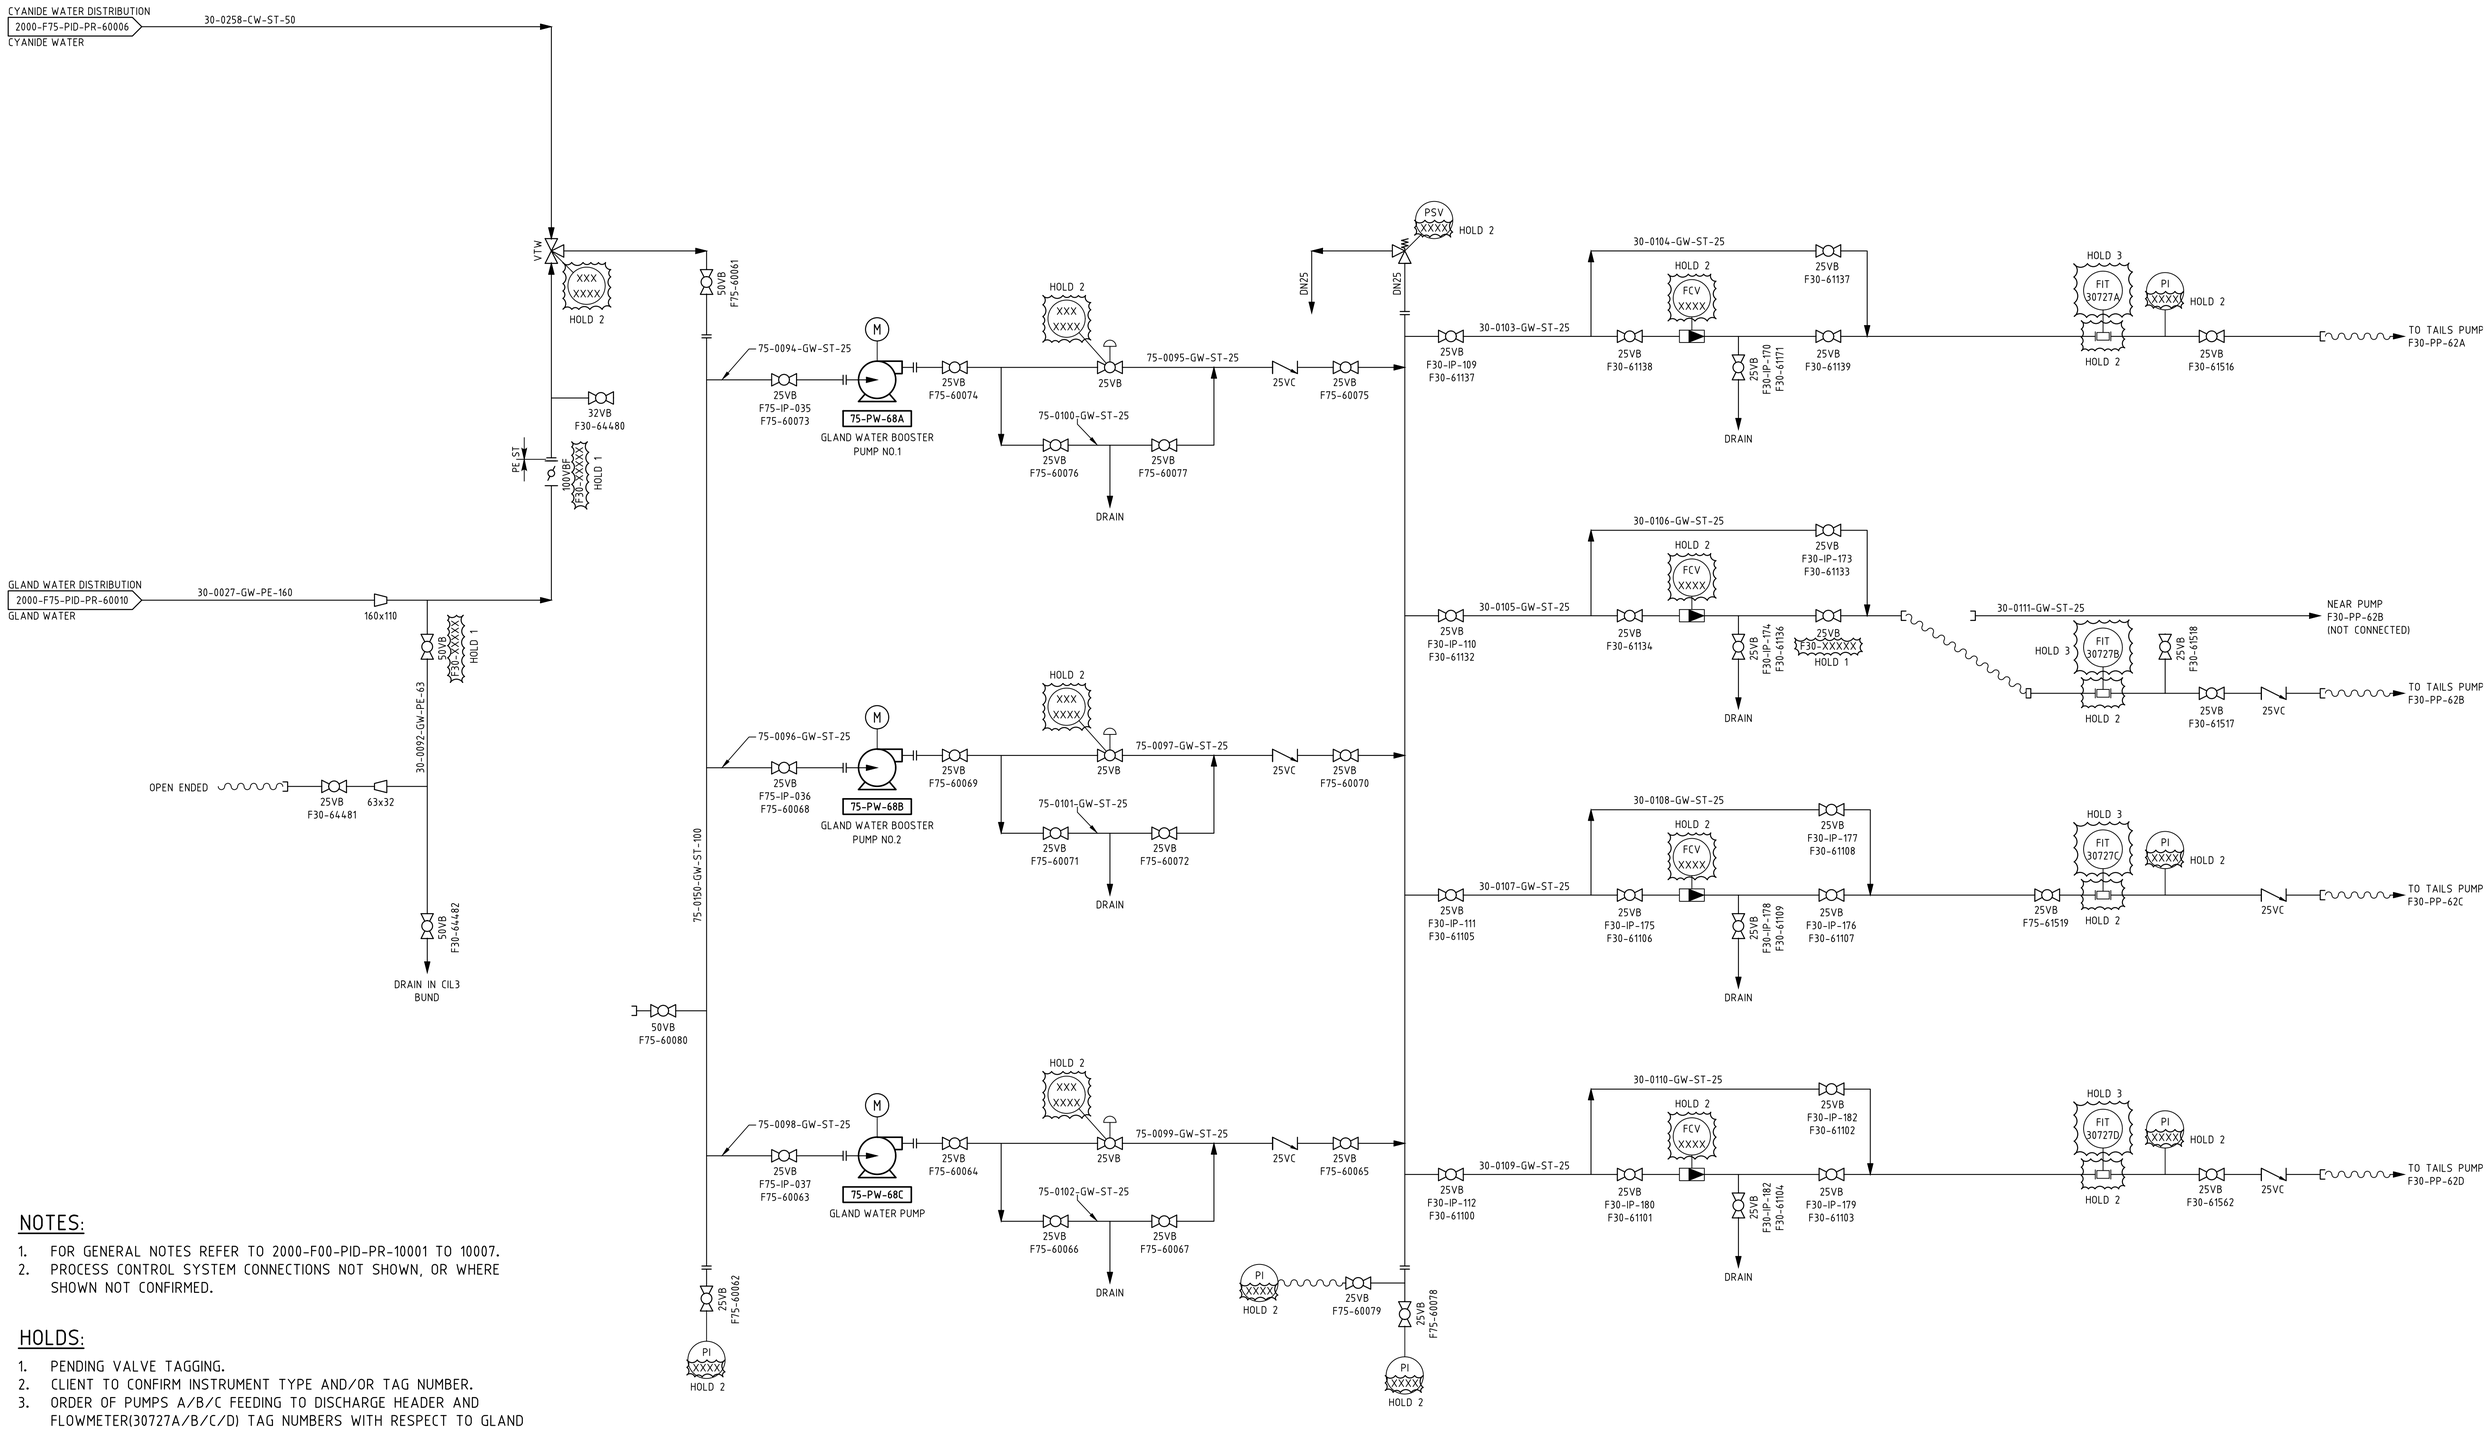


NOTES:

1. FOR GENERAL NOTES REFER TO 2000-F00-PID-PR-10001 TO 10007.
2. PROCESS CONTROL SYSTEM CONNECTIONS NOT SHOWN, OR WHERE SHOWN NOT CONFIRMED.

HOLDS:

1. PENDING VALVE TAGGING.
2. CLIENT TO CONFIRM INSTRUMENT TYPE AND/OR TAG NUMBER.
3. ORDER OF PUMPS A/B/C FEEDING TO DISCHARGE HEADER AND FLOWMETER(30727A/B/C/D) TAG NUMBERS WITH RESPECT TO GLAND WATER FEED LINE TO VARIOUS TAILS PUMPS CANNOT BE CONFIRMED IN ABSENCE OF EQUIPMENT OR FLOWMETER TAGS AT SITE. PUMP NUMBERS AND FLOWMETER TAG NUMBERS INDICATED ON THIS P&ID ARE BASED ON ASSUMPTION THAT ORIGINAL P&ID IS CORRECT - TBC BY CLIENT.

ORIGINAL DRAWING: FME-30-PI-0440

ORIGINAL DRAWING: FME-30-PI-1011