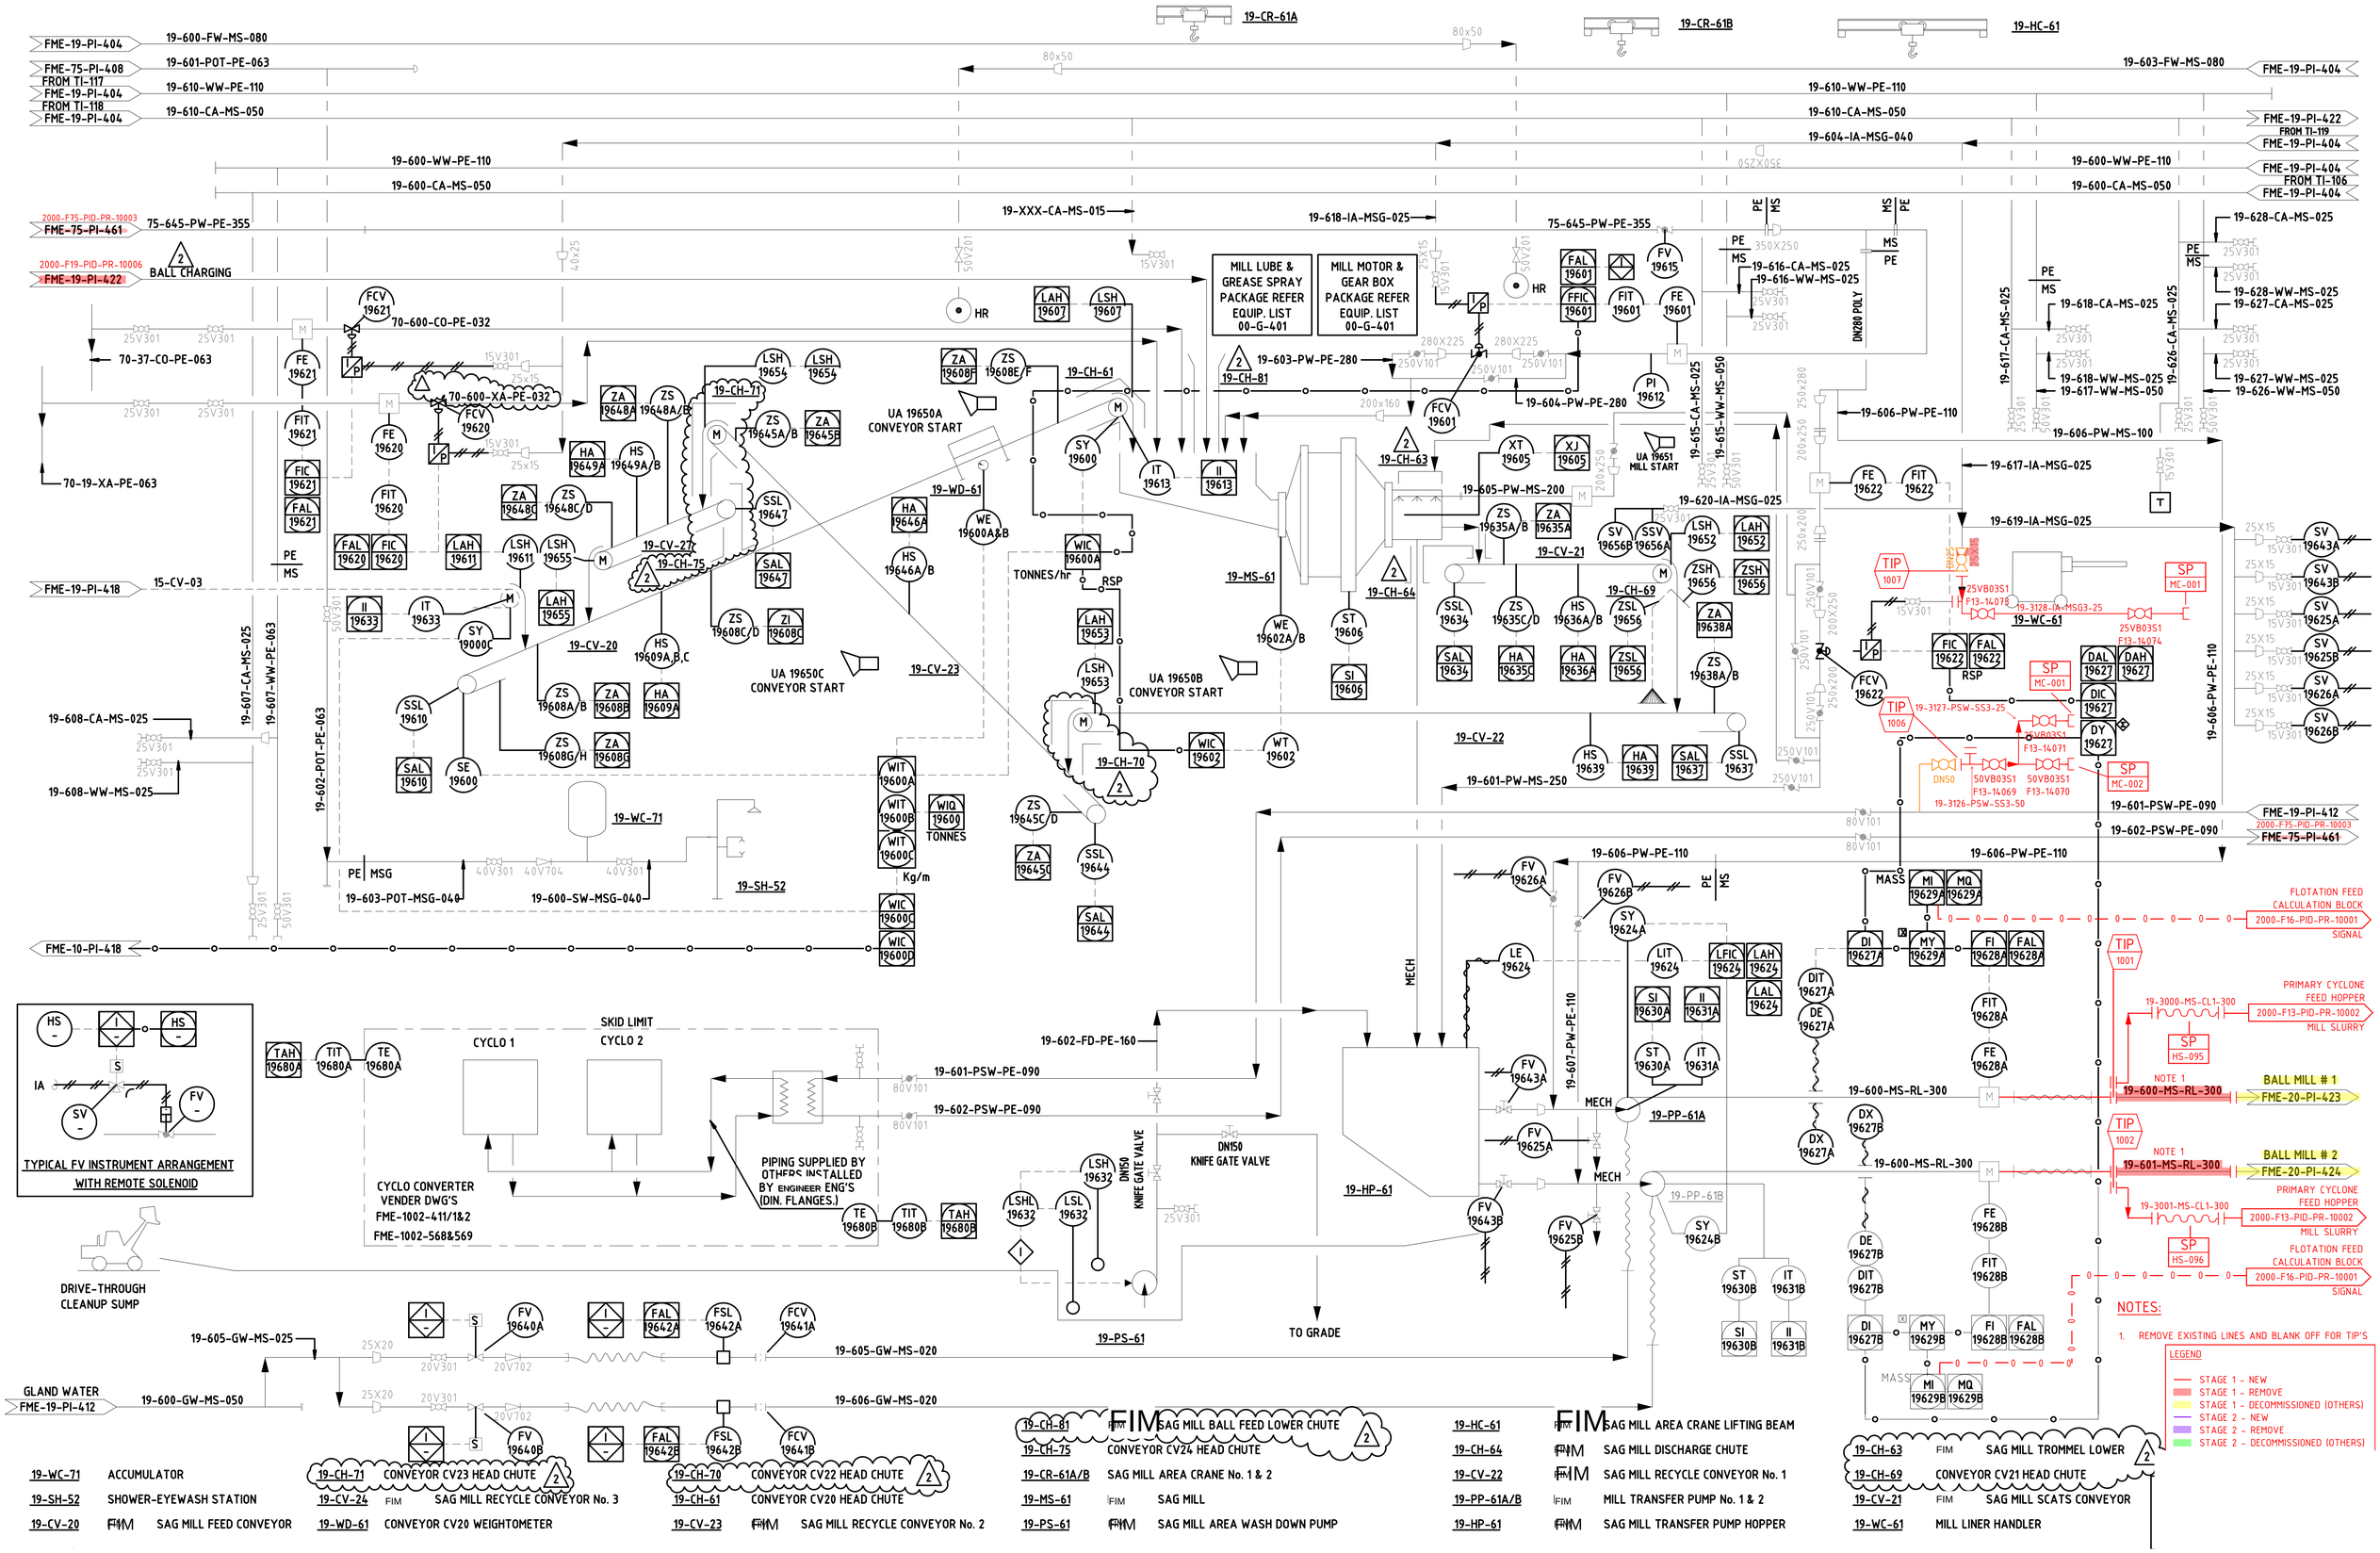

19-CR-61A
19-CR-61B
19-HC-61
FME-19-PI-404
19-600-FW-MS-080
FME-75-PI-408
FROM TI-117
19-601-POT-PE-063
FME-19-PI-404
FROM TI-118
19-610-WW-PE-110
FME-19-PI-404
19-610-CA-MS-050
19-603-FW-MS-080
FME-19-PI-404
19-610-WW-PE-110
19-610-CA-MS-050
FME-19-PI-422
FROM TI-119
FME-19-PI-404
19-604-IA-MSG-040
19-600-WW-PE-110
19-600-CA-MS-050
19-600-WW-PE-110
FME-19-PI-404
FROM TI-106
19-600-CA-MS-050
FME-19-PI-404
2000-F15-PID-PR-10003
FME-75-PI-461
75-645-PW-PE-355
19-XXX-CA-MS-015
19-618-IA-MSG-025
75-645-PW-PE-355
2000-F19-PID-PR-10006
FME-19-PI-422
BALL CHARGING
MILL LUBE & GREASE SPRAY PACKAGE REFER EQUIP. LIST 00-G-401
MILL MOTOR & GEAR BOX PACKAGE REFER EQUIP. LIST 00-G-401
19-603-PW-PE-280
19-CH-81
19-604-PW-PE-280
19-606-PW-PE-110
19-606-PW-MS-100
19-617-IA-MSG-025
19-620-IA-MSG-025
19-619-IA-MSG-025
19-628-CA-MS-025
19-628-WW-MS-025
19-627-CA-MS-025
19-627-WW-MS-025
19-626-CA-MS-025
19-626-WW-MS-050
19-618-CA-MS-025
19-618-WW-MS-025
19-617-WW-MS-050
19-617-CA-MS-025
19-616-CA-MS-025
19-616-WW-MS-025
DN200 POLY
70-37-CO-PE-063
70-19-XA-PE-063
70-600-CO-PE-032
70-600-XA-PE-032
19-CH-71
19-CH-61
UA 19650A CONVEYOR START
19-WD-61
19-MS-61
UA 19651 MILL START
19-615-CA-MS-025
19-615-WW-MS-050
19-605-PW-MS-200
19-CV-21
19-CH-63
19-CH-64
19-CH-69
19-CV-22
19-601-PW-MS-250
FME-19-PI-418
15-CV-03
19-CV-27
19-CH-75
19-CV-20
19-CV-23
UA 19650C CONVEYOR START
UA 19650B CONVEYOR START
TONNES/hr
RSP
19-CH-70
19-WC-61
19-3128-IA-MSG3-25
19-3127-PSW-SS3-25
19-3126-PSW-SS3-50
19-601-PSW-PE-090
19-602-PSW-PE-090
19-606-PW-PE-110
19-607-CA-MS-025
19-607-WW-PE-063
19-602-POT-PE-063
19-608-CA-MS-025
19-608-WW-MS-025
19-WC-71
19-SH-52
19-603-POT-MSG-040
19-600-SW-MSG-040
WIT 19600A
WIT 19600B
WIT 19600C
WIQ 19600 TONNES
Kg/m
WIC 19600C
WIC 19600D
FME-10-PI-418
19-602-FD-PE-160
19-601-PSW-PE-090
19-602-PSW-PE-090
SKID LIMIT
CYCLO 1
CYCLO 2
CYCLO CONVERTER VENDER DWG'S
FME-1002-411/1&2
FME-1002-568&569
PIPING SUPPLIED BY OTHERS INSTALLED BY ENGINEER ENG'S (DIN. FLANGES.)
DN150 KNIFE GATE VALVE
19-HP-61
19-PS-61
19-PP-61A
19-PP-61B
MECH
TO GRADE
19-607-PW-PE-110
TYPICAL FV INSTRUMENT ARRANGEMENT WITH REMOTE SOLENOID
DRIVE-THROUGH CLEANUP SUMP
19-605-GW-MS-025
19-605-GW-MS-020
GLAND WATER
FME-19-PI-412
19-600-GW-MS-050
19-606-GW-MS-020
FLOTATION FEED CALCULATION BLOCK
2000-F16-PID-PR-10001
SIGNAL
PRIMARY CYCLONE FEED HOPPER
2000-F13-PID-PR-10002
MILL SLURRY
BALL MILL # 1
FME-20-PI-423
BALL MILL # 2
FME-20-PI-424
NOTES:
1. REMOVE EXISTING LINES AND BLANK OFF FOR TIP'S
LEGEND
STAGE 1 - NEW
STAGE 1 - REMOVE
STAGE 1 - DECOMMISSIONED (OTHERS)
STAGE 2 - NEW
STAGE 2 - REMOVE
STAGE 2 - DECOMMISSIONED (OTHERS)
19-CH-81 FIM SAG MILL BALL FEED LOWER CHUTE
19-CH-75 CONVEYOR CV24 HEAD CHUTE
19-CR-61A/B SAG MILL AREA CRANE No. 1 & 2
19-MS-61 FIM SAG MILL
19-PS-61 FIM SAG MILL AREA WASH DOWN PUMP
19-HP-61 FIM SAG MILL TRANSFER PUMP HOPPER
19-HC-61 FIM SAG MILL AREA CRANE LIFTING BEAM
19-CH-64 FIM SAG MILL DISCHARGE CHUTE
19-CV-22 FIM SAG MILL RECYCLE CONVEYOR No. 1
19-PP-61A/B FIM MILL TRANSFER PUMP No. 1 & 2
19-CH-63 FIM SAG MILL TROMMEL LOWER
19-CH-69 CONVEYOR CV21 HEAD CHUTE
19-CV-21 FIM SAG MILL SCATS CONVEYOR
19-WC-61 MILL LINER HANDLER
19-WC-71 ACCUMULATOR
19-SH-52 SHOWER-EYEWASH STATION
19-CV-20 FIM SAG MILL FEED CONVEYOR
19-CH-71 CONVEYOR CV23 HEAD CHUTE
19-CV-24 FIM SAG MILL RECYCLE CONVEYOR No. 3
19-WD-61 CONVEYOR CV20 WEIGHTOMETER
19-CH-70 CONVEYOR CV22 HEAD CHUTE
19-CH-61 CONVEYOR CV20 HEAD CHUTE
19-CV-23 FIM SAG MILL RECYCLE CONVEYOR No. 2