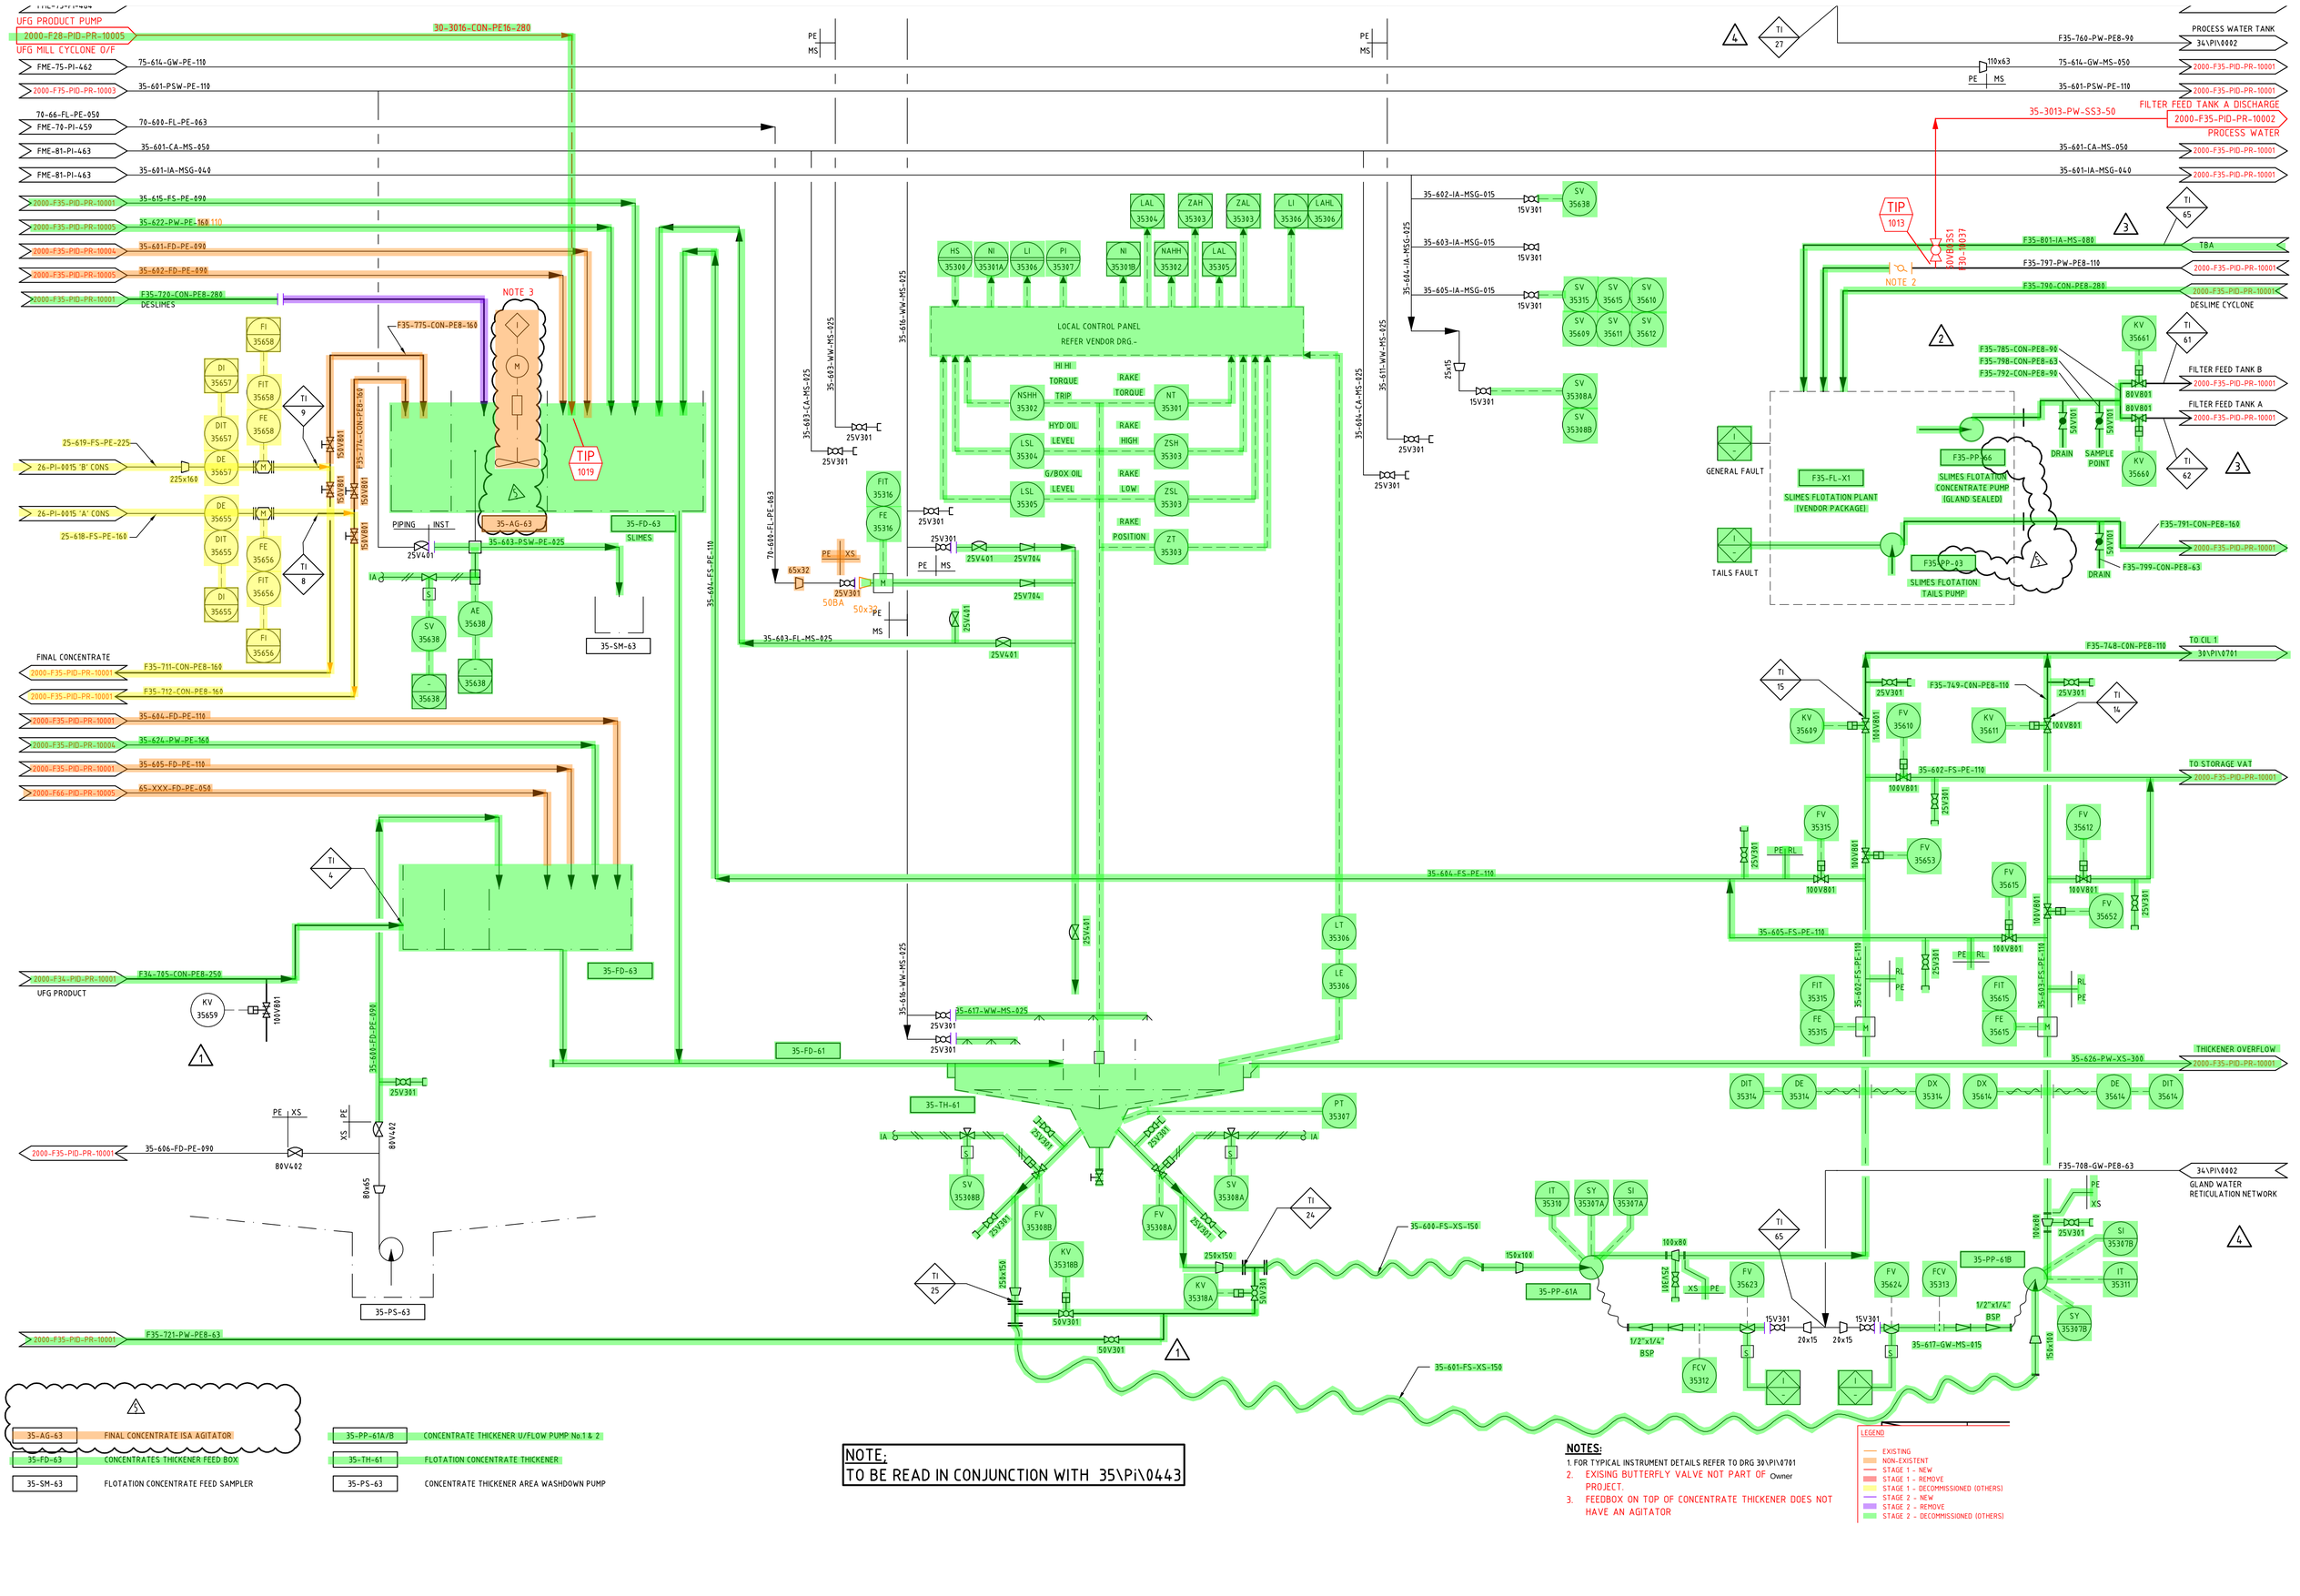

UFG PRODUCT PUMP
2000-F28-PID-PR-10005
UFG MILL CYCLONE O/F
30-3016-CON-PE16-280
FME-75-PI-462
75-614-GW-PE-110
2000-F35-PID-PR-10003
35-601-PSW-PE-110
70-66-FL-PE-050
FME-70-PI-459
70-600-FL-PE-063
FME-81-PI-463
35-601-CA-MS-050
FME-81-PI-463
35-601-IA-MSG-040
2000-F35-PID-PR-10001
35-615-FS-PE-090
2000-F35-PID-PR-10005
35-622-PW-PE-160 110
2000-F35-PID-PR-10004
35-601-FD-PE-090
2000-F35-PID-PR-10005
35-602-FD-PE-090
2000-F35-PID-PR-10001
F35-720-CON-PE8-280
DESLIMES
NOTE 3
F35-775-CON-PE8-160
TIP 1019
25-619-FS-PE-225
26-PI-0015 'B' CONS
225x160
26-PI-0015 'A' CONS
25-618-FS-PE-160
F35-774-CON-PE8-160
PIPING
INST
35-AG-63
35-FD-63
SLIMES
35-603-PSW-PE-025
35-SM-63
35-614-FS-PE-110
FINAL CONCENTRATE
F35-711-CON-PE8-160
F35-712-CON-PE8-160
35-604-FD-PE-110
35-624-PW-PE-160
35-605-FD-PE-110
65-XXX-FD-PE-050
2000-F34-PID-PR-10001
F34-705-CON-PE8-250
UFG PRODUCT
35-603-FD-PE-090
35-606-FD-PE-090
35-PS-63
2000-F35-PID-PR-10001
F35-721-PW-PE8-63
35-603-CA-MS-025
35-603-WW-MS-025
25V301
35-616-WW-MS-025
35-617-WW-MS-025
35-618-WW-MS-025
35-TH-61
35-FD-61
70-600-FL-PE-063
35-603-FL-MS-025
25V401
25V704
25V491
35-611-WW-MS-025
35-604-CA-MS-025
35-602-IA-MSG-015
35-603-IA-MSG-015
35-605-IA-MSG-015
35-604-IA-MSG-025
25x15
15V301
LOCAL CONTROL PANEL
REFER VENDOR DRG.-
HI HI TORQUE TRIP
HYD OIL LEVEL
G/BOX OIL LEVEL
RAKE POSITION
RAKE TORQUE
RAKE HIGH
RAKE LOW
35-604-FS-PE-110
35-605-FS-PE-110
35-602-FS-PE-110
35-603-FS-PE-110
35-626-PW-XS-300
THICKENER OVERFLOW
35-608-FS-XS-150
35-601-FS-XS-150
35-PP-61A
35-PP-61B
F35-708-GW-PE8-63
34\PI\0002
GLAND WATER RETICULATION NETWORK
F35-748-CON-PE8-110
TO CIL 1
30\PI\0701
F35-749-CON-PE8-110
35-617-GW-MS-015
TO STORAGE VAT
2000-F35-PID-PR-10001
PROCESS WATER TANK
34\PI\0002
75-614-GW-MS-050
35-601-PSW-PE-110
FILTER FEED TANK A DISCHARGE
35-3013-PW-SS3-50
2000-F35-PID-PR-10002
PROCESS WATER
35-601-CA-MS-050
35-601-IA-MSG-040
TIP 1013
NOTE 2
F35-801-IA-MS-080
TBA
F35-797-PW-PE8-110
F35-790-CON-PE8-280
DESLIME CYCLONE
F35-785-CON-PE8-90
F35-798-CON-PE8-63
F35-792-CON-PE8-90
FILTER FEED TANK B
FILTER FEED TANK A
DRAIN
SAMPLE POINT
GENERAL FAULT
F35-FL-X1
SLIMES FLOTATION PLANT (VENDOR PACKAGE)
F35-PP-66
SLIMES FLOTATION CONCENTRATE PUMP (GLAND SEALED)
F35-791-CON-PE8-160
F35-799-CON-PE8-63
TAILS FAULT
F35-PP-03
SLIMES FLOTATION TAILS PUMP
35-PS-63
35-AG-63 FINAL CONCENTRATE ISA AGITATOR
35-FD-63 CONCENTRATES THICKENER FEED BOX
35-SM-63 FLOTATION CONCENTRATE FEED SAMPLER
35-PP-61A/B CONCENTRATE THICKENER U/FLOW PUMP No.1 & 2
35-TH-61 FLOTATION CONCENTRATE THICKENER
35-PS-63 CONCENTRATE THICKENER AREA WASHDOWN PUMP
NOTE:
TO BE READ IN CONJUNCTION WITH 35\Pi\0443
NOTES:
1. FOR TYPICAL INSTRUMENT DETAILS REFER TO DRG 30\PI\0701
2. EXISING BUTTERFLY VALVE NOT PART OF Owner PROJECT.
3. FEEDBOX ON TOP OF CONCENTRATE THICKENER DOES NOT HAVE AN AGITATOR
LEGEND
EXISTING
NON-EXISTENT
STAGE 1 - NEW
STAGE 1 - REMOVE
STAGE 1 - DECOMMISSIONED (OTHERS)
STAGE 2 - NEW
STAGE 2 - REMOVE
STAGE 2 - DECOMMISSIONED (OTHERS)