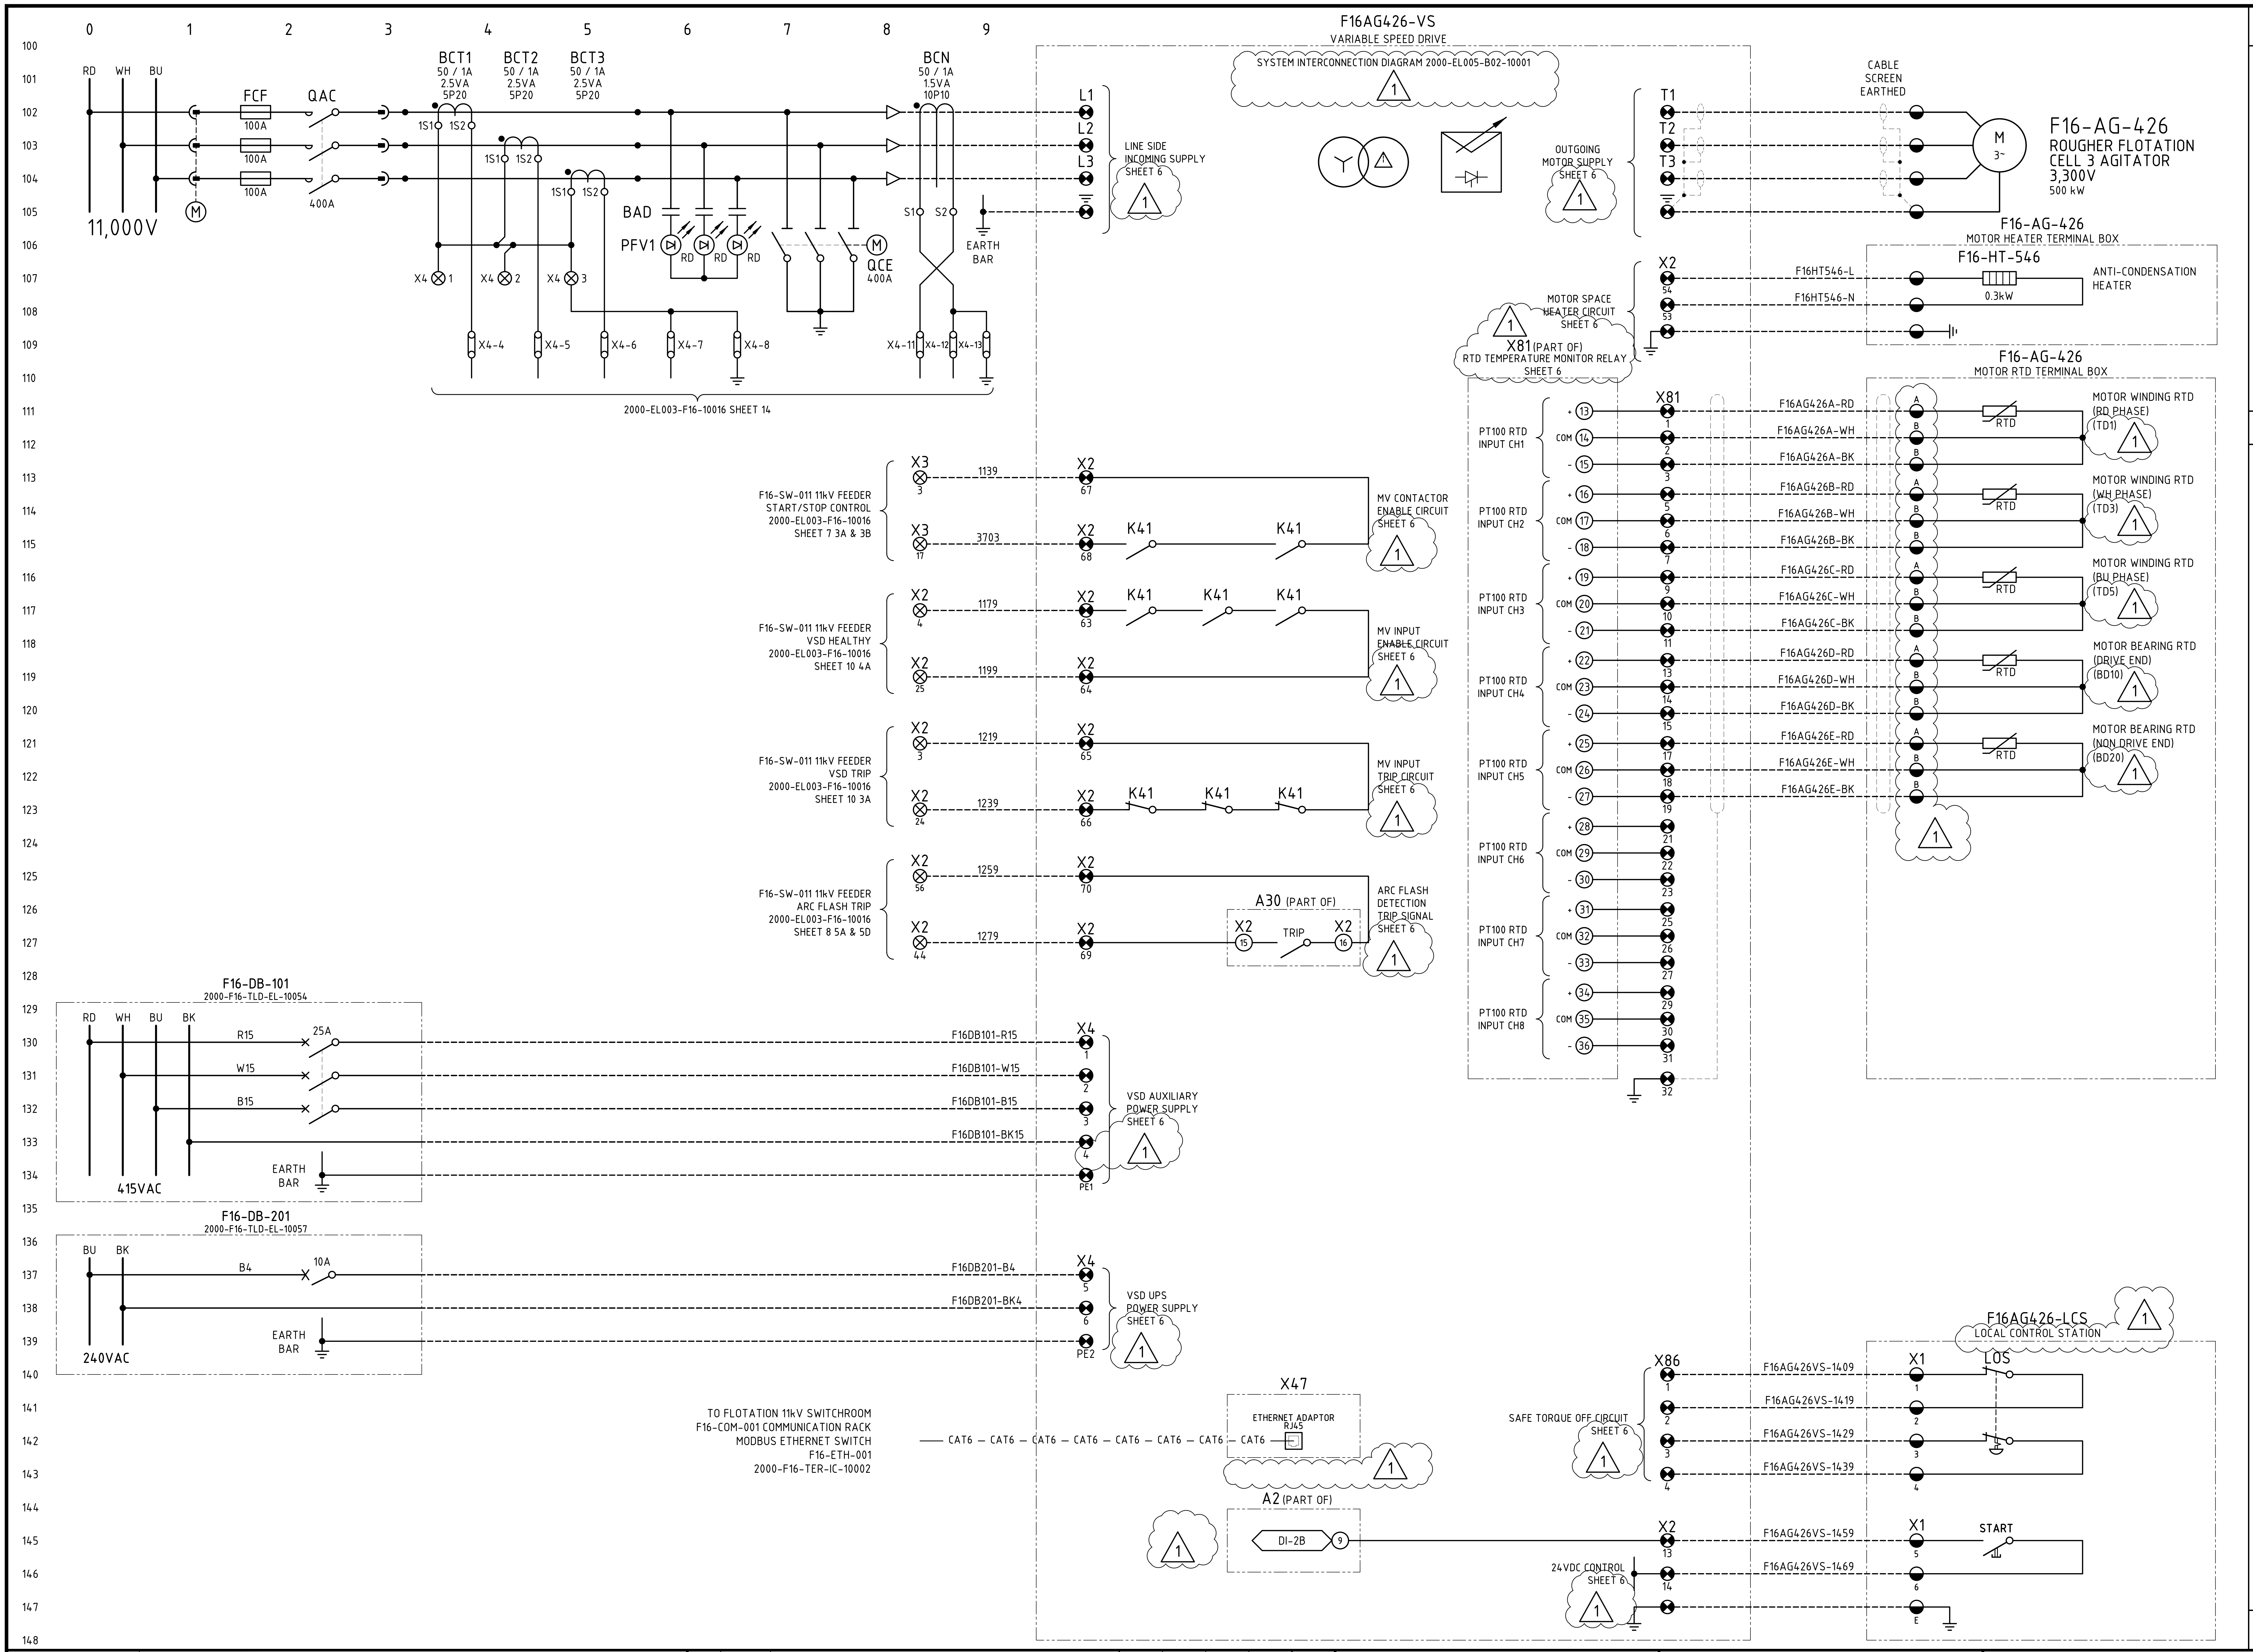

NOTES

1. WIRE NUMBER FERRULES ON TERMINAL STRIP SHALL BE PREFIXED WITH EQUIPMENT NUMBER e.g. F16AG426-1200, UNLESS OTHERWISE NOTED.
2. EACH WIRE SHALL BE IDENTIFIED AT BOTH ENDS WITH FERRULES.

LEGEND

⊗	11kV SWITCHBOARD TERMINAL
⨂	VSD TERMINAL
◒	FIELD TERMINAL
◑	DCS OR I/O TERMINAL
◧	MARSHALLING TERMINAL
ⓧ	DEVICE TERMINAL

PANEL A07

DRG No.	REFERENCES
2000-EL003-F16-10016	F16-SW-011 ABB SCHEMATIC DIAGRAM
2000-F16-TER-EL-10113	F16-SW-011 11kV SWITCHBOARD - PANEL A07 (F16AG426-VS) TERMINATION DIAGRAM SHEET 1
2000-F16-SLD-EL-10002	F16-SW-011 11kV SWITCHBOARD SINGLE LINE DIAGRAM SHEET 2
2000-F00-STD-EL-10001	GENERAL NOTES AND STANDARD DRAWINGS INDEX

REV	DATE	DESCRIPTION	DRAW	CHECK	DESIGN	TECH APP	PROJ APP
			[redacted]	[redacted]	[redacted]		[redacted]
1	29AUG25	FAT REDLINES INCORPORATED	[redacted]	[redacted]	[redacted]	[redacted]	[redacted]
0	15JAN25	APPROVED FOR CONSTRUCTION	[redacted]	[redacted]	[redacted]	[redacted]	[redacted]

NORTHERN STAR
RESOURCES LIMITED

PRIMERO
primero.com.au | DESIGN | CONSTRUCT | OPERATE

PRIMERO PROJECT NUMBER: 23517

INFORMATION AND REPRESENTATIONS ON THIS DRAWING ARE THE INTELLECTUAL PROPERTY OF PRIMERO UNLESS SPECIFICALLY IDENTIFIED OTHERWISE. ALL RIGHTS INCLUDING USE RESERVED

PROJECT: NORTHERN STAR RESOURCES LTD
KCGM GROWTH PROJECT

TITLE: ROUGHER & SCAVENGER FLOTATION - F16-SW-011
F16-AG-426 SCAVENGER FLOT CELL 3 AGITATOR VSD FDR
SCHEMATIC DIAGRAM

SHEET	SCALE	DRG No.	REVISION
A1	NONE	2000-F16-SCM-EL-10113	1