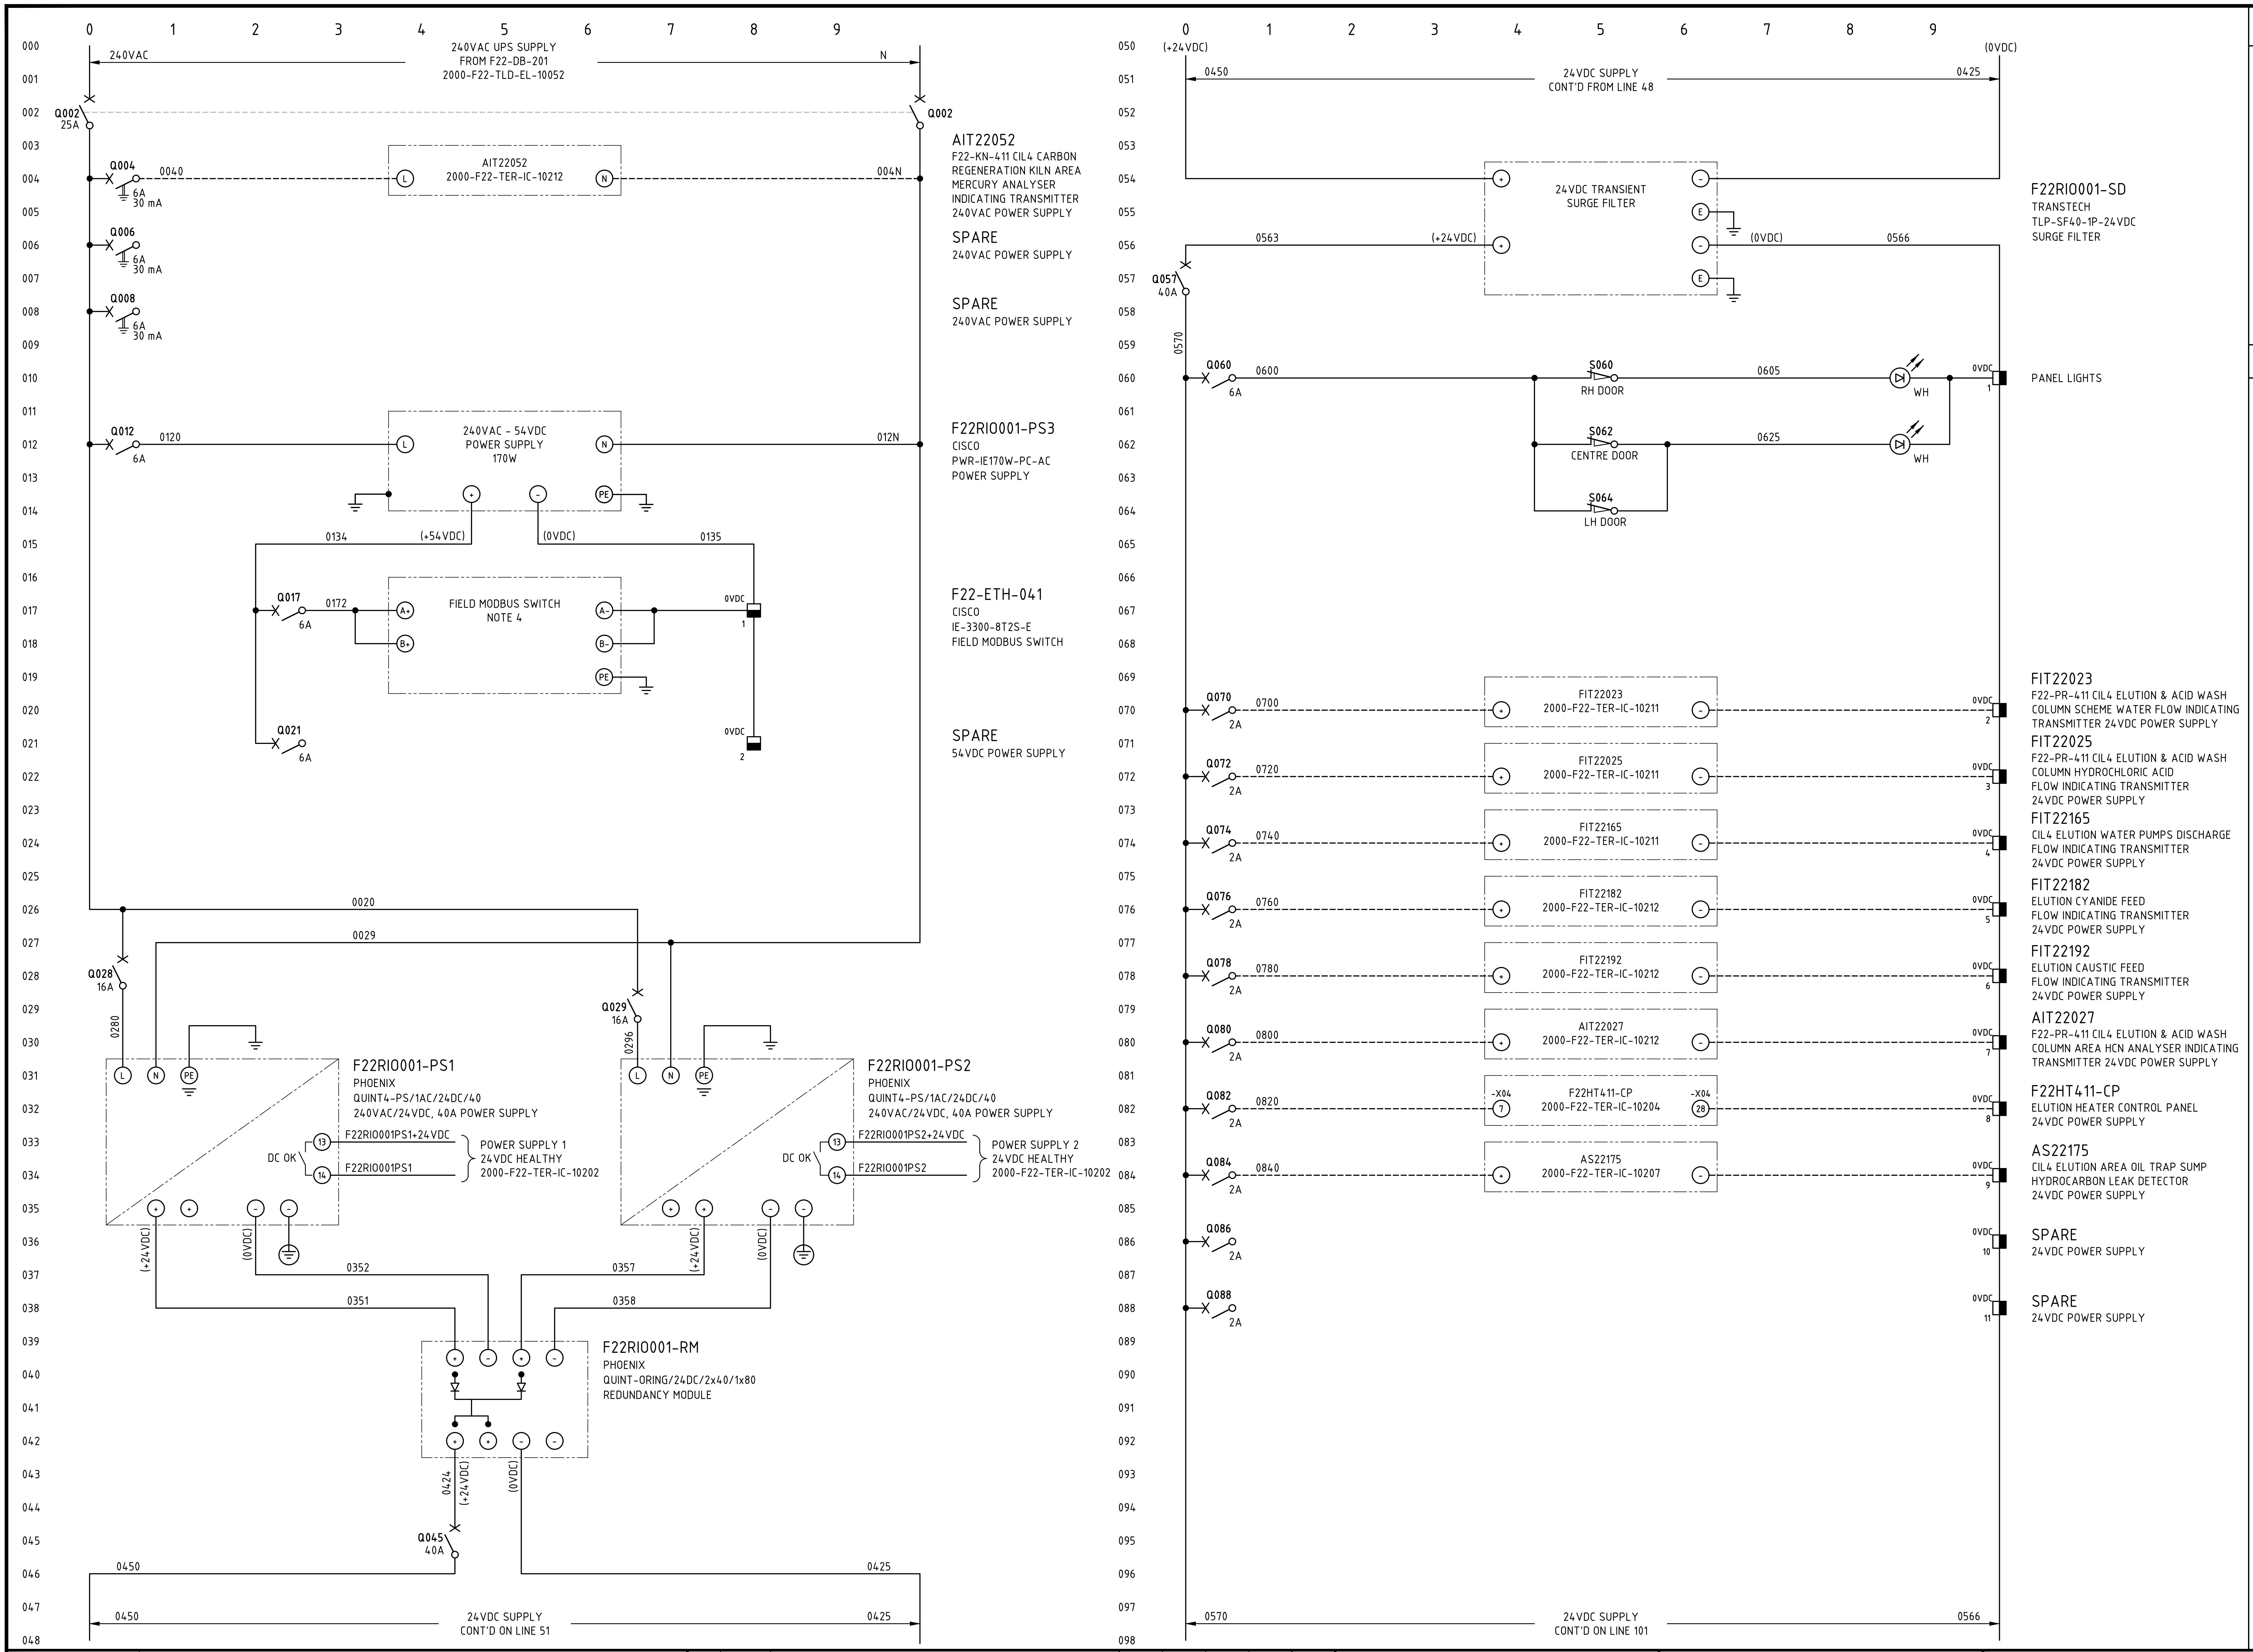
240VAC UPS SUPPLY
FROM F22-DB-201
2000-F22-TLD-EL-10052
240VAC
N
Q002
25A
Q004
0040
6A
30 mA
AIT22052
2000-F22-TER-IC-10212
004N
AIT22052
F22-KN-411 CIL4 CARBON
REGENERATION KILN AREA
MERCURY ANALYSER
INDICATING TRANSMITTER
240VAC POWER SUPPLY
Q006
Q008
SPARE
240VAC POWER SUPPLY
SPARE
240VAC POWER SUPPLY
Q012
0120
240VAC - 54VDC
POWER SUPPLY
170W
012N
F22RIO001-PS3
CISCO
PWR-IE170W-PC-AC
POWER SUPPLY
0134
(+54VDC)
(0VDC)
0135
Q017
0172
FIELD MODBUS SWITCH
NOTE 4
F22-ETH-041
CISCO
IE-3300-8T2S-E
FIELD MODBUS SWITCH
Q021
SPARE
54VDC POWER SUPPLY
0020
0029
Q028
16A
0280
Q029
16A
0296
F22RIO001-PS1
PHOENIX
QUINT4-PS/1AC/24DC/40
240VAC/24VDC, 40A POWER SUPPLY
DC OK
F22RIO001PS1+24VDC
F22RIO001PS1
POWER SUPPLY 1
24VDC HEALTHY
2000-F22-TER-IC-10202
F22RIO001-PS2
PHOENIX
QUINT4-PS/1AC/24DC/40
240VAC/24VDC, 40A POWER SUPPLY
F22RIO001PS2+24VDC
F22RIO001PS2
POWER SUPPLY 2
24VDC HEALTHY
2000-F22-TER-IC-10202
(+24VDC)
(0VDC)
0351
0352
0357
0358
F22RIO001-RM
PHOENIX
QUINT-ORING/24DC/2x40/1x80
REDUNDANCY MODULE
0424
Q045
40A
0450
0425
24VDC SUPPLY
CONT'D ON LINE 51
24VDC SUPPLY
CONT'D FROM LINE 48
24VDC TRANSIENT
SURGE FILTER
F22RIO001-SD
TRANSTECH
TLP-SF40-1P-24VDC
SURGE FILTER
0563
0566
Q057
40A
0570
Q060
0600
S060
RH DOOR
0605
S062
CENTRE DOOR
0625
S064
LH DOOR
WH
PANEL LIGHTS
Q070
0700
FIT22023
2000-F22-TER-IC-10211
FIT22023
F22-PR-411 CIL4 ELUTION & ACID WASH
COLUMN SCHEME WATER FLOW INDICATING
TRANSMITTER 24VDC POWER SUPPLY
Q072
0720
FIT22025
2000-F22-TER-IC-10211
FIT22025
F22-PR-411 CIL4 ELUTION & ACID WASH
COLUMN HYDROCHLORIC ACID
FLOW INDICATING TRANSMITTER
24VDC POWER SUPPLY
Q074
0740
FIT22165
2000-F22-TER-IC-10211
FIT22165
CIL4 ELUTION WATER PUMPS DISCHARGE
FLOW INDICATING TRANSMITTER
24VDC POWER SUPPLY
Q076
0760
FIT22182
2000-F22-TER-IC-10212
FIT22182
ELUTION CYANIDE FEED
FLOW INDICATING TRANSMITTER
24VDC POWER SUPPLY
Q078
0780
FIT22192
2000-F22-TER-IC-10212
FIT22192
ELUTION CAUSTIC FEED
FLOW INDICATING TRANSMITTER
24VDC POWER SUPPLY
Q080
0800
AIT22027
2000-F22-TER-IC-10212
AIT22027
F22-PR-411 CIL4 ELUTION & ACID WASH
COLUMN AREA HCN ANALYSER INDICATING
TRANSMITTER 24VDC POWER SUPPLY
Q082
0820
-X04
F22HT411-CP
2000-F22-TER-IC-10204
F22HT411-CP
ELUTION HEATER CONTROL PANEL
24VDC POWER SUPPLY
Q084
0840
AS22175
2000-F22-TER-IC-10207
AS22175
CIL4 ELUTION AREA OIL TRAP SUMP
HYDROCARBON LEAK DETECTOR
24VDC POWER SUPPLY
Q086
Q088
2A
SPARE
24VDC POWER SUPPLY
SPARE
24VDC POWER SUPPLY
0VDC
24VDC SUPPLY
CONT'D ON LINE 101

NOTES

1. TERMINALS ON TERMINAL STRIPS ABOVE 50VAC SHALL HAVE A SEPARATE PERSPEX SHROUD AND SHALL BE LABELLED "DANGER xxxVAC".
2. WIRE NUMBER FERRULES ON TERMINAL STRIP SHALL BE PREFIXED WITH EQUIPMENT NUMBER e.g. F22RIO001-XXXX.
3. EACH WIRE SHALL BE IDENTIFIED AT BOTH ENDS WITH FERRULES.
4. FOR NETWORK CONNECTION & BUS CABLING DETAILS REFER TO RIO PANEL COMMUNICATIONS TERMINATION DIAGRAMS.
5. INSTRUMENT EARTH BAR TO BE BONDED TO MAIN EARTH BAR WITH SOLID COPPER LINK.

LEGEND

◒	FIELD TERMINAL
◑	DCS OR I/O TERMINAL
◨	0VDC TERMINAL FOR 24VDC
⬓	0VDC TERMINAL FOR 54VDC
ⓧ	DEVICE TERMINAL
⊳ cc	INDICATION LAMP cc = COLOUR
⏚	EARTH BAR
⊜	INSTRUMENT EARTH BAR

DRG No.	REFERENCES
2000-F22-TLD-EL-10052	F22-DB-201 LV SWITCHROOM 240V UPS DB THREE LINE DIAGRAM
2000-F22-DRG-IC-10201	F22-RIO-001 FIELD N-IO PANEL GENERAL ARRANGEMENT
2000-F22-SCM-IC-10202	F22-RIO-001 FIELD N-IO PANEL SCHEMATIC DIAGRAM SHEET 2
2000-F22-TER-IC-10200	F22-RIO-001 FIELD N-IO PANEL COMMUNICATIONS TERMINATION DIAGRAM SHEET 1 (TO SHEET 2 - 10201)
2000-F22-TER-IC-10202	F22-RIO-001 FIELD N-IO PANEL TERMINATION DIAGRAM SHEET 1 (TO SHEET 12 - 10213)
2000-F00-STD-EL-10001	GENERAL NOTES AND STANDARD DRAWINGS INDEX

REV	DATE	DESCRIPTION	DRAW	CHECK	DESIGN	TECH APP	PROJ APP
0	17APR25	APPROVED FOR CONSTRUCTION	[redacted]				

NORTHERN STAR
RESOURCES LIMITED

PRIMERO
primero.com.au | DESIGN | CONSTRUCT | OPERATE

PRIMERO PROJECT NUMBER: 23517

PROJECT: NORTHERN STAR RESOURCES LTD
KCGM GROWTH PROJECT

TITLE: CIL4 - CARBON TREATMENT & ELUTION
F22-RIO-001 ELUTION FIELD N-IO PANEL
SCHEMATIC DIAGRAM SHEET 1

INFORMATION AND REPRESENTATIONS ON THIS DRAWING ARE THE INTELLECTUAL PROPERTY OF PRIMERO UNLESS SPECIFICALLY IDENTIFIED OTHERWISE. ALL RIGHTS INCLUDING USE RESERVED

SHEET	SCALE	DRG No.	REVISION
A1	NONE	2000-F22-SCM-IC-10201	0

O:\CAD PROJECTS\235 NORTHERN STAR RESOURCES LTD\23517 KCGM GROWTH PROJECT\03 DELIVERABLES\IC\F22 - CIL4 CARBON TREAMENT & ELUTION\2000-F22-SCM-IC-10201.DWG 17APR25 6:40AM SANDRA.CULL