

Docusign Envelope ID: 8E76B63A-48AC-42D5-A478-EF0F2193FA0A

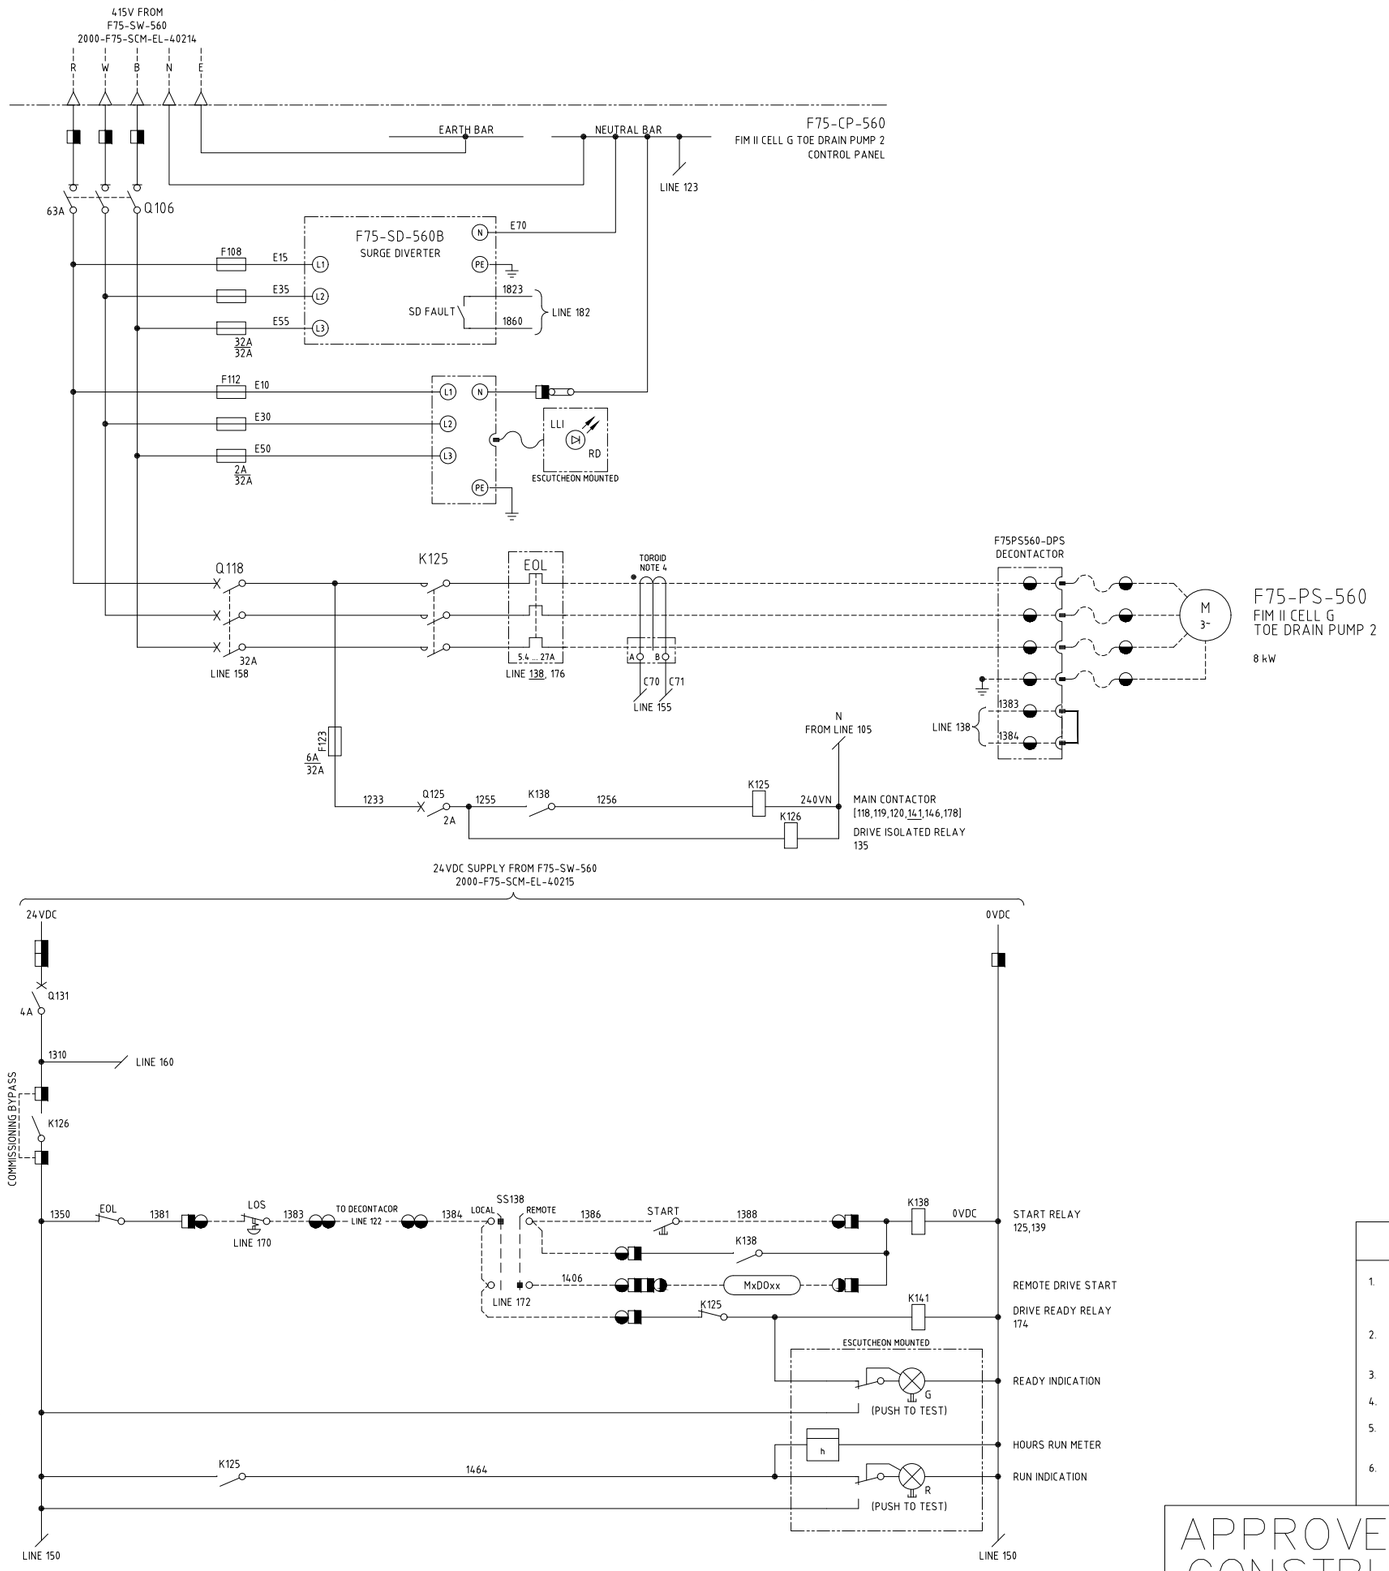

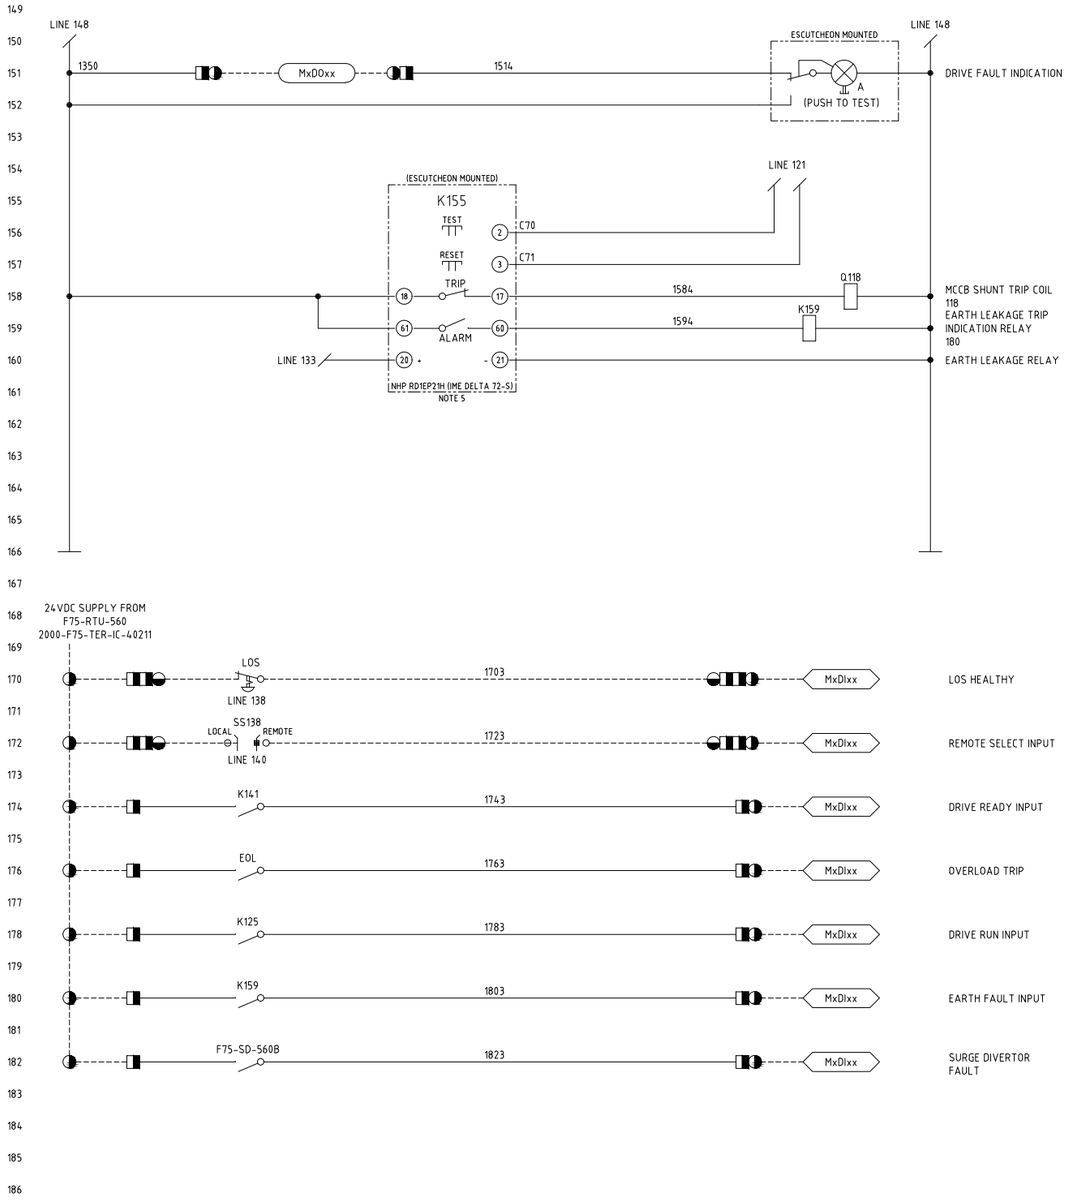


NOTES

1. TERMINALS ON TERMINAL STRIPS ABOVE 50VAC SHALL HAVE A SEPARATE PERSPEX SHROUD AND SHALL BE LABELLED "DANGER xxxVAC".
2. WIRE NUMBER FERRULES ON TERMINAL STRIP SHALL BE PREFIXED WITH EQUIPMENT NUMBER e.g. FxxPSxxx-1200.
3. EACH WIRE SHALL BE IDENTIFIED AT BOTH ENDS WITH FERRULES.
4. NHP TDGx2 TOROID TO SUIT CABLE DIAMETER.
5. EARTH LEAKAGE RELAY USER INTERFACE TO BE MOUNTED ON CONTROL PANEL ESCUTCHEON.
6. REFER 2000-F75-LST-IC-40004 FOR RTU I/O ADDRESSES AND TERMINATION DETAILS.

LEGEND

- MxDIxx — RTU DIGITAL INPUT
- MxDOxx — RTU DIGITAL OUTPUT
- SWITCHBOARD TERMINAL
- VSD TERMINAL
- FIELD TERMINAL
- RTU TERMINAL
- CONTROL PANEL TERMINAL
- DEVICE TERMINAL
- INDICATION LAMP cc = COLOUR

TERMINATION LEGEND

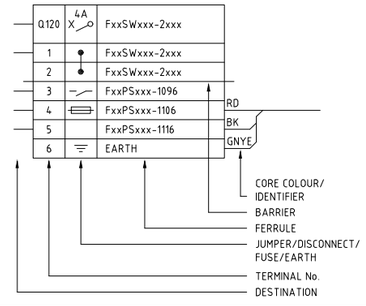

APPROVED FOR CONSTRUCTION

REFERENCES	DWG No	REV	DATE	REVISION
F75-RTU-560 FIM II TSF CELL G SWITCHBOARD 1 RTU TERMINATION DIAGRAM SHEET 1	2000-F75-TER-IC-40211			
F75-SW-560 FIM II TSF CELL G SWITCHBOARD 1 SCHEMATIC DIAGRAM SHEET 2	2000-F75-SCM-EL-40215			
F75-CP-560 FIM II CELL G TOE DRAIN PUMP 2 CONTROL PANEL GENERAL ARRANGEMENT SHEET 1	2000-F75-DRG-EL-40217			
F75-CP-560 FIM II CELL G TOE DRAIN PUMP 2 CONTROL PANEL TERMINATION DIAGRAM	2000-F75-TER-EL-40212			
F75-SW-560 FIM II TSF CELL G SWITCHBOARD 1 SCHEMATIC DIAGRAM SHEET 1	2000-F75-SCM-EL-40214			
GENERAL NOTES AND STANDARD DRAWINGS INDEX	2000-F00-STD-EL-10001	O	29.MAY.25	APPROVED FOR CONSTRUCTION

	Initial	Initial	Initial	DS
	FG	KVN	KVN	TH
	DRN	CHK	TECH APP	APP

NORTHERN STAR RESOURCES LIMITED

DRA PACIFIC (PTY) LIMITED

DRAWN	J.TORRALBA	03.APR.2025
CHECKED	L.YANG.WEN	03.APR.2025
DESIGNED	J.TORRALBA	03.APR.2025
TECH APP	K.VAN.NAMEN	29.APR.2025
PROJ APP	T.HAMDORF	29.MAY.2025
CLIENT APP		

PROJECT: KCGM
FIM TSF PROJECT

TITLE: FIM II TAILINGS DAM
F75-CP-560 FIM II CELL G TOE DRAIN PUMP 2 CP
SCHEMATIC DIAGRAM

SIZE	SCALE	DRG No.	REV
A1	NTS	2000-F75-SCM-EL-40212	O