


RECYCLE CONVEYOR 2 METAL DETECTOR
2000-F13-PID-PR-10005
SIGNAL

RECYCLE CONVEYOR 2
2000-F13-PID-PR-10005
PEBBLES

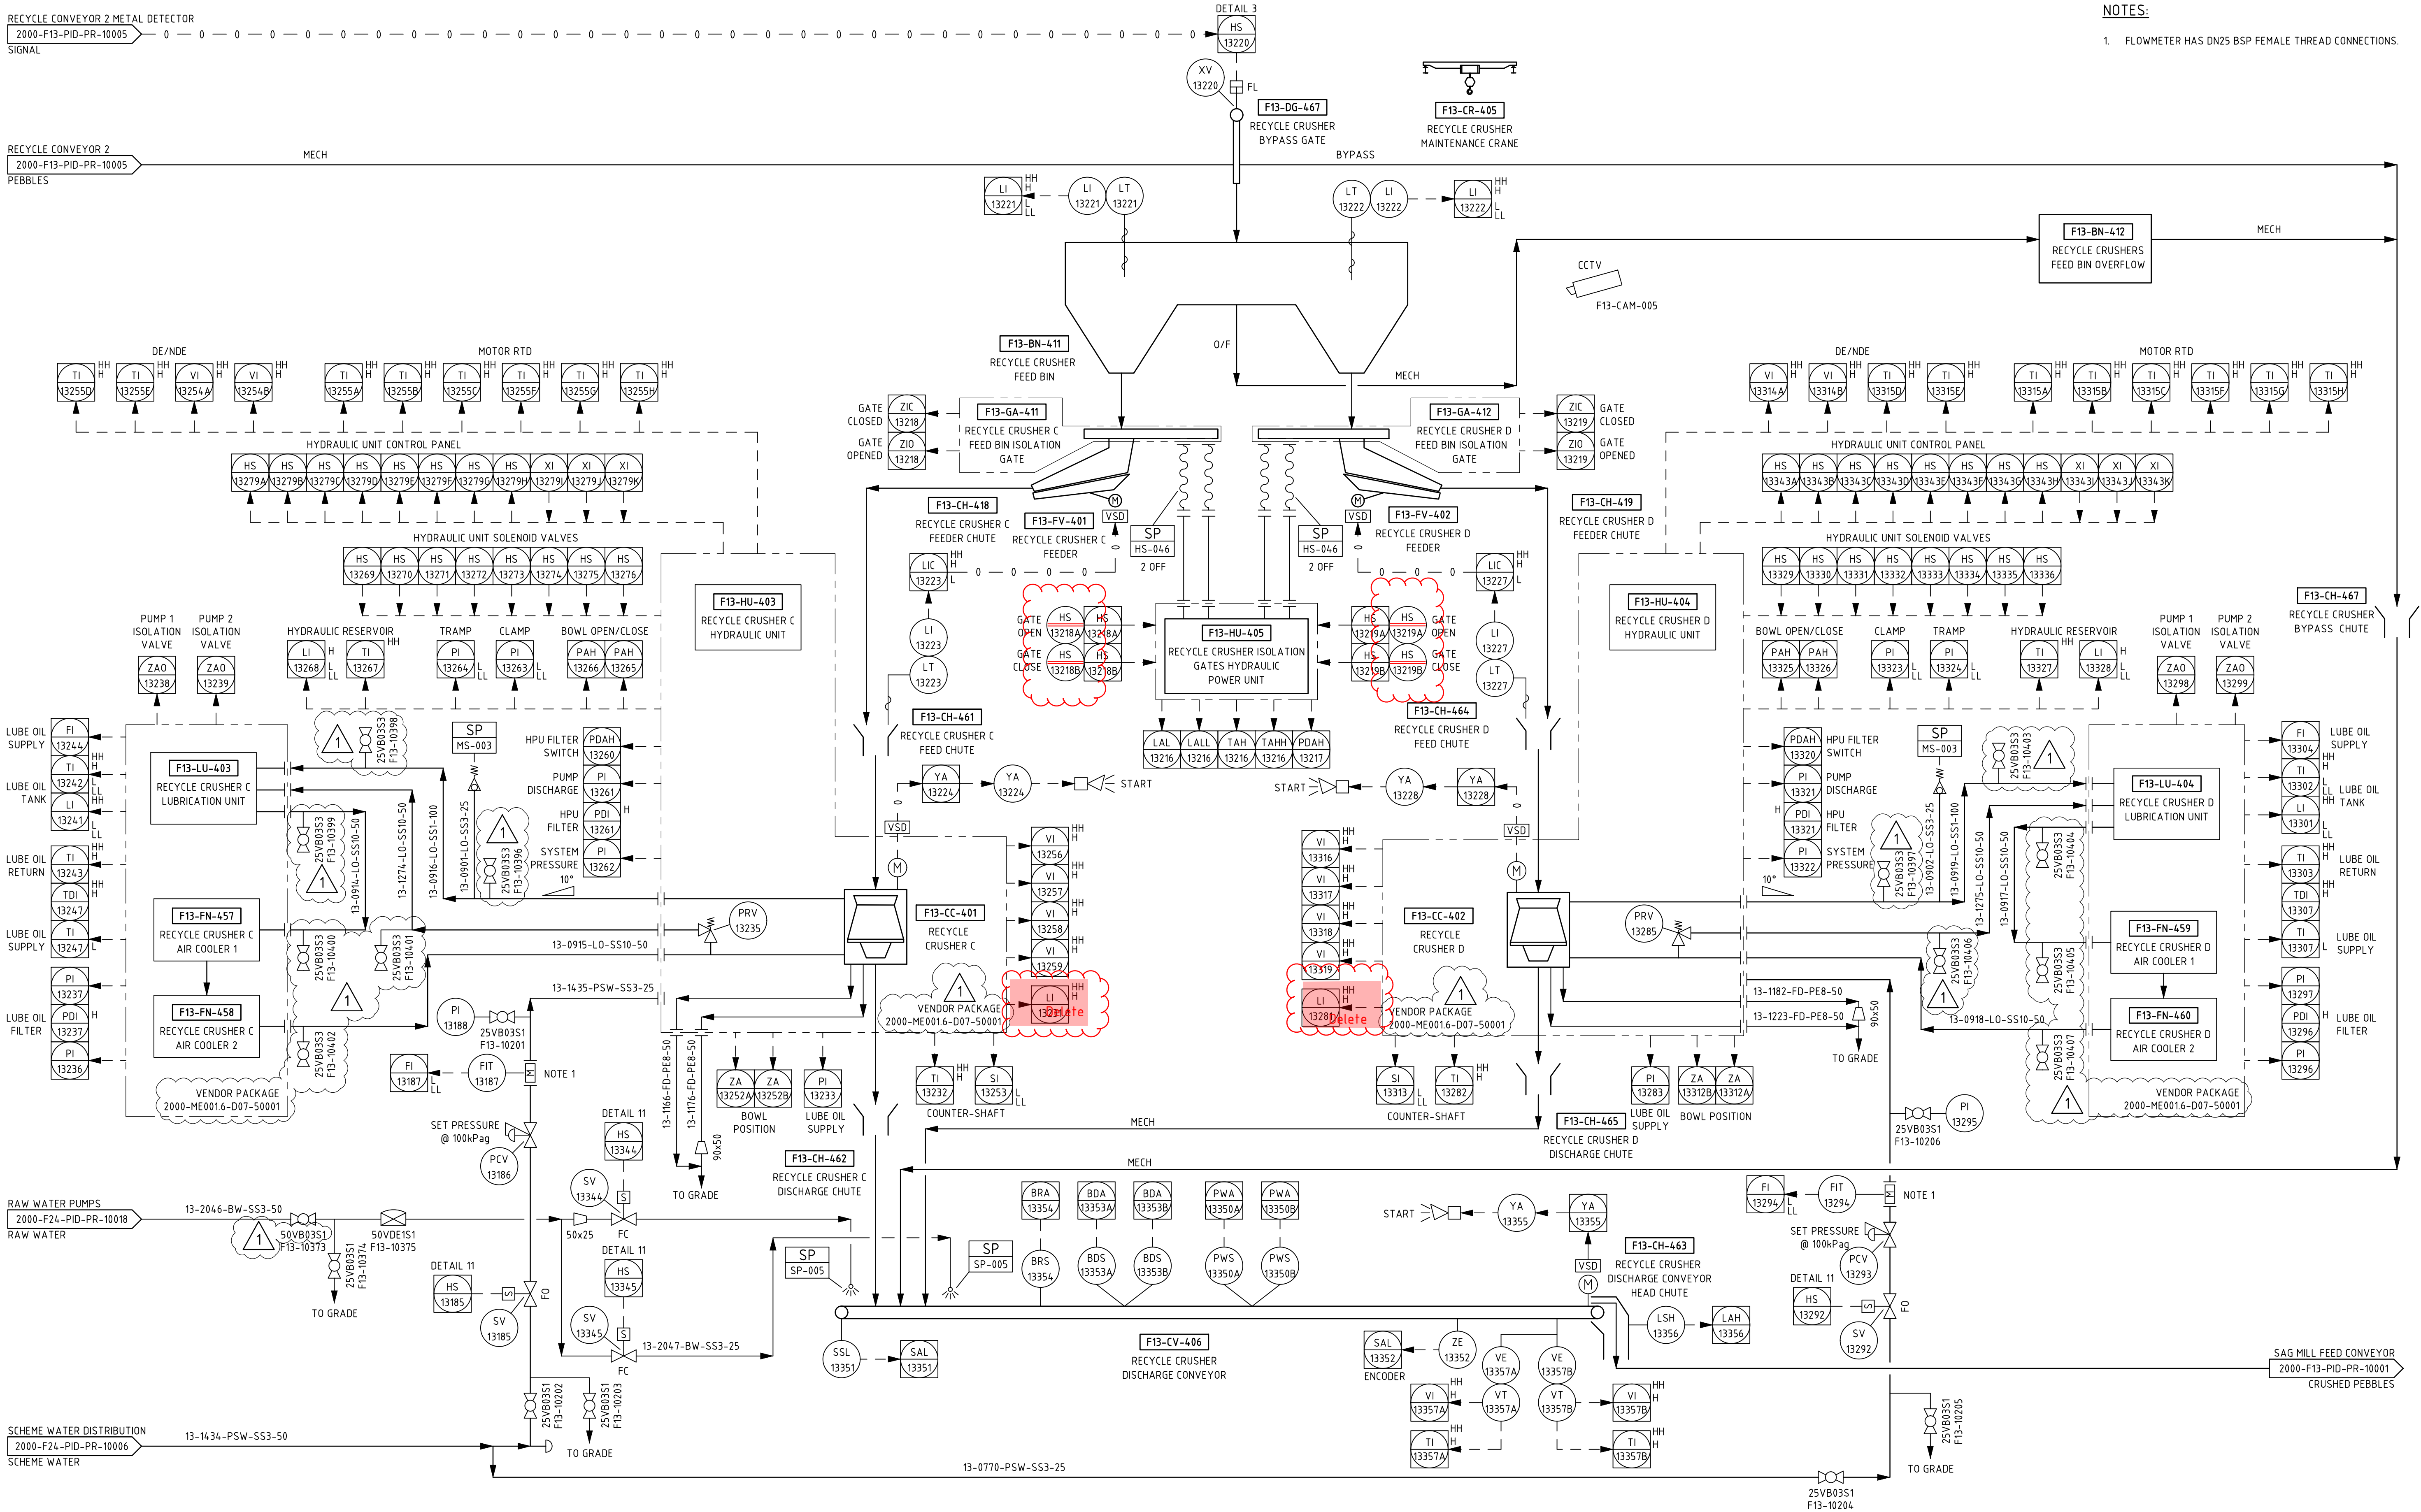

NOTES:

1. FLOWMETER HAS DN25 BSP FEMALE THREAD CONNECTIONS.