


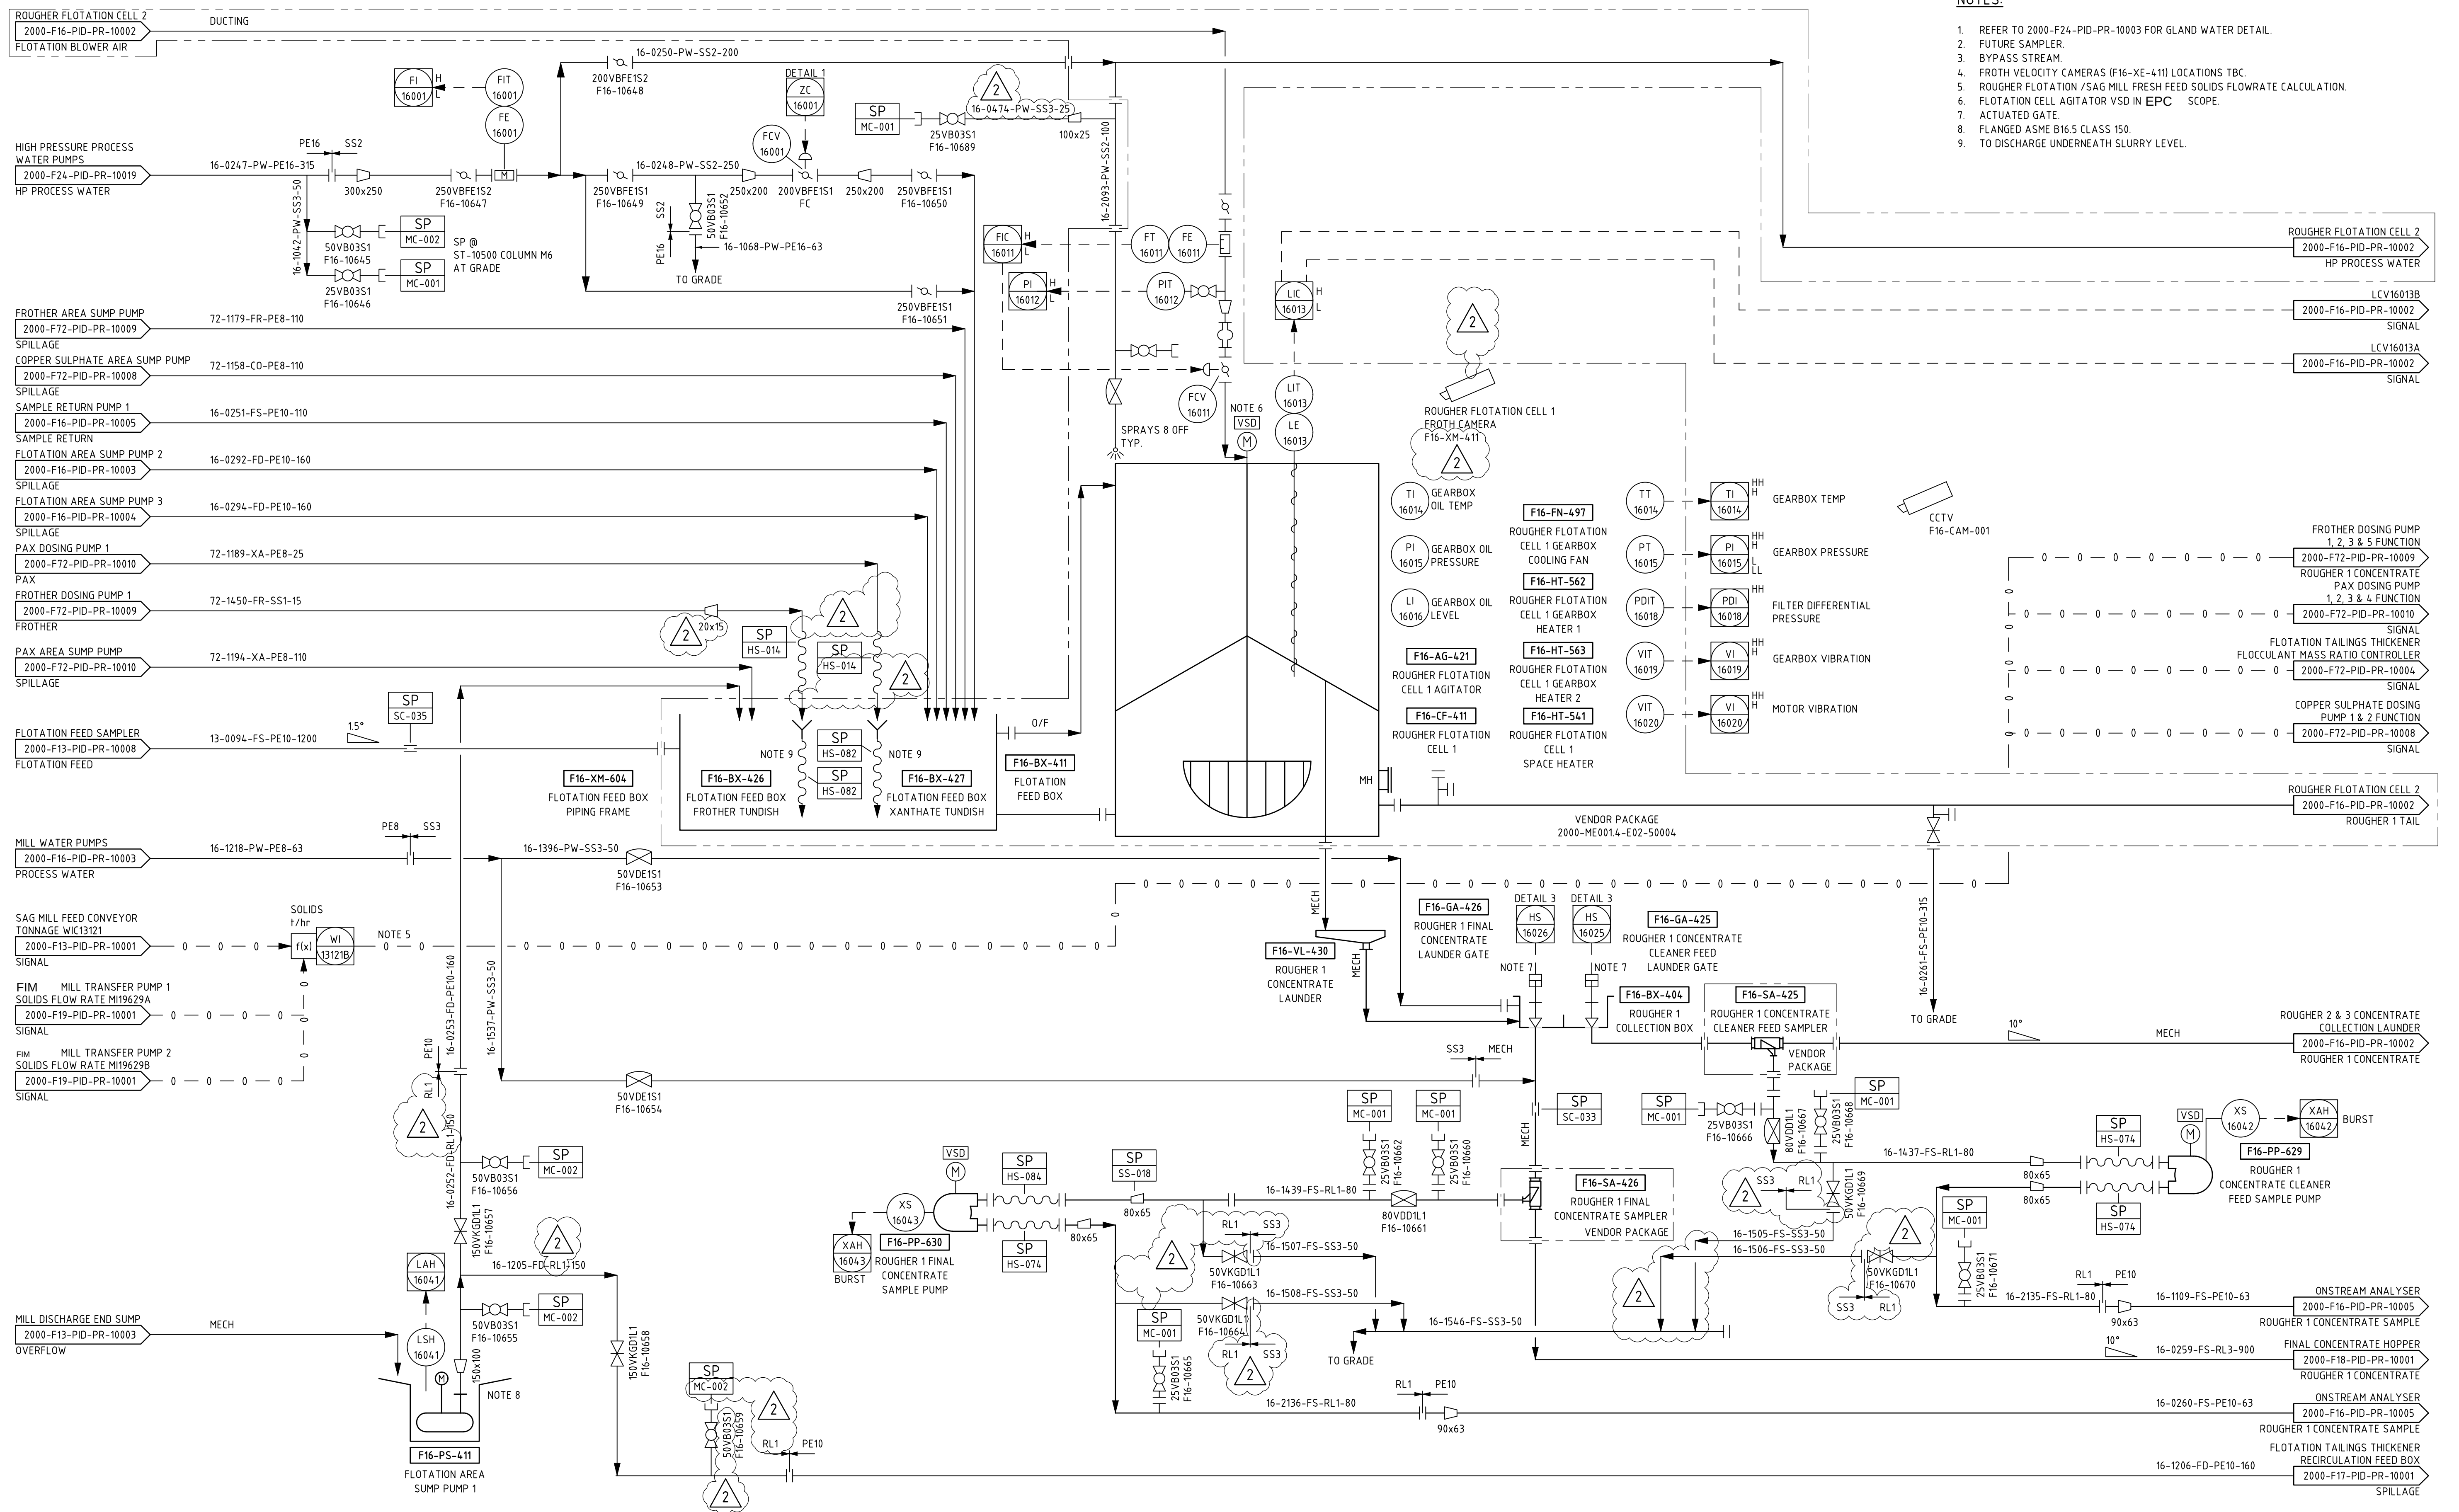

1. REFER TO 2000-F24-PID-PR-10003 FOR GLAND WATER DETAIL.
2. FUTURE SAMPLER.
3. BYPASS STREAM.
4. FROTH VLOCITY CAMERAS (F16-XE-411) LOCATIONS TBC.
5. ROUGHER FLOTATION /SAG MILL FRESH FEED SOLIDS FLOWRATE.
6. FLOTATION CELL AGITATOR VSD IN EPC SCOPE.
7. ACTUATED GATE.
8. FLANGED ASME B16.5 CLASS 150.
9. TO DISCHARGE UNDERNEATH SLURRY LEVEL.

1. REFER TO 2000-FID-PID-PR-10003 FOR GLAND WATER DETAIL.
2. FUTURE SAMPLER.
3. BYPASS STREAM.
4. FROTH VELOCITY CAMERAS (F16-XE-411) LOCATIONS TBC.
5. ROUGHER FLOTATION /SAG MILL FRESH FEED SOLIDS FLOWRATE CALCULATION.
6. FLOTATION CELL AGITATOR VSD IN EPC SCOPE.
7. ACTUATED GATE.
8. FLANGED ASME B16.5 CLASS 150.
9. TO DISCHARGE UNDERNEATH SLURRY LEVEL.