


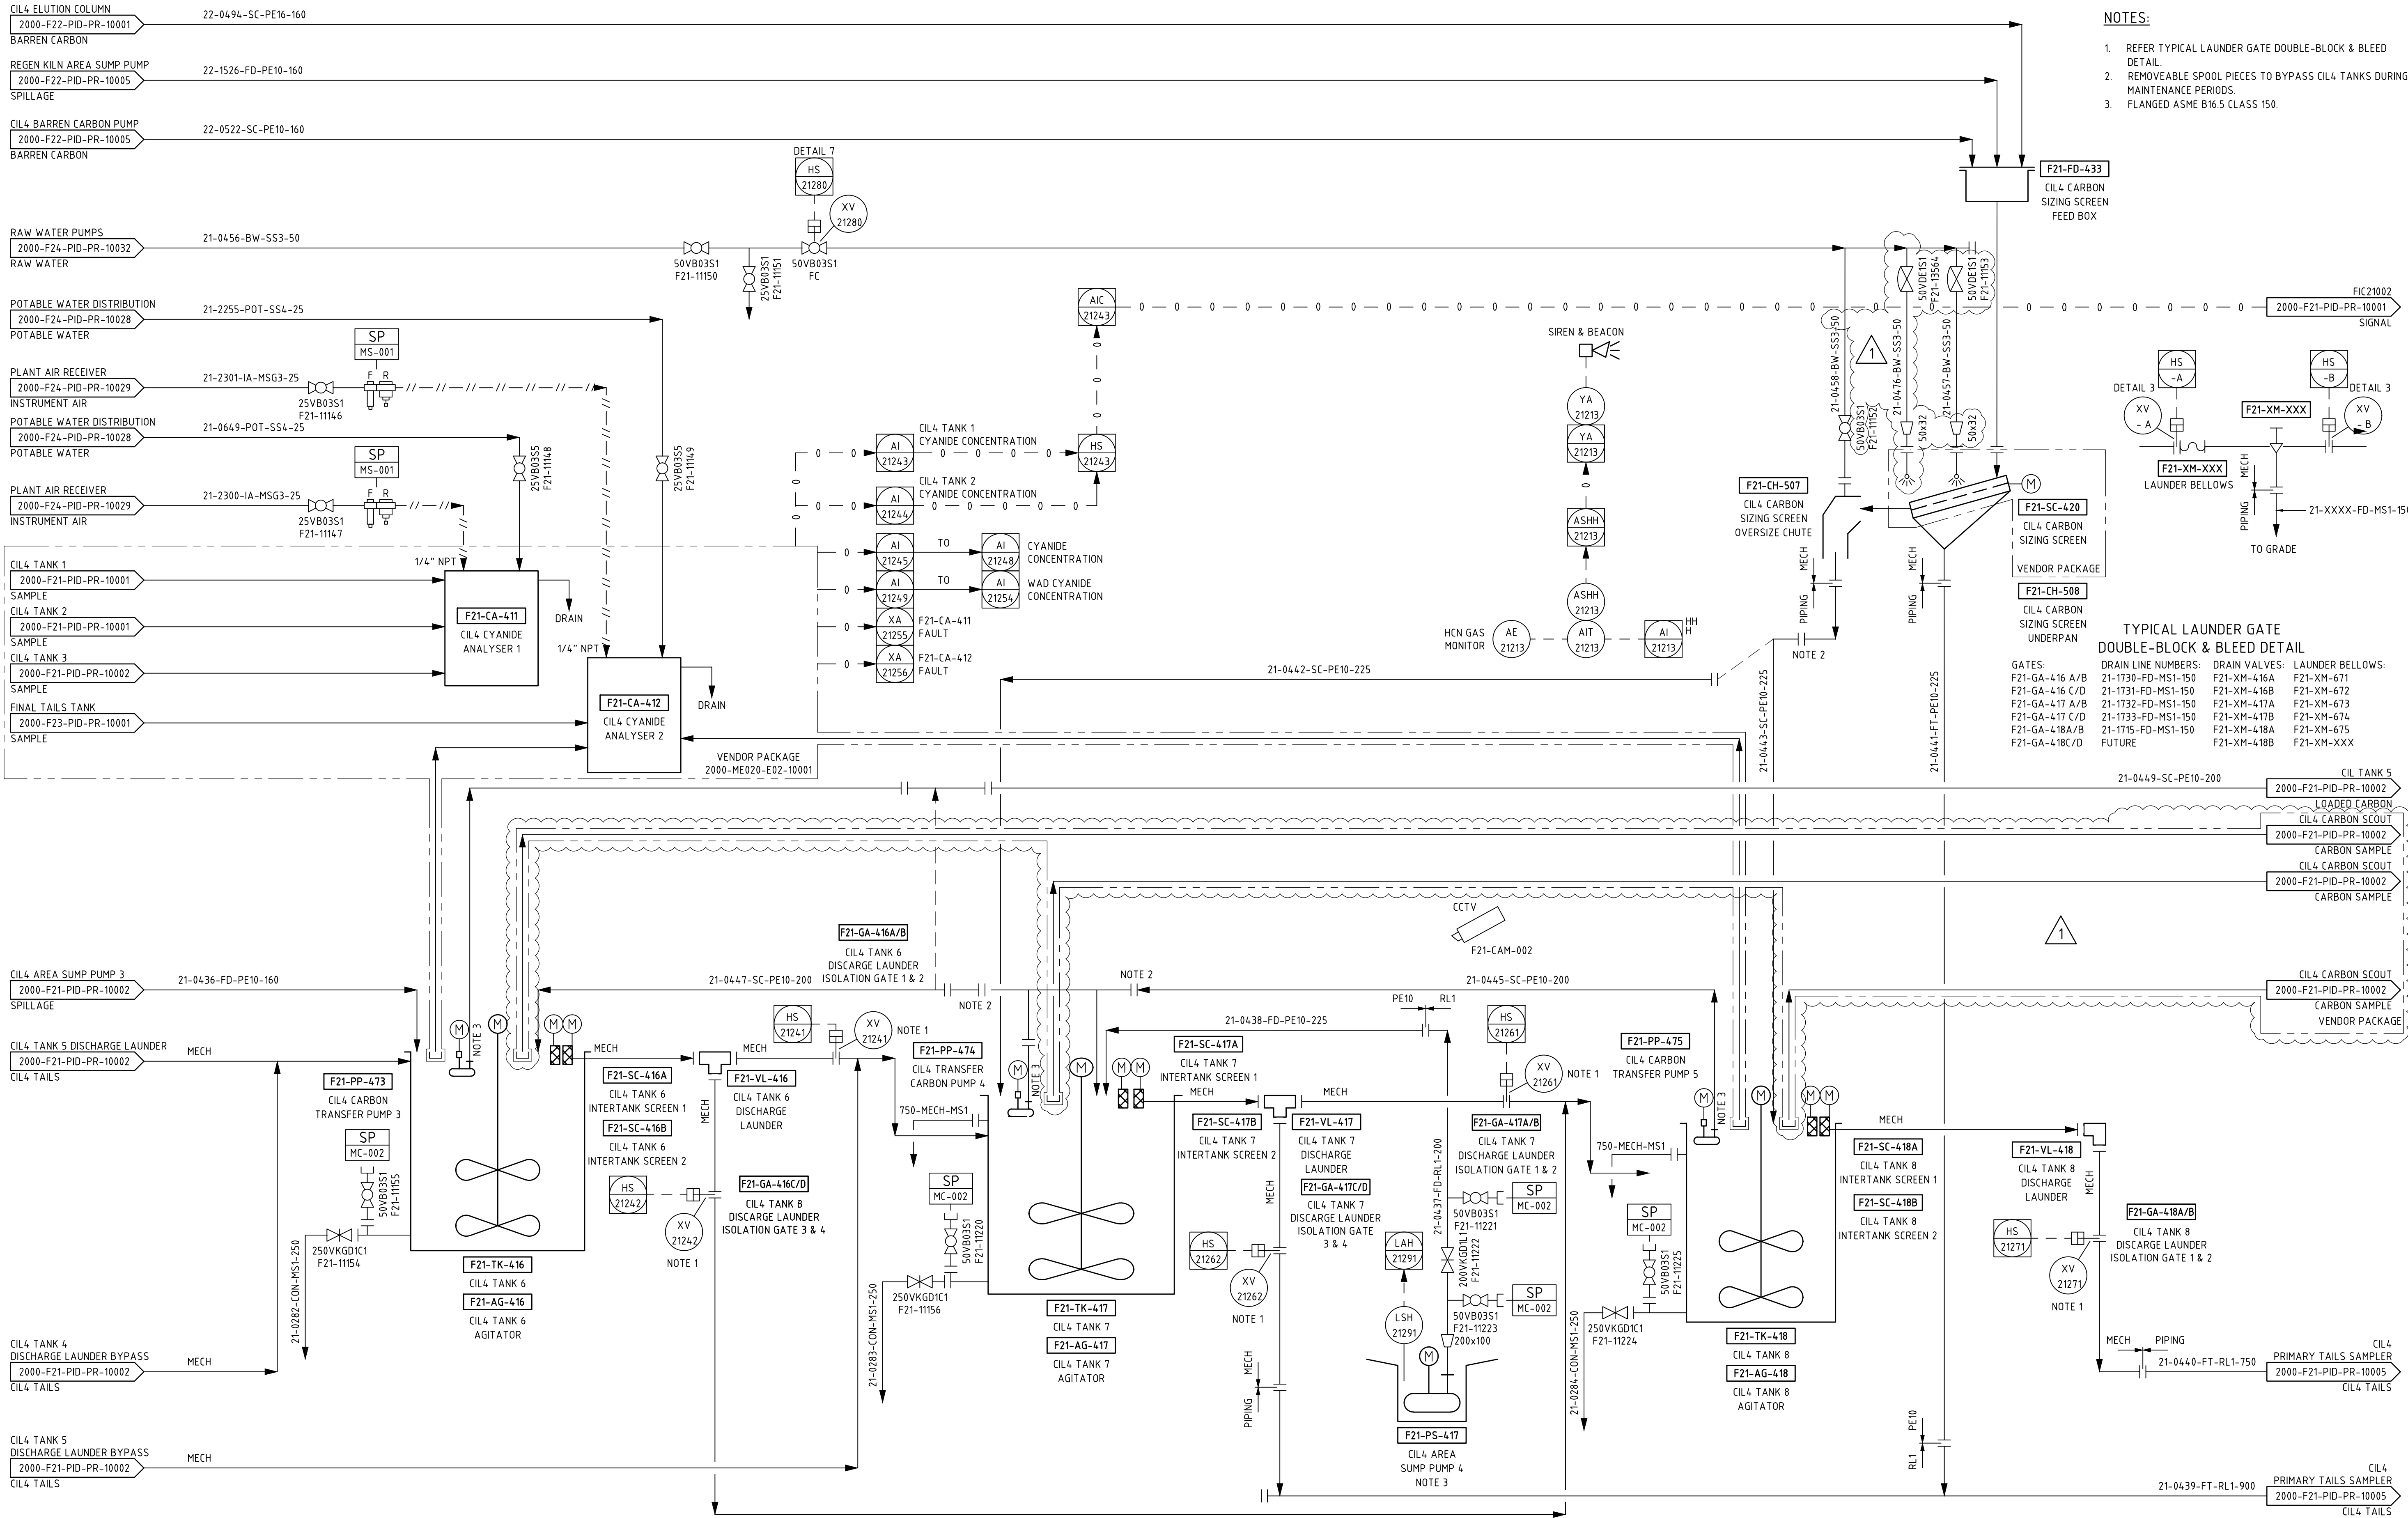

- NOTES:
1. REFER TYPICAL LAUNDER GATE DOUBLE-BLOCK & BLEED DETAIL.
 2. REMOVEABLE SPOOL PIECES TO BYPASS CIL4 TANKS DURING MAINTENANCE PERIODS.
 3. FLANGED ASME B16.5 CLASS 150.

TYPICAL LAUNDER GATE DOUBLE-BLOCK & BLEED DETAIL

GATES:	DRAIN LINE NUMBERS:	DRAIN VALVES:	LAUNDER BELLOWS:
F21-GA-416 A/B	21-1730-FD-MS1-150	F21-XM-416A	F21-XM-671
F21-GA-416 C/D	21-1731-FD-MS1-150	F21-XM-416B	F21-XM-672
F21-GA-417 A/B	21-1732-FD-MS1-150	F21-XM-417A	F21-XM-673
F21-GA-417 C/D	21-1733-FD-MS1-150	F21-XM-417B	F21-XM-674
F21-GA-418A/B	21-1715-FD-MS1-150	F21-XM-418A	F21-XM-675
F21-GA-418C/D	FUTURE	F21-XM-418B	F21-XM-XXX