

LEGEND:

EXISTING

NEW

———— FUTURE



— — — — — DECOMMISSIONED

NOTES:

1. VALVES WILL BE HYDRAULICALLY ACTUATED VIA HYDRAULIC POWER PACK F23-HY-420.
2. DRAIN WILL BE LOCATED AT PIPE LOW POINT PRIOR TO RAILWAY.
3. MANUAL OPERATED VALVE WITH PROXIMITY SWITCHES.

HOLDS:

1. ON HOLD PENDING CONFIRMATION OF VENDOR DATA.

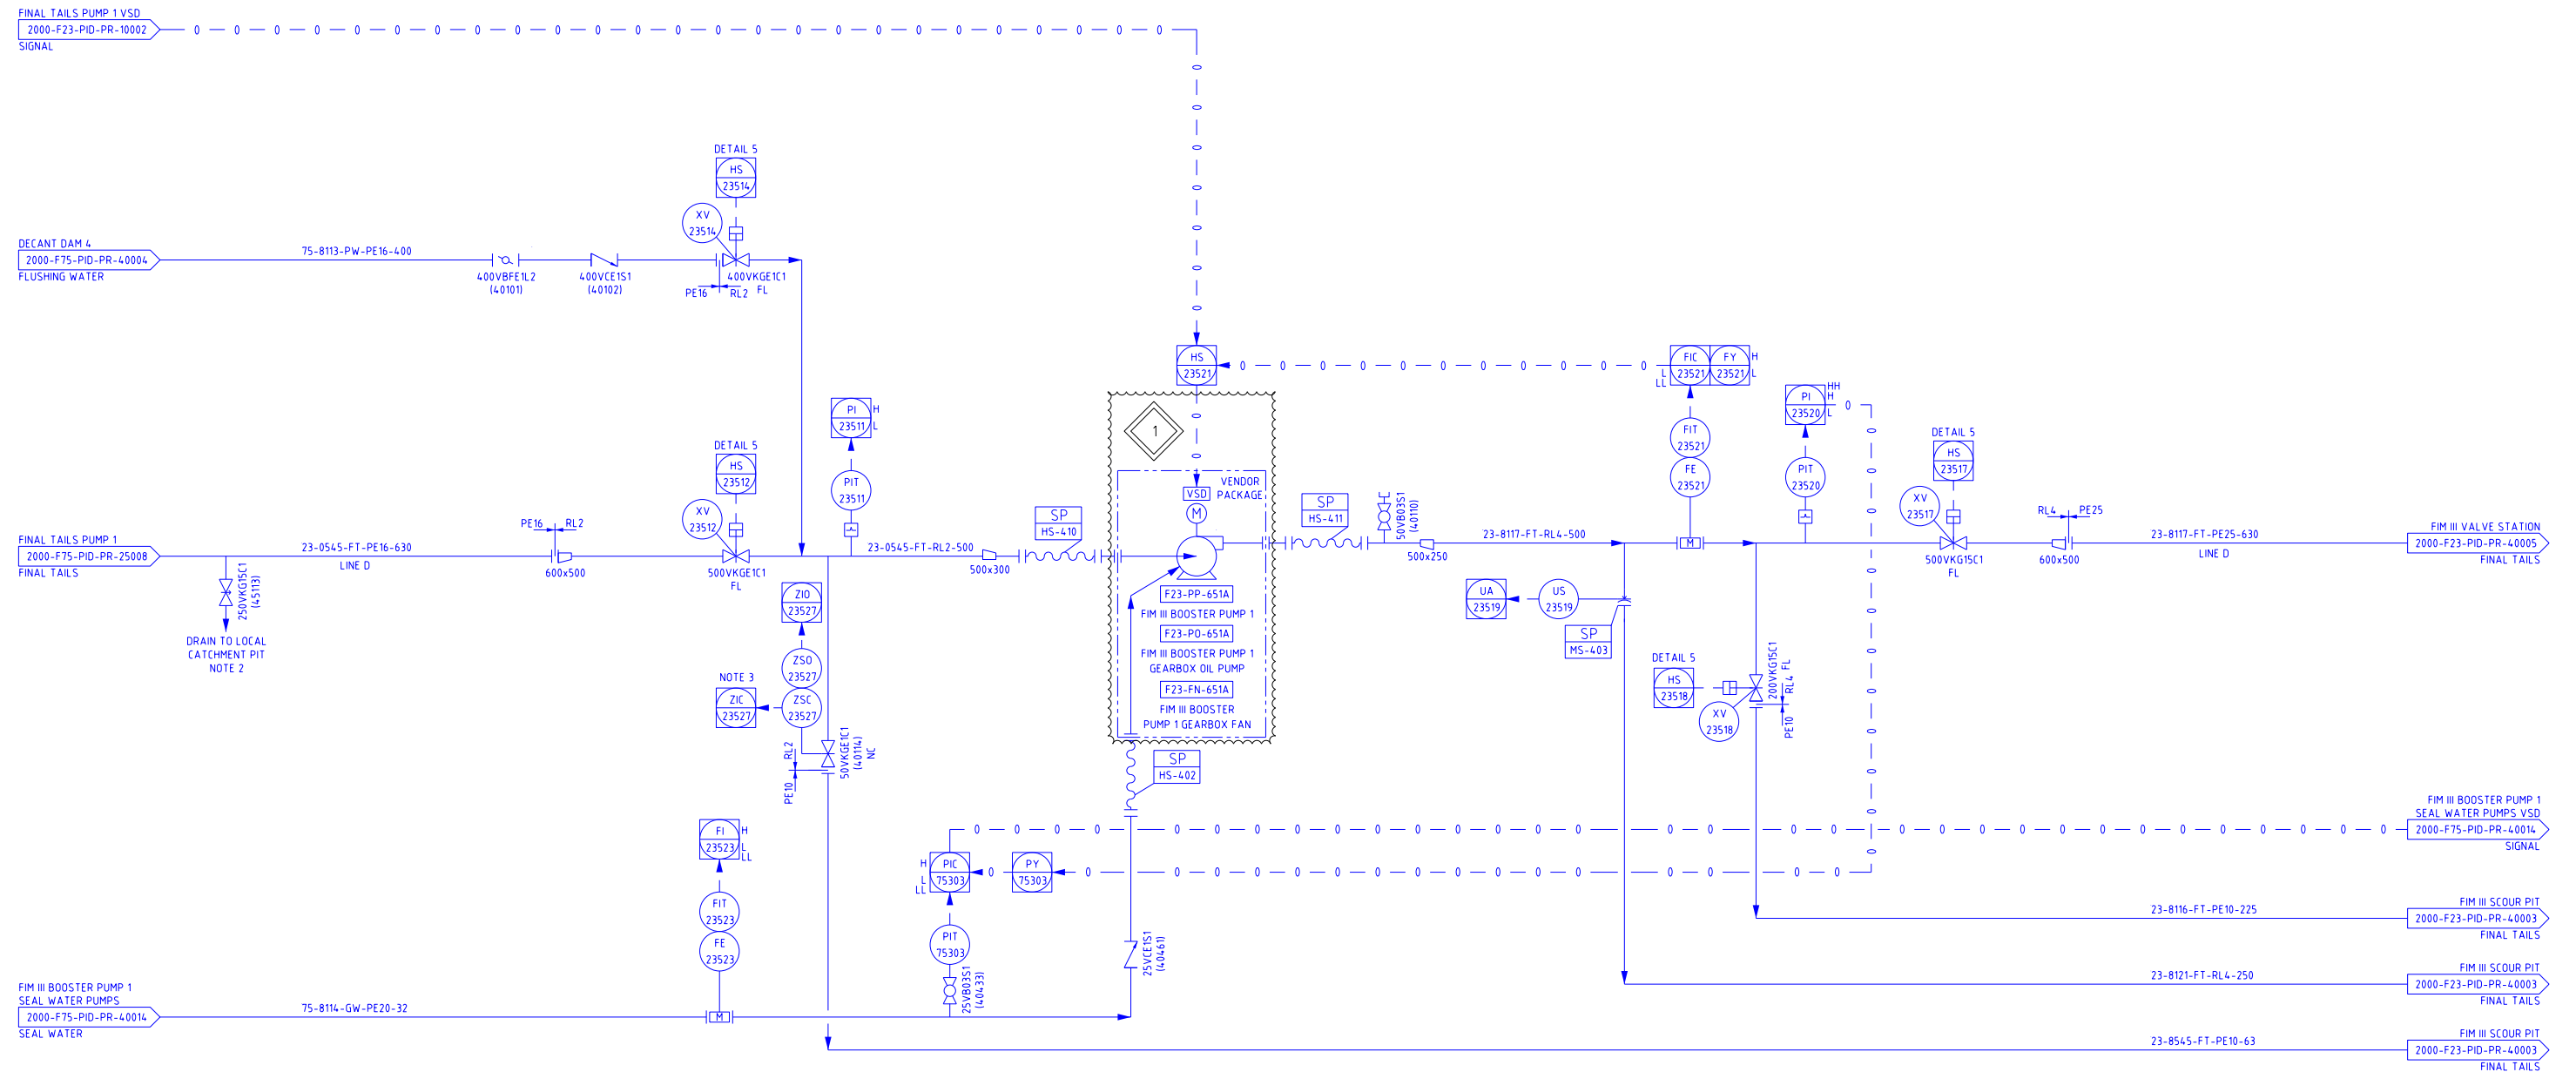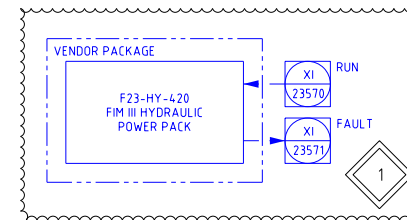

APPROVED FOR
CONSTRUCTION