


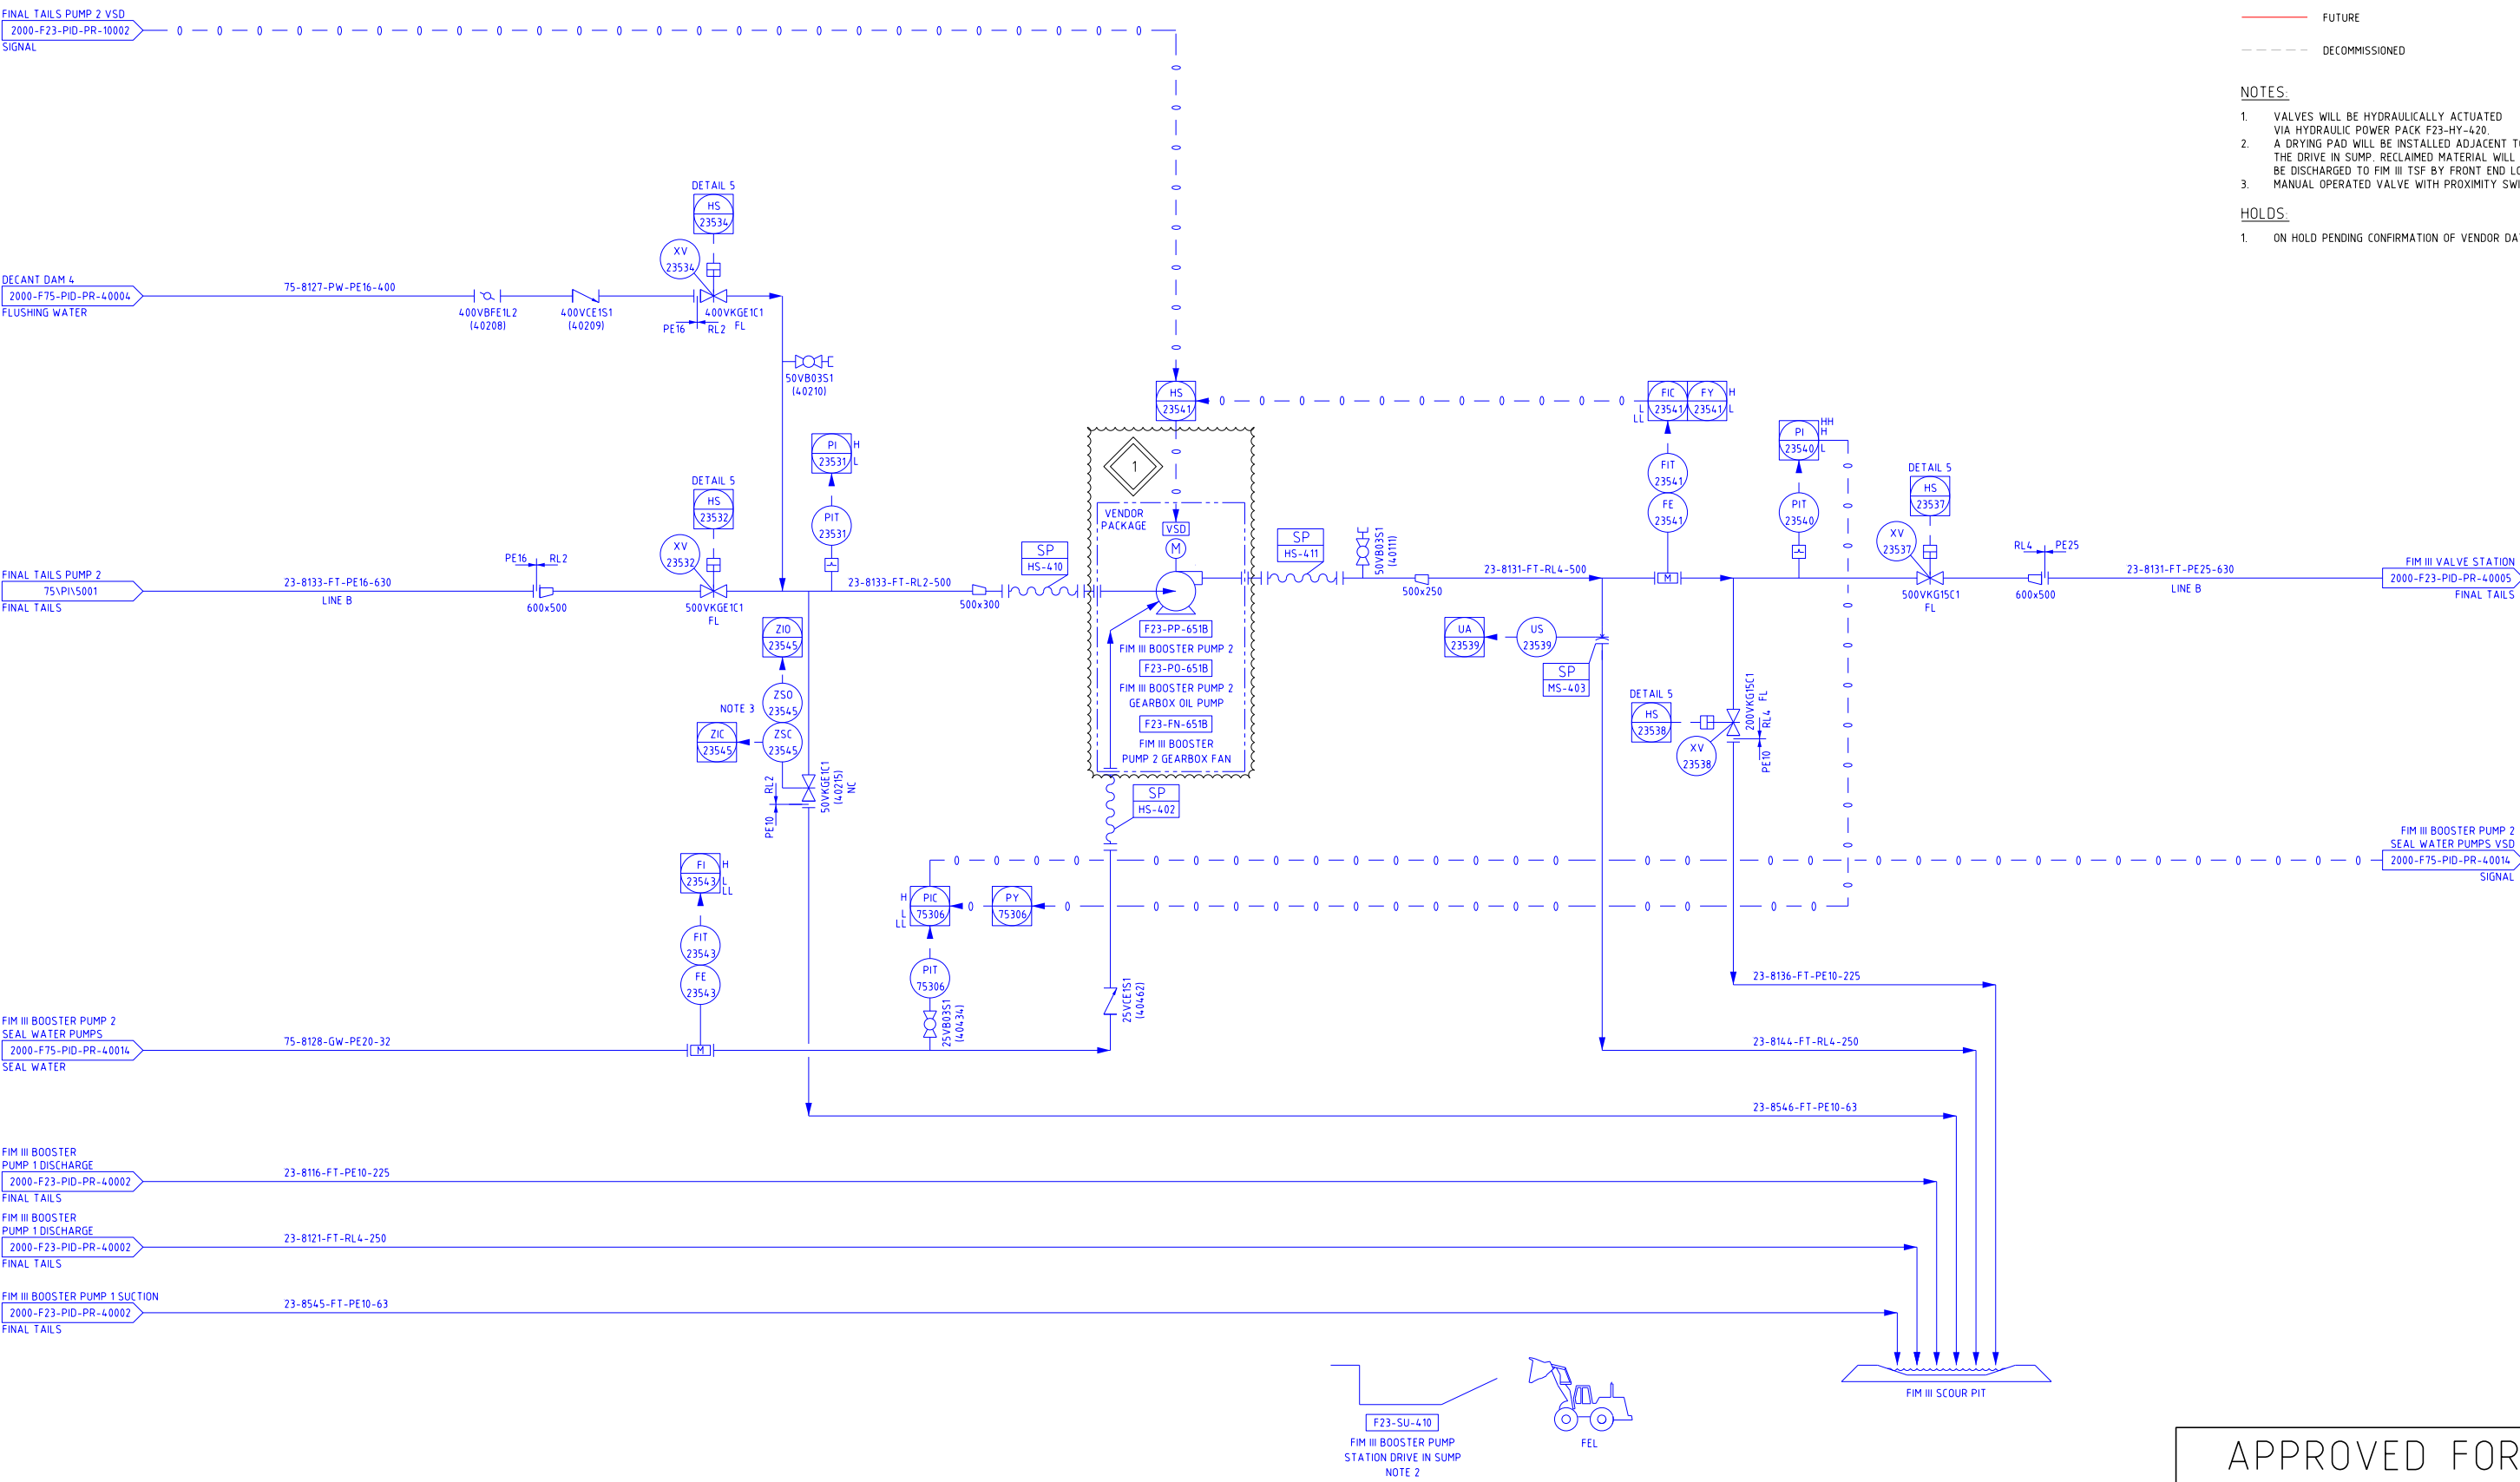

- LEGEND:**
- EXISTING
 - NEW
 - FUTURE
 - DECOMMISSIONED

- NOTES:**
- VALVES WILL BE HYDRAULICALLY ACTUATED VIA HYDRAULIC POWER PACK F23-HY-420.
 - A DRYING PAD WILL BE INSTALLED ADJACENT TO THE DRIVE IN SUMP. RECLAIMED MATERIAL WILL BE DISCHARGED TO FIM III TSF BY FRONT END LOADER.
 - MANUAL OPERATED VALVE WITH PROXIMITY SWITCHES.
- HOLDS:**
- ON HOLD PENDING CONFIRMATION OF VENDOR DATA.

APPROVED FOR
CONSTRUCTION