


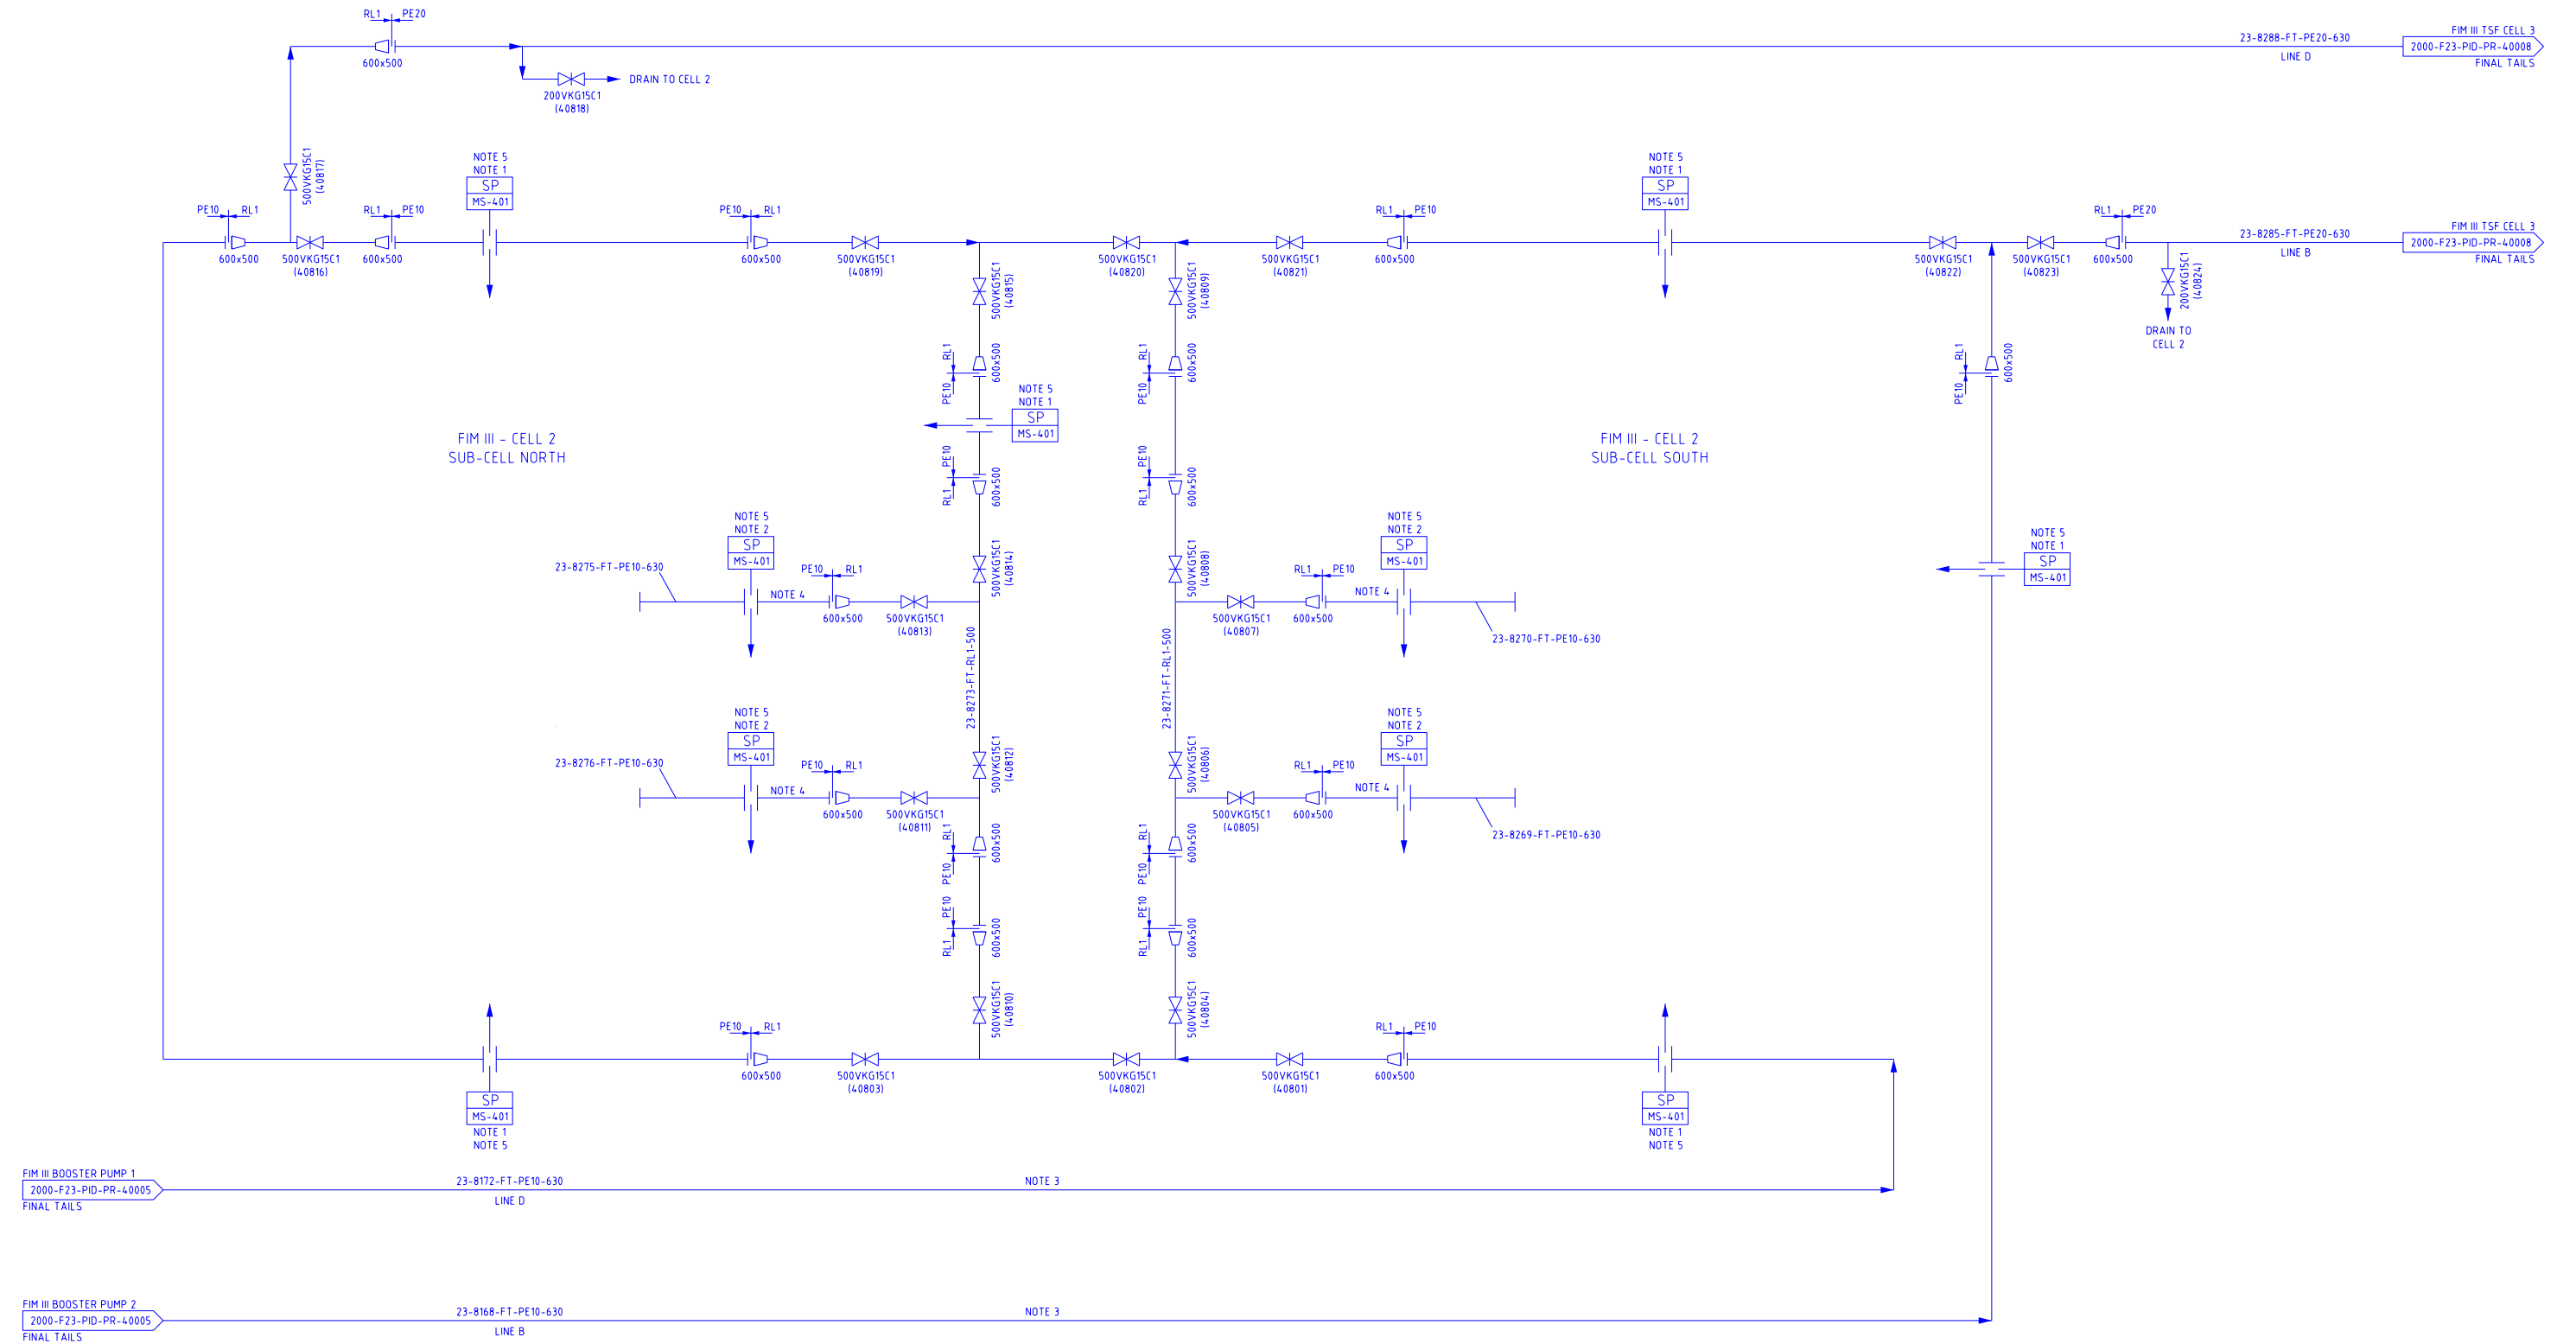

APPROVED FOR
CONSTRUCTION

- NOTES:**
1. SPIGOTS PLACED AT 40m CENTRES UNLESS OTHERWISE NOTED.
 2. SPIGOTS PLACED AT 15m CENTRES ON THE CAUSEWAYS.
 3. PIPING ON TSF EMBANKMENT TO BE FLANGED EVERY 40m.
 4. CAUSEWAY PIPING TO BE FLANGED EVERY 15m.
 5. REFER TO DRAWING 2000-T03-DRG-GE-40003 FOR SPIGOT DETAILS. A TOTAL OF 357 SPIGOTS REQUIRED WITH UNIQUE VALVE NUMBERS 43401 TO 43757.
- LEGEND:**
- EXISTING
 - NEW
 - FUTURE
 - DECOMMISSIONED