


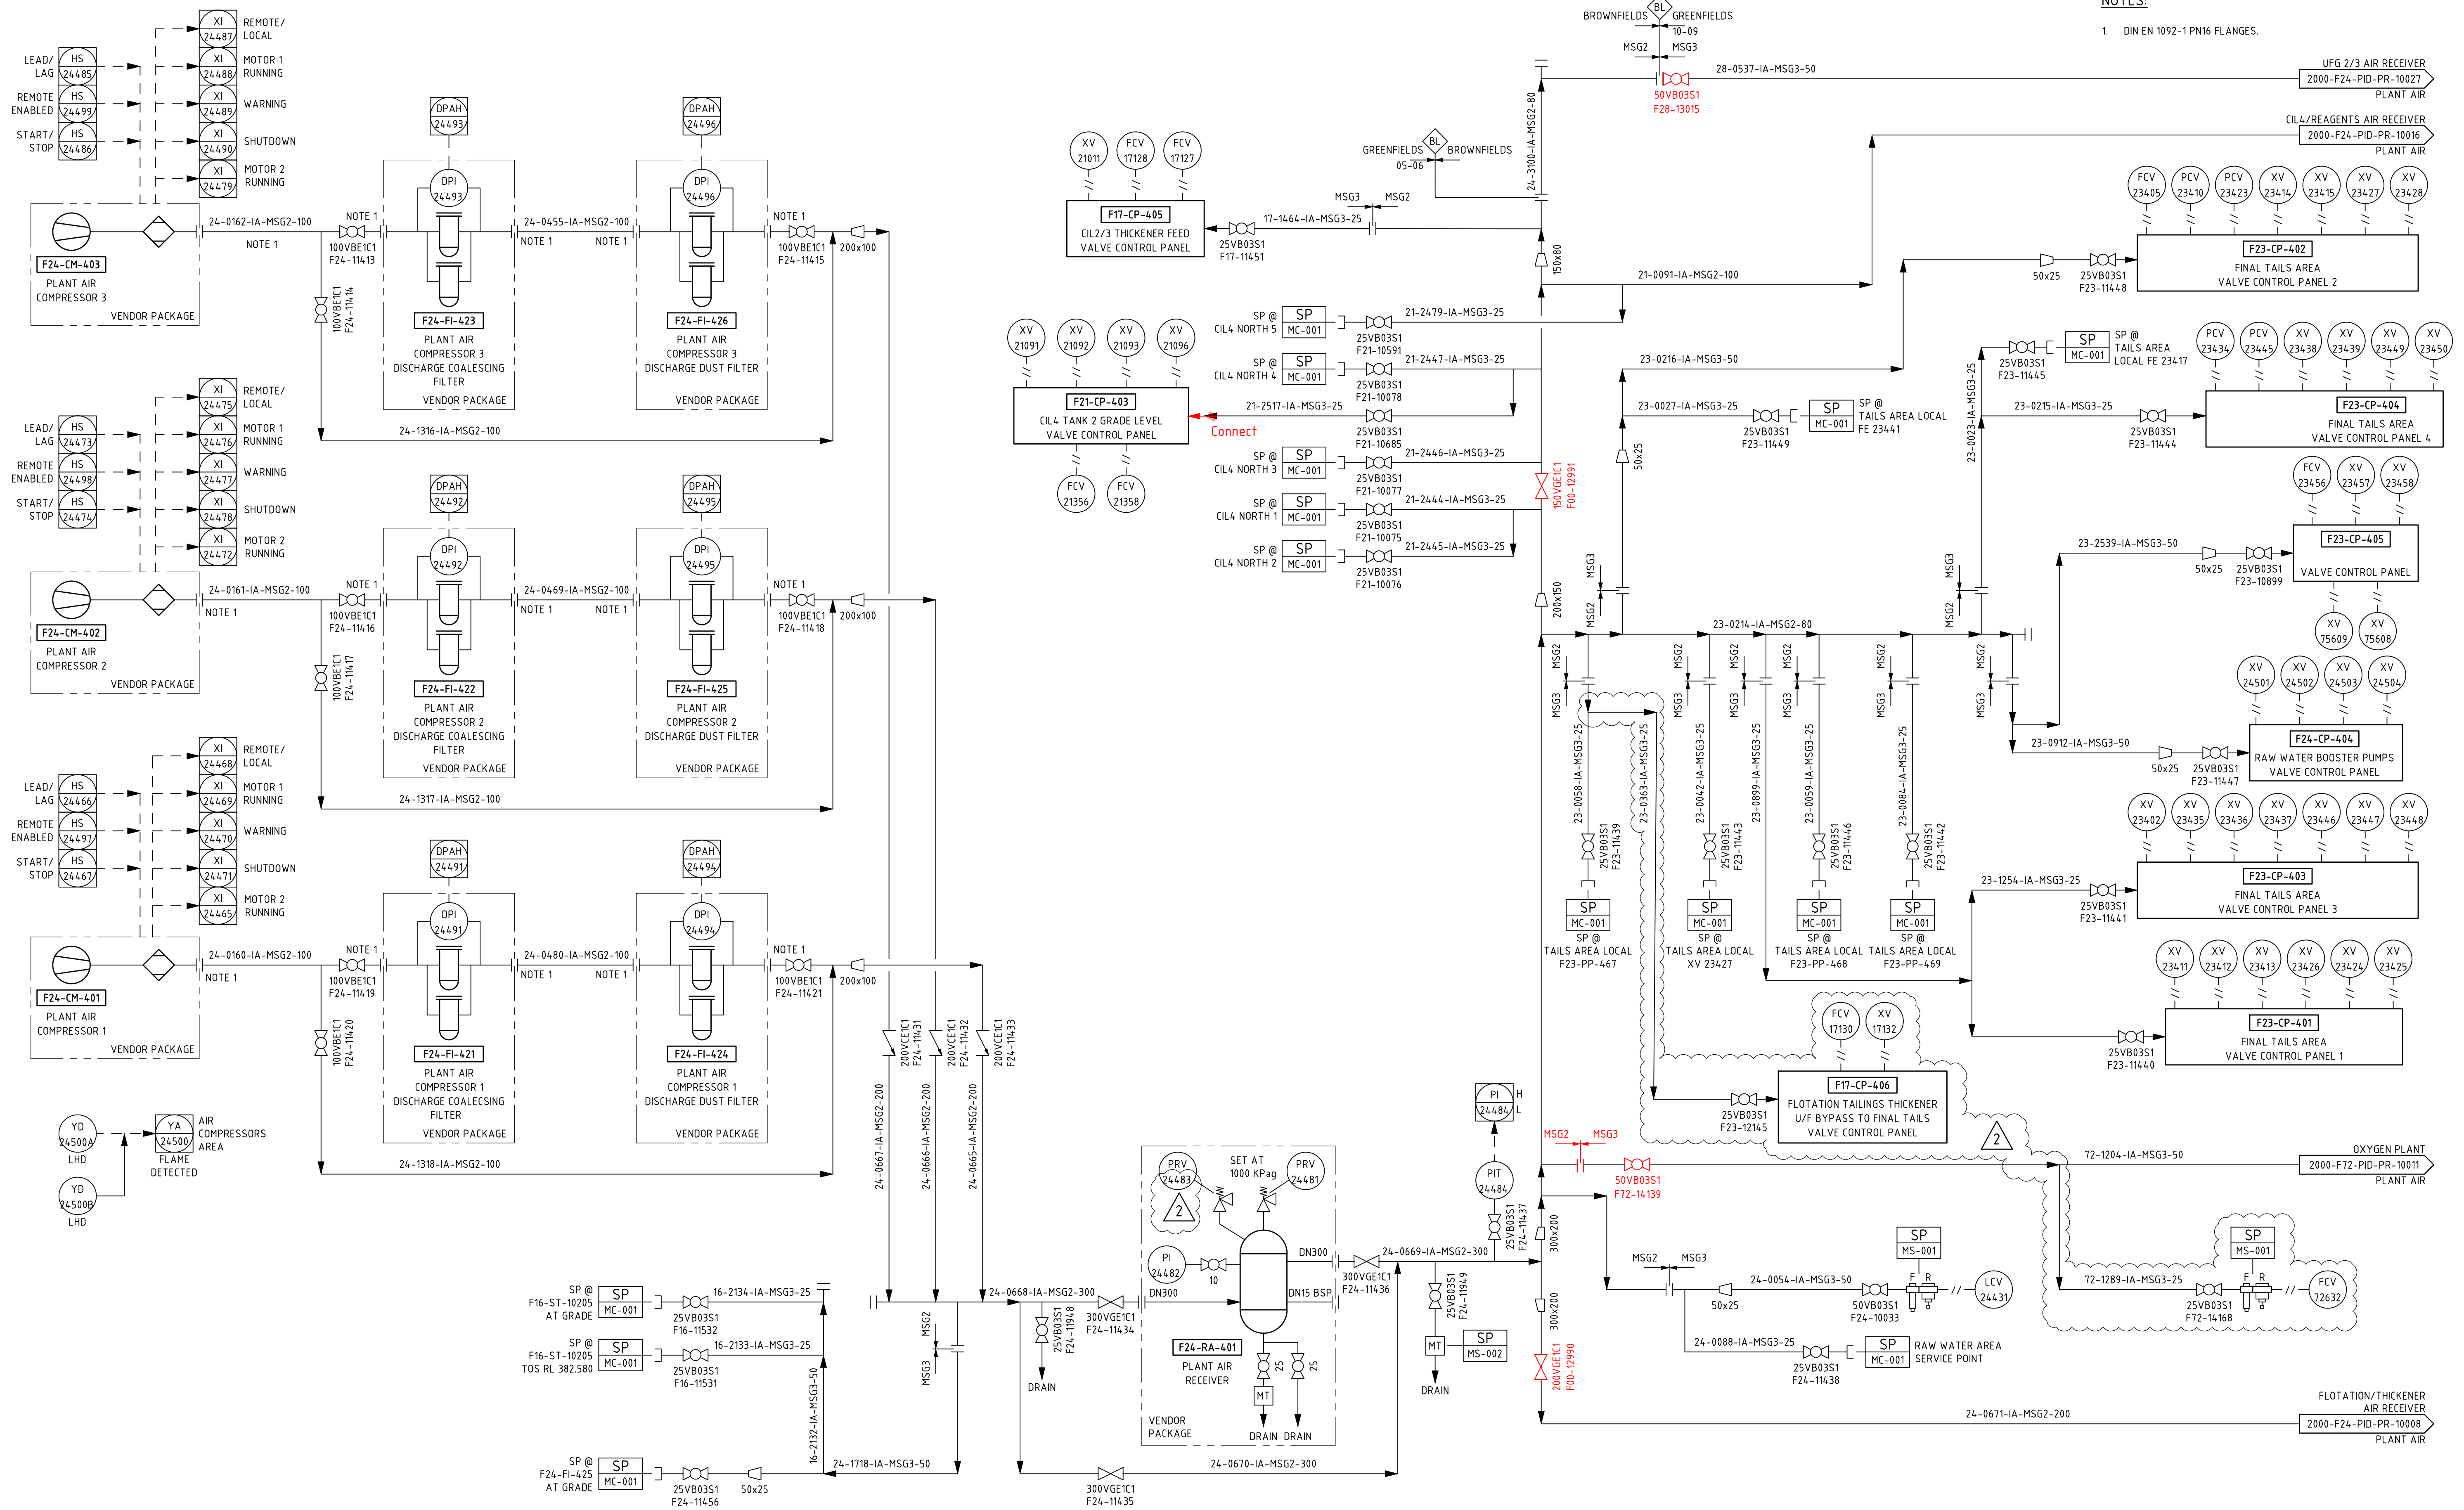

NOTES:

- DIN EN 1092-1 PN16 FLANGES.