


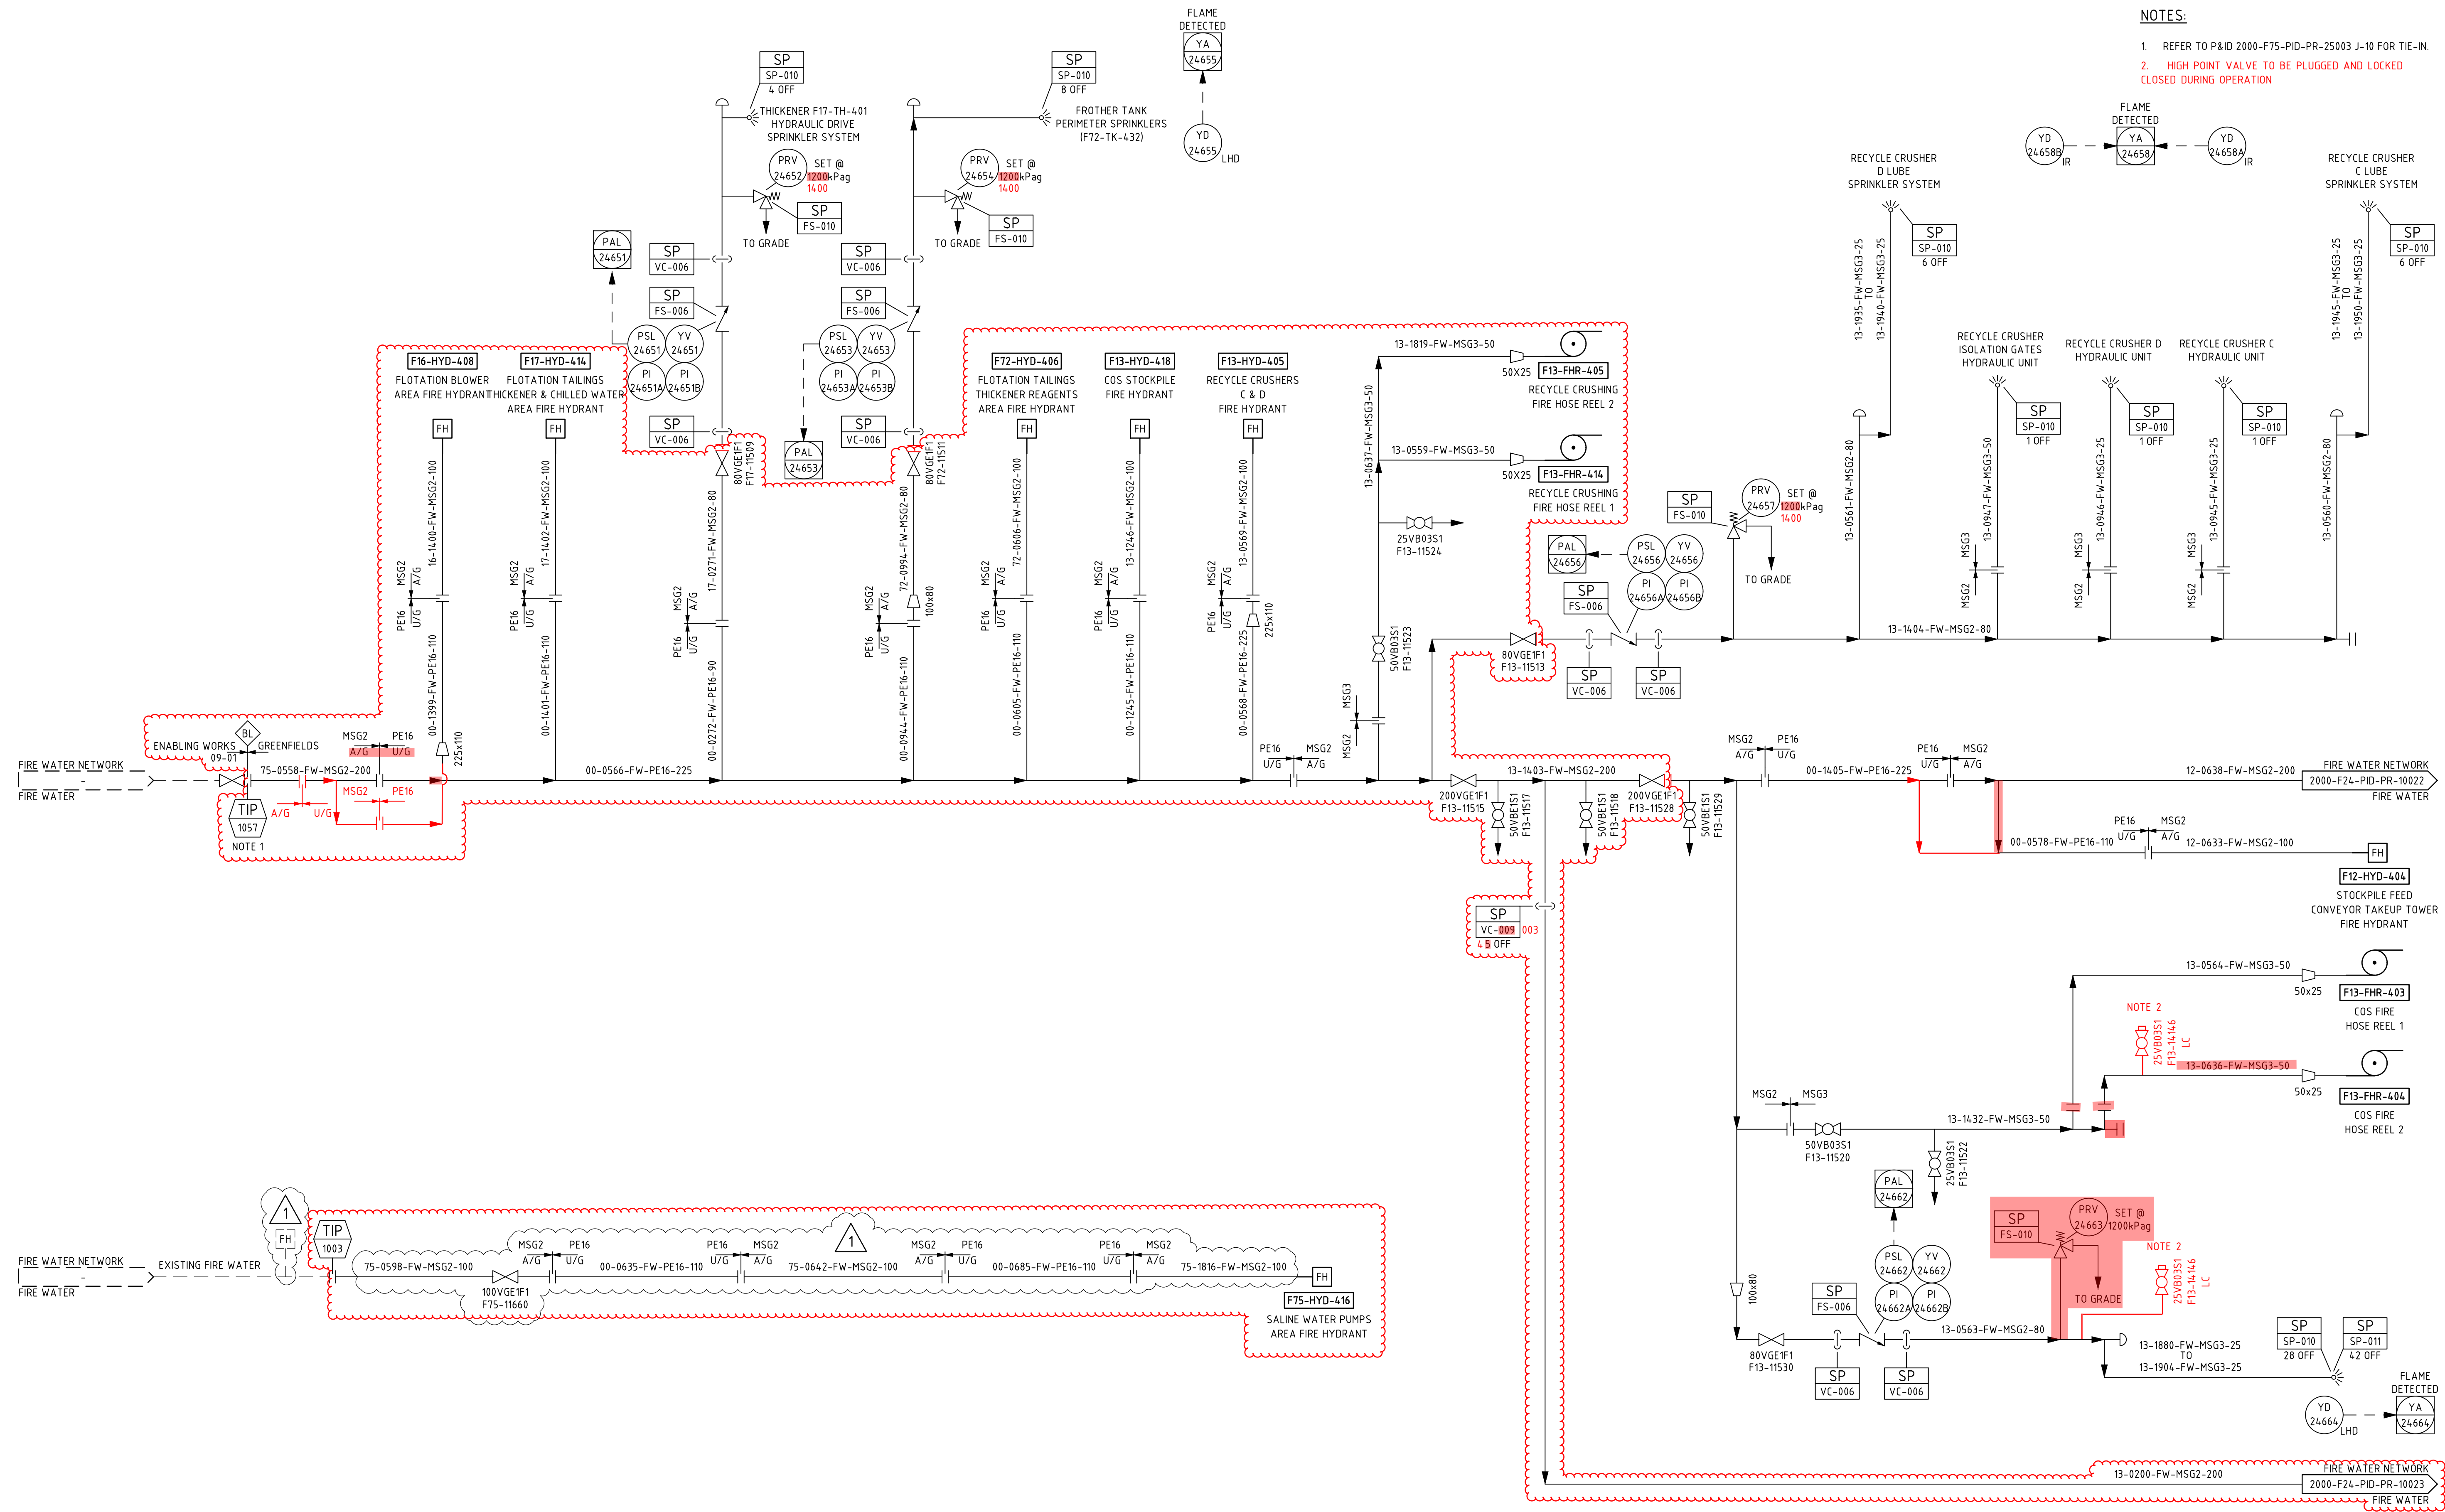

- NOTES:
1. REFER TO P&ID 2000-F75-PID-PR-25003 J-10 FOR TIE-IN.
 2. HIGH POINT VALVE TO BE PLUGGED AND LOCKED CLOSED DURING OPERATION