


NOTES:

1. REFER TO 2000-F24-PID-PR-10003 AND 2000-F24-PID-PR-10014 FOR THE GREENFIELDS LOW PRESSURE GLAND SEAL WATER CIRCUIT.
2. REFER TO 2000-F24-PID-PR-10004 AND 2000-F24-PID-PR-10014 FOR THE GREENFIELDS HIGH PRESSURE GLAND SEAL WATER CIRCUIT.
3. PUMPS REQUIRING GLAND WATER THAT ARE WITHIN BROWNFIELDS SCOPE ARE TO TIE IN TO THE EXISTING GLAND WATER CIRCUIT. REFER TO 2000-F75-PID-PR-10007 FOR THE BROWNFIELDS GLAND WATER CIRCUIT.
4. VALVE SIZE MATCHES LINE SIZE UNLESS OTHERWISE SPECIFIED IN THE RELEVANT GLAND WATER DETAIL.
5. LP REFERS TO THE GREENFIELDS LOW PRESSURE GLAND WATER CIRCUIT, HP REFERS TO THE GREENFIELDS LOW PRESSURE GLAND WATER CIRCUIT, HP REFERS TO THE BROWNFIELDS GLAND WATER CIRCUIT AND BF REFERS TO THE BROWNFIELDS GLAND WATER CIRCUIT.
6. REDUCING BUSH REQUIRED BETWEEN HOSE AND PUMP CONNECTION.

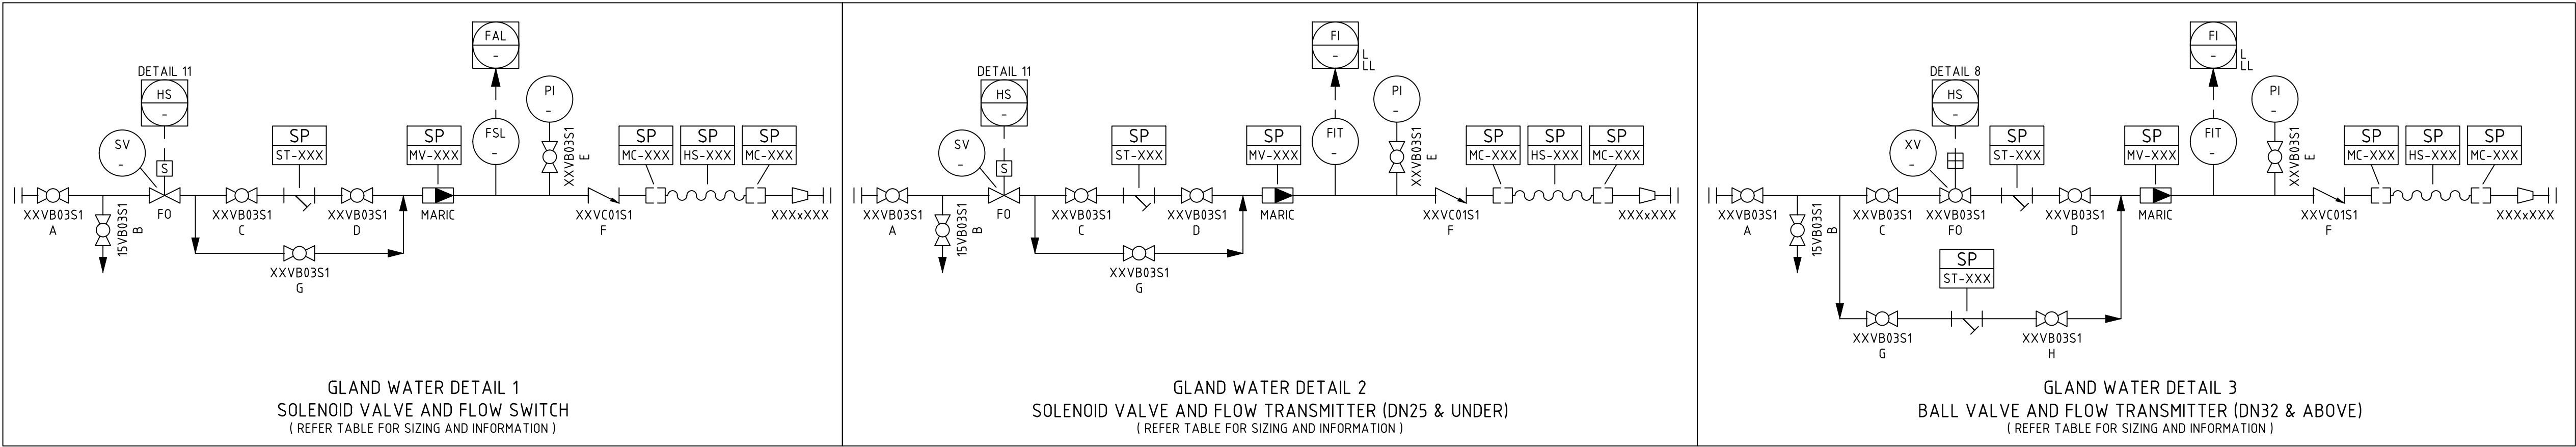

| EQUIPMENT DETAILS |                                            |                       |                     |        |                    | MANUAL VALVE TAG NUMBERS |           |           |           |           |           |           |   | INSTRUMENTATION |         |       | SPECIAL PIPING ITEMS |       |       |       |         |  |
|-------------------|--------------------------------------------|-----------------------|---------------------|--------|--------------------|--------------------------|-----------|-----------|-----------|-----------|-----------|-----------|---|-----------------|---------|-------|----------------------|-------|-------|-------|---------|--|
| EQUIPMENT NUMBER  | PUMP DESCRIPTION                           | P&ID NUMBER           | LINE SIZE<br>NOTE 4 | DETAIL | HP/LP/BF<br>NOTE 5 | A                        | B         | C         | D         | E         | F         | G         | H | XV/SV/HS        | FSL/FAL | PI    | SP-MV                | SP-ST | SP-MC | SP-HS | REDUCER |  |
| F21-PP-478        | CIL4 TANK 1 OXYGEN INJECTION PUMP          | 2000-F21-PID-PR-10001 | 25                  | 1      | LP                 | F21-10570                | F21-10571 | F21-10572 | F21-10573 | F21-10575 | F21-10576 | F21-10574 | - | 21320           | 21321   | 21322 | 002                  | 011   | 001   | 015   | N/A     |  |
| F21-PP-491        | CIL4 TANK 2 OXYGEN INJECTION PUMP          | 2000-F21-PID-PR-10001 | 25                  | 1      | LP                 | F21-10577                | F21-10578 | F21-10579 | F21-10580 | F21-10582 | F21-10583 | F21-10581 | - | 21324           | 21325   | 21326 | 002                  | 011   | 001   | 015   | N/A     |  |
| F22-PP-490        | CIL4 BARREN CARBON PUMP                    | 2000-F22-PID-PR-10005 | 25                  | 1      | LP                 | F22-10584                | F22-10585 | F22-10586 | F22-10587 | F22-10589 | F22-10590 | F22-10588 | - | 22260           | 22261   | 22262 | 001                  | 011   | 001   | 015   | 25x8    |  |
| F28-PP-461        | UFG MILL 3 FEED PUMP                       | 2000-F28-PID-PR-10003 | 25                  | 1      | HP                 | F28-11921                | F28-11922 | F28-11923 | F28-11924 | F28-11926 | F28-11927 | F28-11925 | - | 28433           | 28434   | 28435 | 005                  | 011   | 001   | 015   | 25x8    |  |
| F28-PW-431        | UFG MILL 3 ISACHARGER PUMP                 | 2000-F28-PID-PR-10003 | 25                  | 1      | HP                 | F28-11935                | F28-11936 | F28-11937 | F28-11938 | F28-11940 | F28-11941 | F28-11939 | - | 28430           | 28431   | 28432 | 002                  | 011   | 001   | 015   | 25x10   |  |
| F28-PP-463        | UFG MILL 3 DISCHARGE PUMP                  | 2000-F28-PID-PR-10004 | 25                  | 1      | HP                 | F28-11907                | F28-11908 | F28-11909 | F28-11910 | F28-11912 | F28-11913 | F28-11911 | - | 28436           | 28437   | 28438 | 004                  | 011   | 001   | 015   | 25x15   |  |
| F72-PP-658        | SLAKED LIME TRANSFER PUMP 1                | 2000-F72-PID-PR-10001 | 25                  | 1      | HP                 | F72-10774                | F72-10775 | F72-10776 | F72-10777 | F72-10779 | F72-10780 | F72-10778 | - | 72492           | 72493   | 72494 | 005                  | 011   | 001   | 015   | 25x8    |  |
| F72-PP-659        | SLAKED LIME TRANSFER PUMP 2                | 2000-F72-PID-PR-10002 | 25                  | 1      | HP                 | F72-10809                | F72-10810 | F72-10811 | F72-10812 | F72-10814 | F72-10815 | F72-10813 | - | 72495           | 72496   | 72497 | 005                  | 011   | 001   | 015   | 25x8    |  |
| F72-PP-656        | LIME RINGMAIN PUMP 1                       | 2000-F72-PID-PR-10003 | 25                  | 1      | HP                 | F72-10781                | F72-10782 | F72-10783 | F72-10784 | F72-10786 | F72-10787 | F72-10785 | - | 72470           | 72471   | 72472 | 005                  | 011   | 001   | 015   | 25x8    |  |
| F72-PP-657        | LIME RINGMAIN PUMP 2                       | 2000-F72-PID-PR-10003 | 25                  | 1      | HP                 | F72-10788                | F72-10789 | F72-10790 | F72-10791 | F72-10793 | F72-10794 | F72-10792 | - | 72474           | 72475   | 72476 | 005                  | 011   | 001   | 015   | 25x8    |  |
| F30-PP-415        | CONCENTRATE PRE-LEACH THICKENER U/F PUMP 1 | 2000-F30-PID-PR-10004 | 25                  | 1      | BF                 | F30-10598                | F30-10599 | F30-10600 | F30-10601 | F30-10603 | F30-10604 | F30-10602 | - | 30403           | 30404   | 30405 | 001                  | 011   | 001   | 015   | 25x8    |  |
| F30-PP-416        | CONCENTRATE PRE-LEACH THICKENER U/F PUMP 2 | 2000-F30-PID-PR-10004 | 25                  | 1      | BF                 | F30-10605                | F30-10606 | F30-10607 | F30-10608 | F30-10610 | F30-10611 | F30-10609 | - | 30408           | 30409   | 30410 | 001                  | 011   | 001   | 015   | 25x8    |  |
| F30-PP-426        | CONCENTRATE LEACH TRANSFER PUMP 1          | 2000-F30-PID-PR-10006 | 25                  | 1      | BF                 | F30-10612                | F30-10613 | F30-10614 | F30-10615 | F30-10617 | F30-10618 | F30-10616 | - | 30434           | 30435   | 30436 | 005                  | 011   | 001   | 015   | 25x8    |  |
| F30-PP-427        | CONCENTRATE LEACH TRANSFER PUMP 2          | 2000-F30-PID-PR-10006 | 25                  | 1      | BF                 | F30-10619                | F30-10620 | F30-10621 | F30-10622 | F30-10624 | F30-10625 | F30-10623 | - | 30440           | 30441   | 30442 | 005                  | 011   | 001   | 015   | 25x8    |  |
| F30-TK32A-PP01    | CIL2 TANK 1 OXYGEN INJECTION PUMP          | 2000-F30-PID-PR-10007 | 25                  | 1      | BF                 | F30-10563                | F30-10564 | F30-10565 | F30-10566 | F30-10568 | F30-10569 | F30-10567 | - | 30552           | 30553   | 30554 | 002                  | 011   | 001   | 015   | N/A     |  |
| F30-TK32B-PP01    | CIL2 TANK 2 OXYGEN INJECTION PUMP          | 2000-F30-PID-PR-10007 | 25                  | 1      | BF                 | F30-10795                | F30-10796 | F30-10797 | F30-10798 | F30-10800 | F30-10801 | F30-10799 | - | 30567           | 30568   | 30569 | 002                  | 011   | 001   | 015   | N/A     |  |
| F30-PP-428        | CIL3 TAILS PUMP 1                          | 2000-F30-PID-PR-10011 | 25                  | 1      | BF                 | F30-10626                | F30-10627 | F30-10628 | F30-10629 | F30-10631 | F30-10632 | F30-10630 | - | 30466           | 30467   | 30468 | 005                  | 011   | 001   | 015   | 25x8    |  |
| F30-PP-429        | CIL3 TAILS PUMP 2                          | 2000-F30-PID-PR-10011 | 25                  | 1      | BF                 | F30-10633                | F30-10634 | F30-10635 | F30-10636 | F30-10638 | F30-10639 | F30-10637 | - | 30472           | 30473   | 30474 | 005                  | 011   | 001   | 015   | 25x8    |  |
| F65-PP-481        | CIL3 LOADED CARBON PUMP                    | 2000-F30-PID-PR-10017 | 25                  | 1      | BF                 | F65-10802                | F65-10803 | F65-10804 | F65-10805 | F65-10807 | F65-10808 | F65-10806 | - | 65408           | 65409   | 65410 | 001                  | 011   | 001   | 015   | 25x8    |  |
| F34-PP-443        | UFG MILL 1 PRODUCT PUMP                    | 2000-F34-PID-PR-10002 | 25                  | 1      | BF                 | F34-10760                | F34-10761 | F34-10762 | F34-10763 | F34-10765 | F34-10766 | F34-10764 | - | 34406           | 34407   | 34408 | 001                  | 011   | 001   | 015   | 25x8    |  |
| F35-PP-449        | UFG CIRCUIT 3 FEED PUMP                    | 2000-F35-PID-PR-10002 | 25                  | 1      | BF                 | F35-10767                | F35-10768 | F35-10769 | F35-10770 | F35-10772 | F35-10773 | F35-10771 | - | 35445           | 35446   | 35447 | 001                  | 011   | 001   | 015   | 25x8    |  |

1

1