


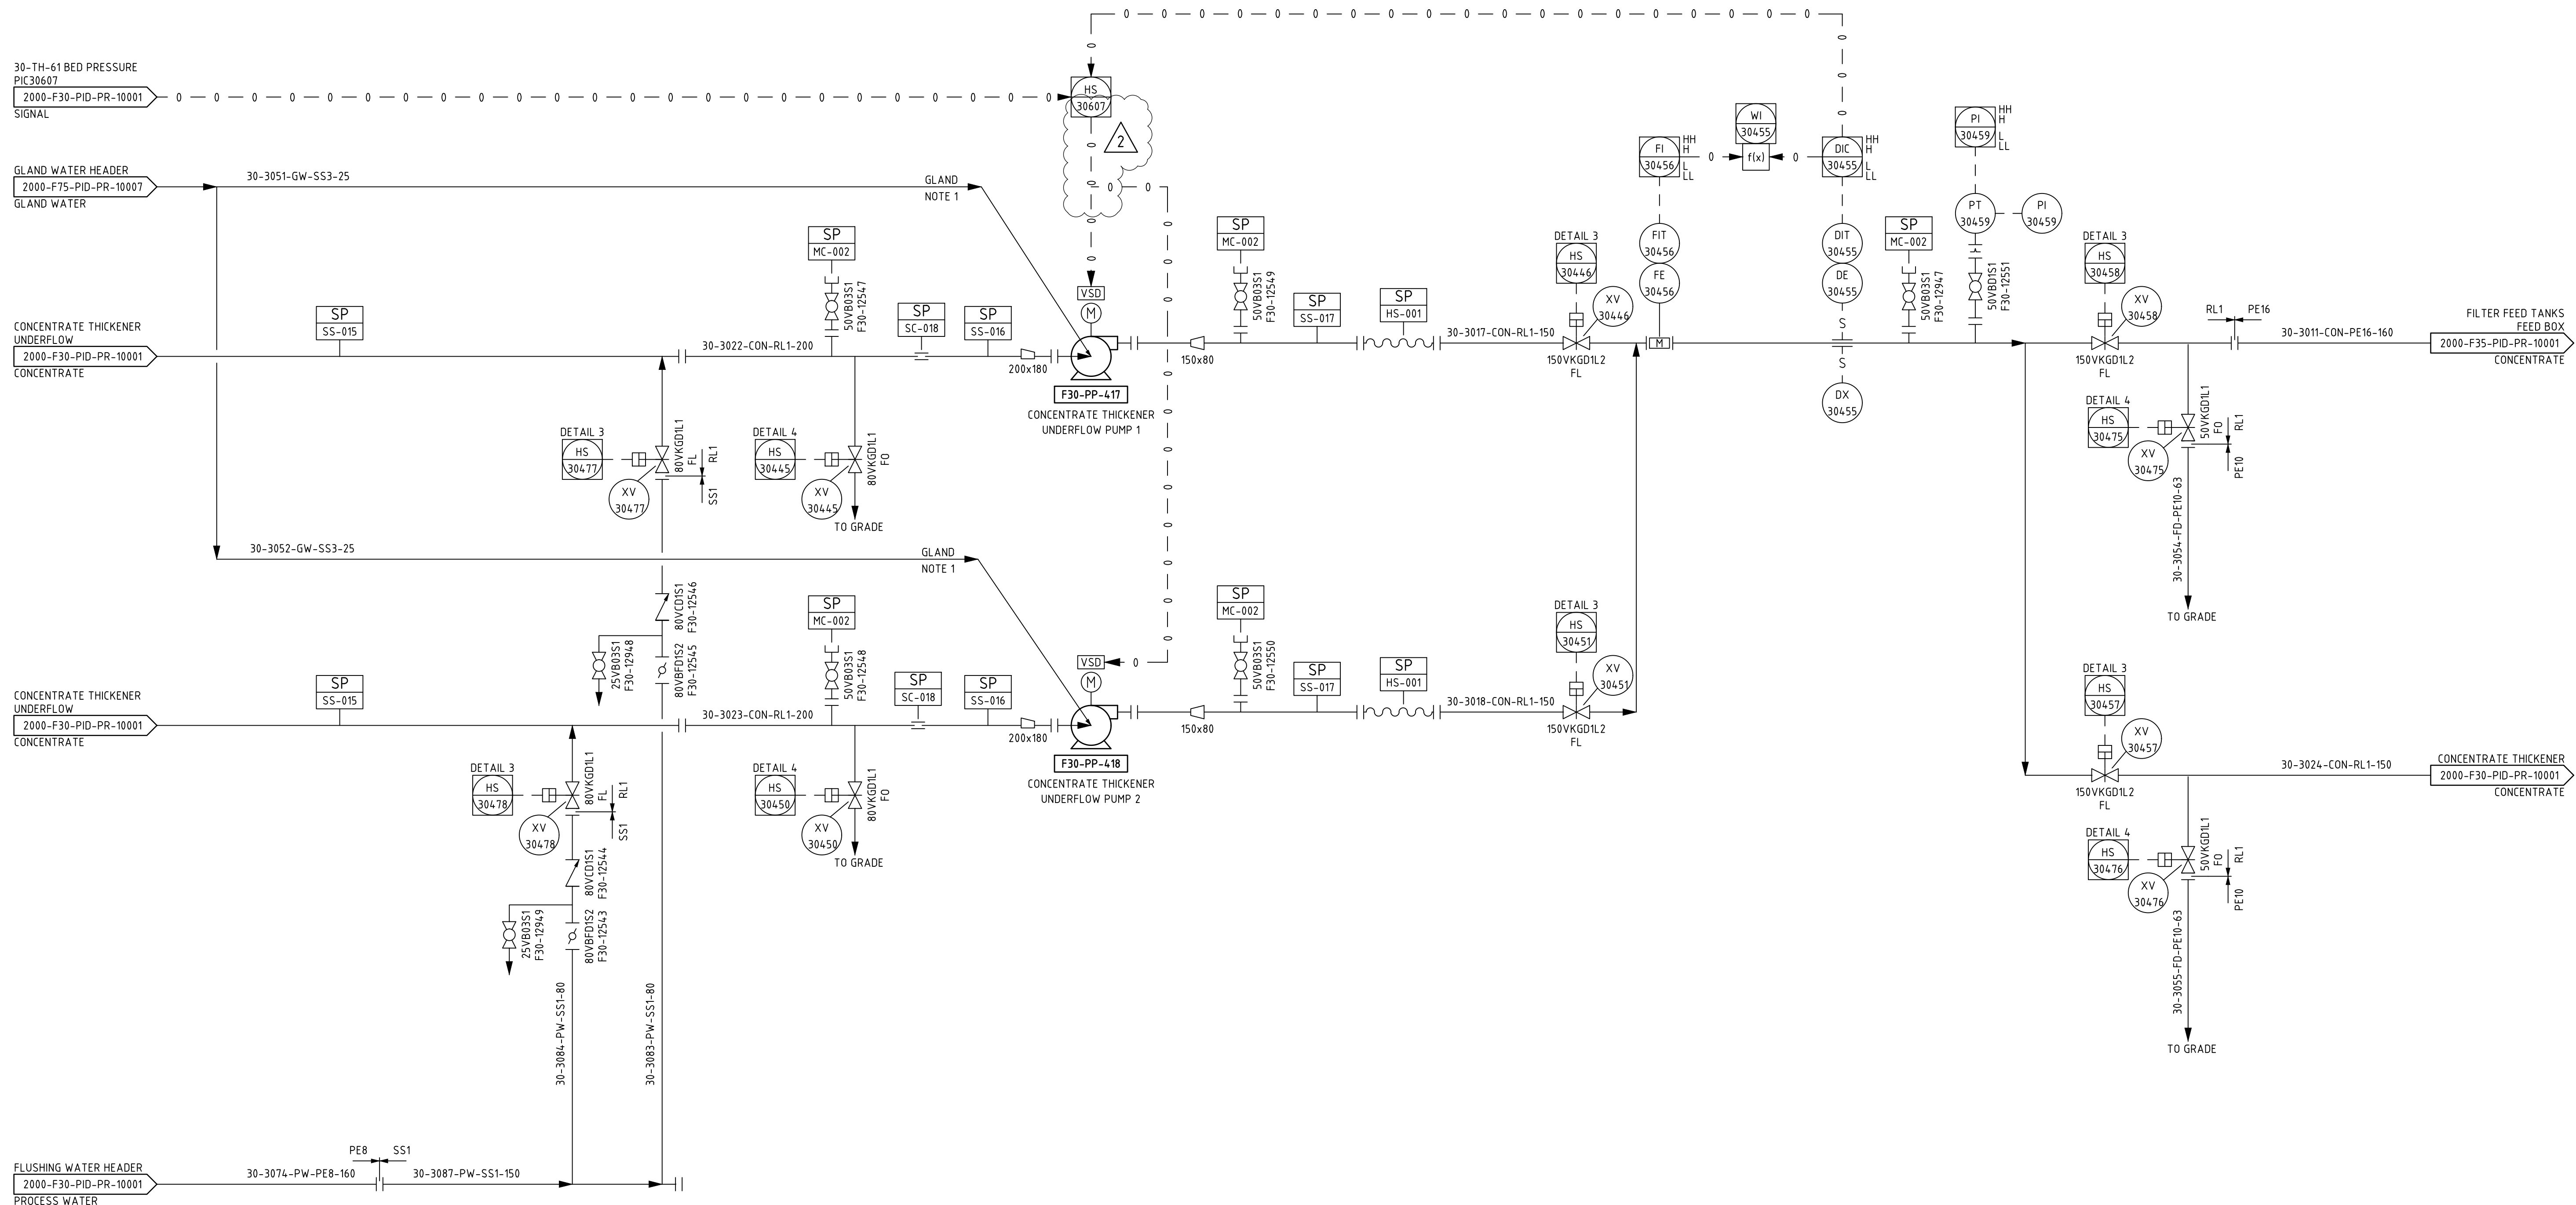

1. REFER TO 2000-F24-PID-PR-10034 FOR GLAND WATER DETAIL.
2. MINSUP POINT TO BE SITUATED CLOSE TO DENSITY GAUGE FOR COMMISSIONING.

1. REFER TO 2000-F24-PID-PR-10034 FOR GLAND WATER DETAIL.
2. MINSUP POINT TO BE SITUATED CLOSE TO DENSITY GAUGE FOR COMMISSIONING.