


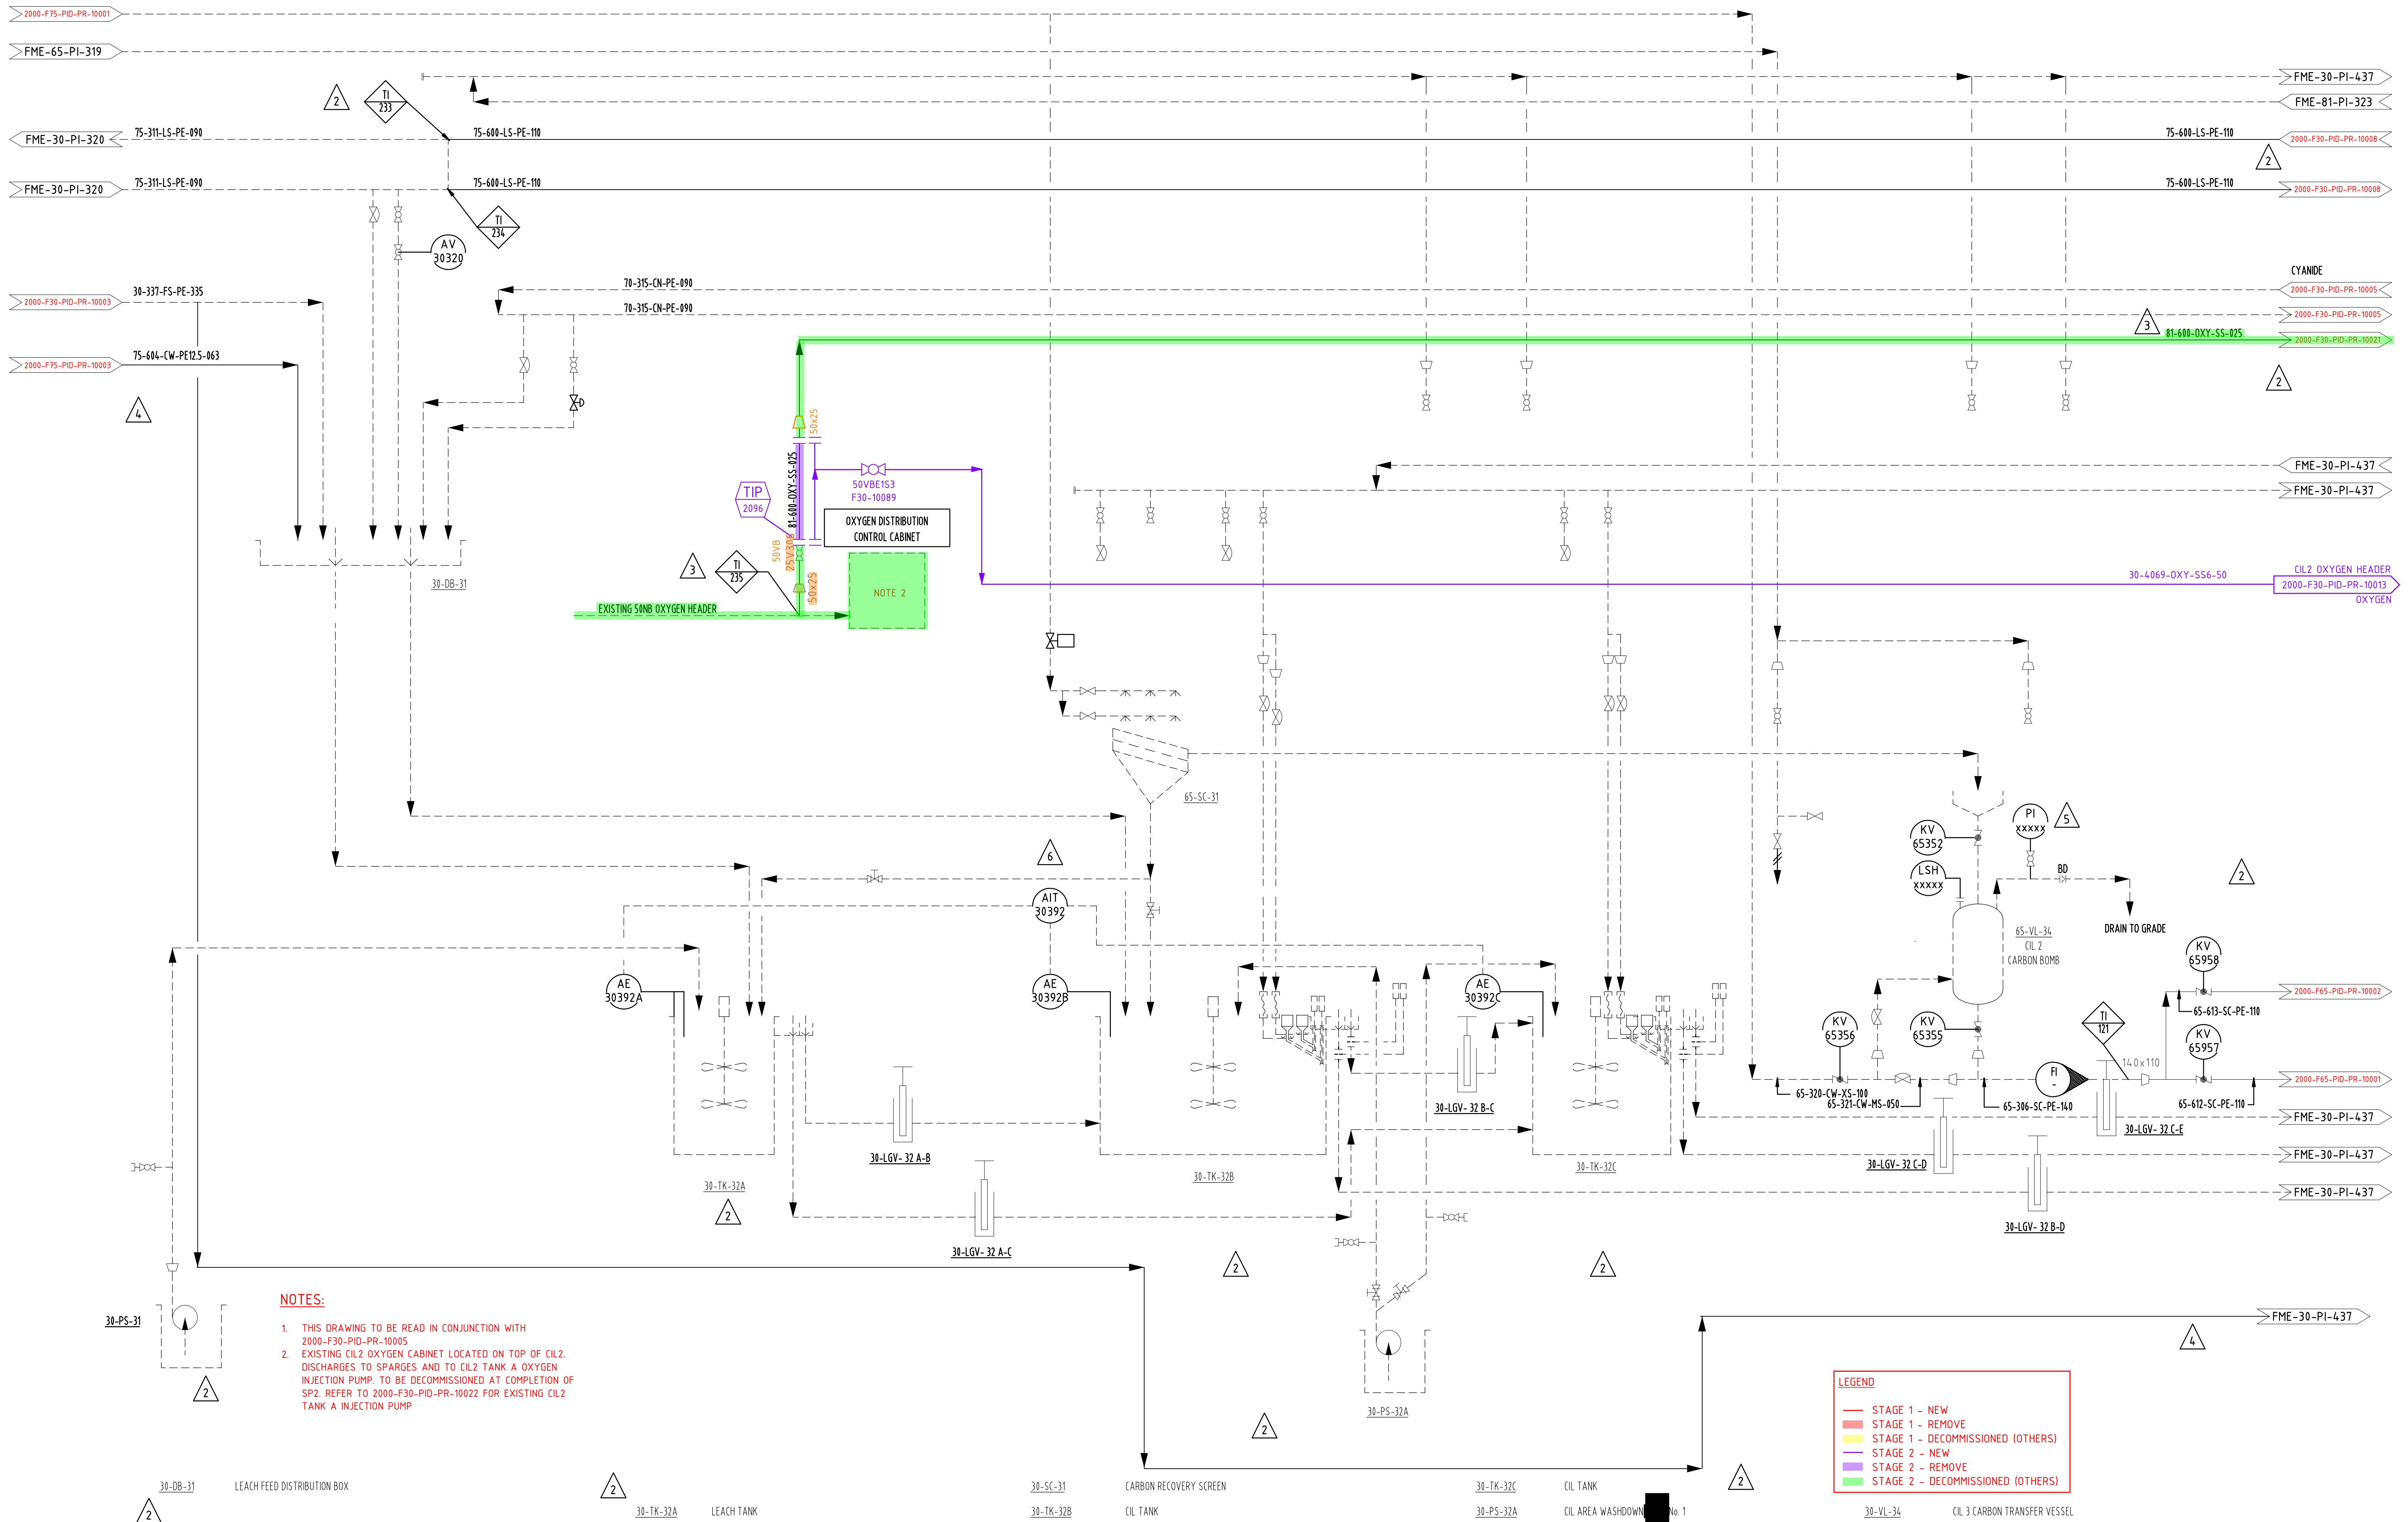

NOTES:

1. THIS DRAWING TO BE READ IN CONJUNCTION WITH 2000-F30-PID-PR-10005
2. EXISTING CIL2 OXYGEN CABINET LOCATED ON TOP OF CIL2. DISCHARGES TO SPARGES AND TO CIL2 TANK A OXYGEN INJECTION PUMP. TO BE DECOMMISSIONED AT COMPLETION OF SP2. REFER TO 2000-F30-PID-PR-10022 FOR EXISTING CIL2 TANK A INJECTION PUMP

LEGEND	
—	STAGE 1 - NEW
—	STAGE 1 - REMOVE
—	STAGE 1 - DECOMMISSIONED (OTHERS)
—	STAGE 2 - NEW
—	STAGE 2 - REMOVE
—	STAGE 2 - DECOMMISSIONED (OTHERS)