


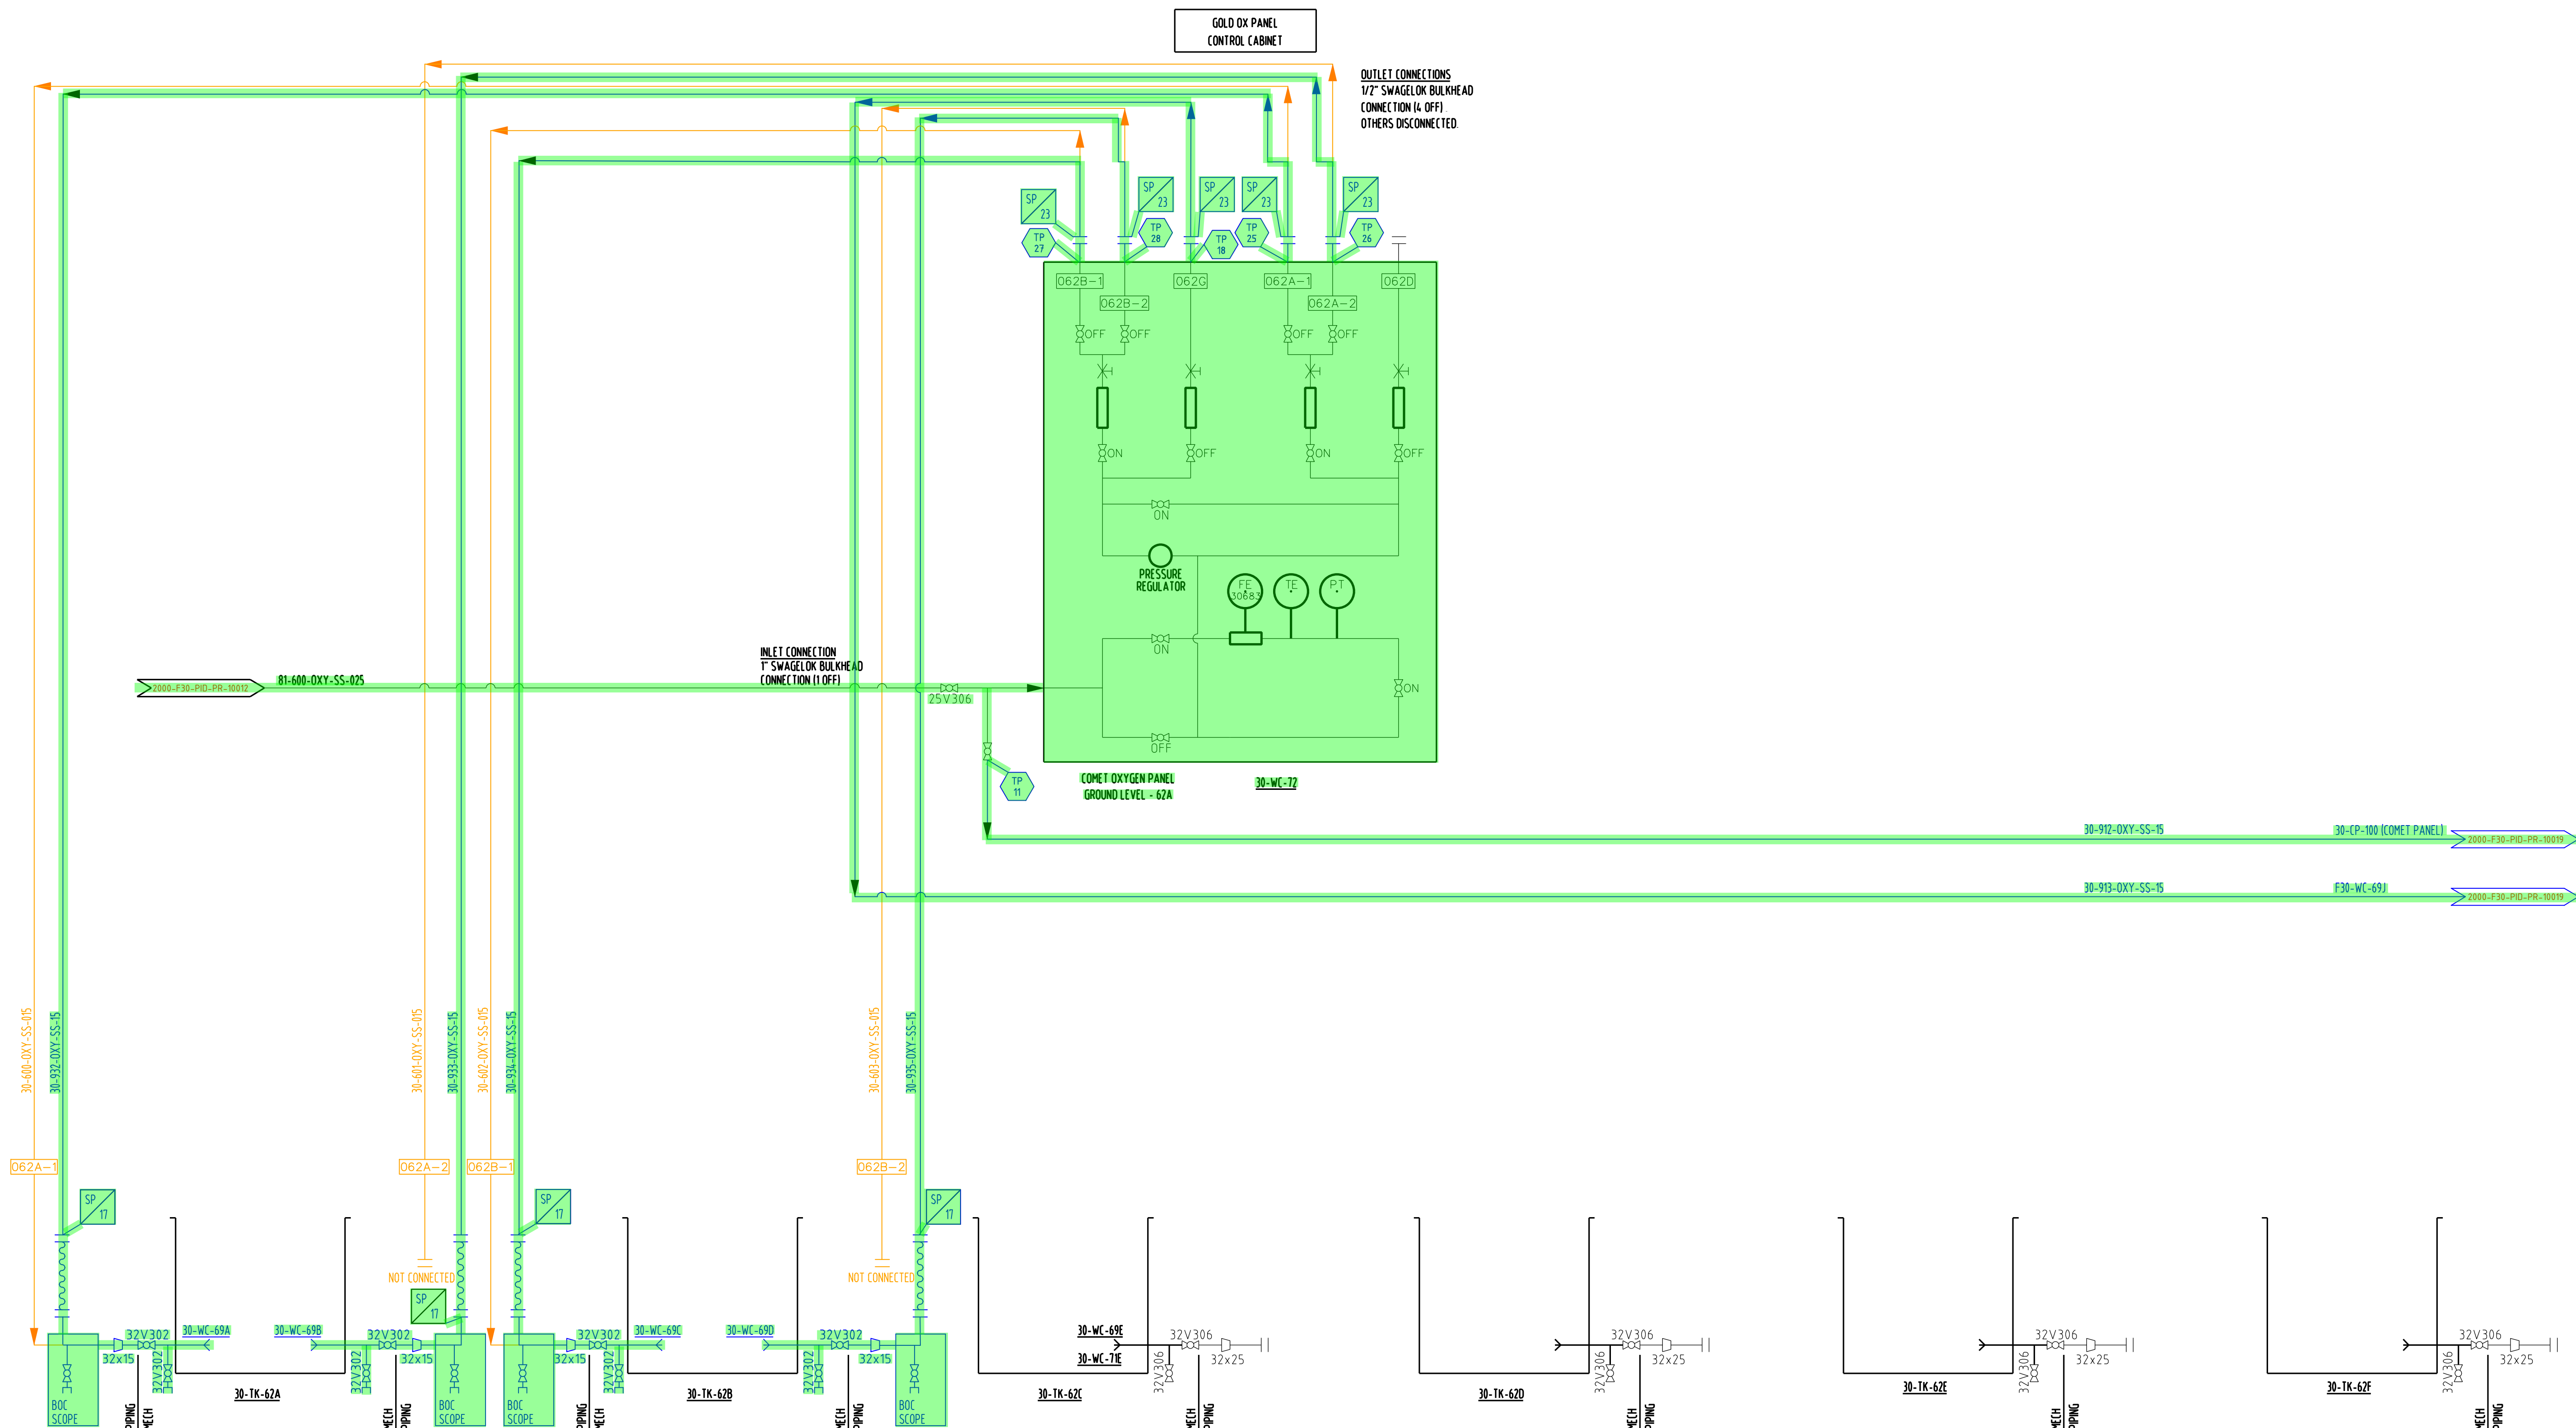

30-WC-69A CIL3 TANK A OXYGEN SPARGE 1
30-WC-69B CIL3 TANK A OXYGEN SPARGE 2
30-WC-69C CIL3 TANK B OXYGEN SPARGE 1
30-WC-69D CIL3 TANK B OXYGEN SPARGE 2
30-WC-72 OXYGEN SPARGE & PUMP CONTROL PANEL

LEGEND

EXISTING
NEW
DEMOLISH/MODIFY

EXISTING
NON-EXISTENT
STAGE 1 - NEW
STAGE 1 - REMOVE
STAGE 1 - DECOMMISSIONED (OTHERS)
STAGE 2 - NEW
STAGE 2 - REMOVE
STAGE 2 - DECOMMISSIONED (OTHERS)