


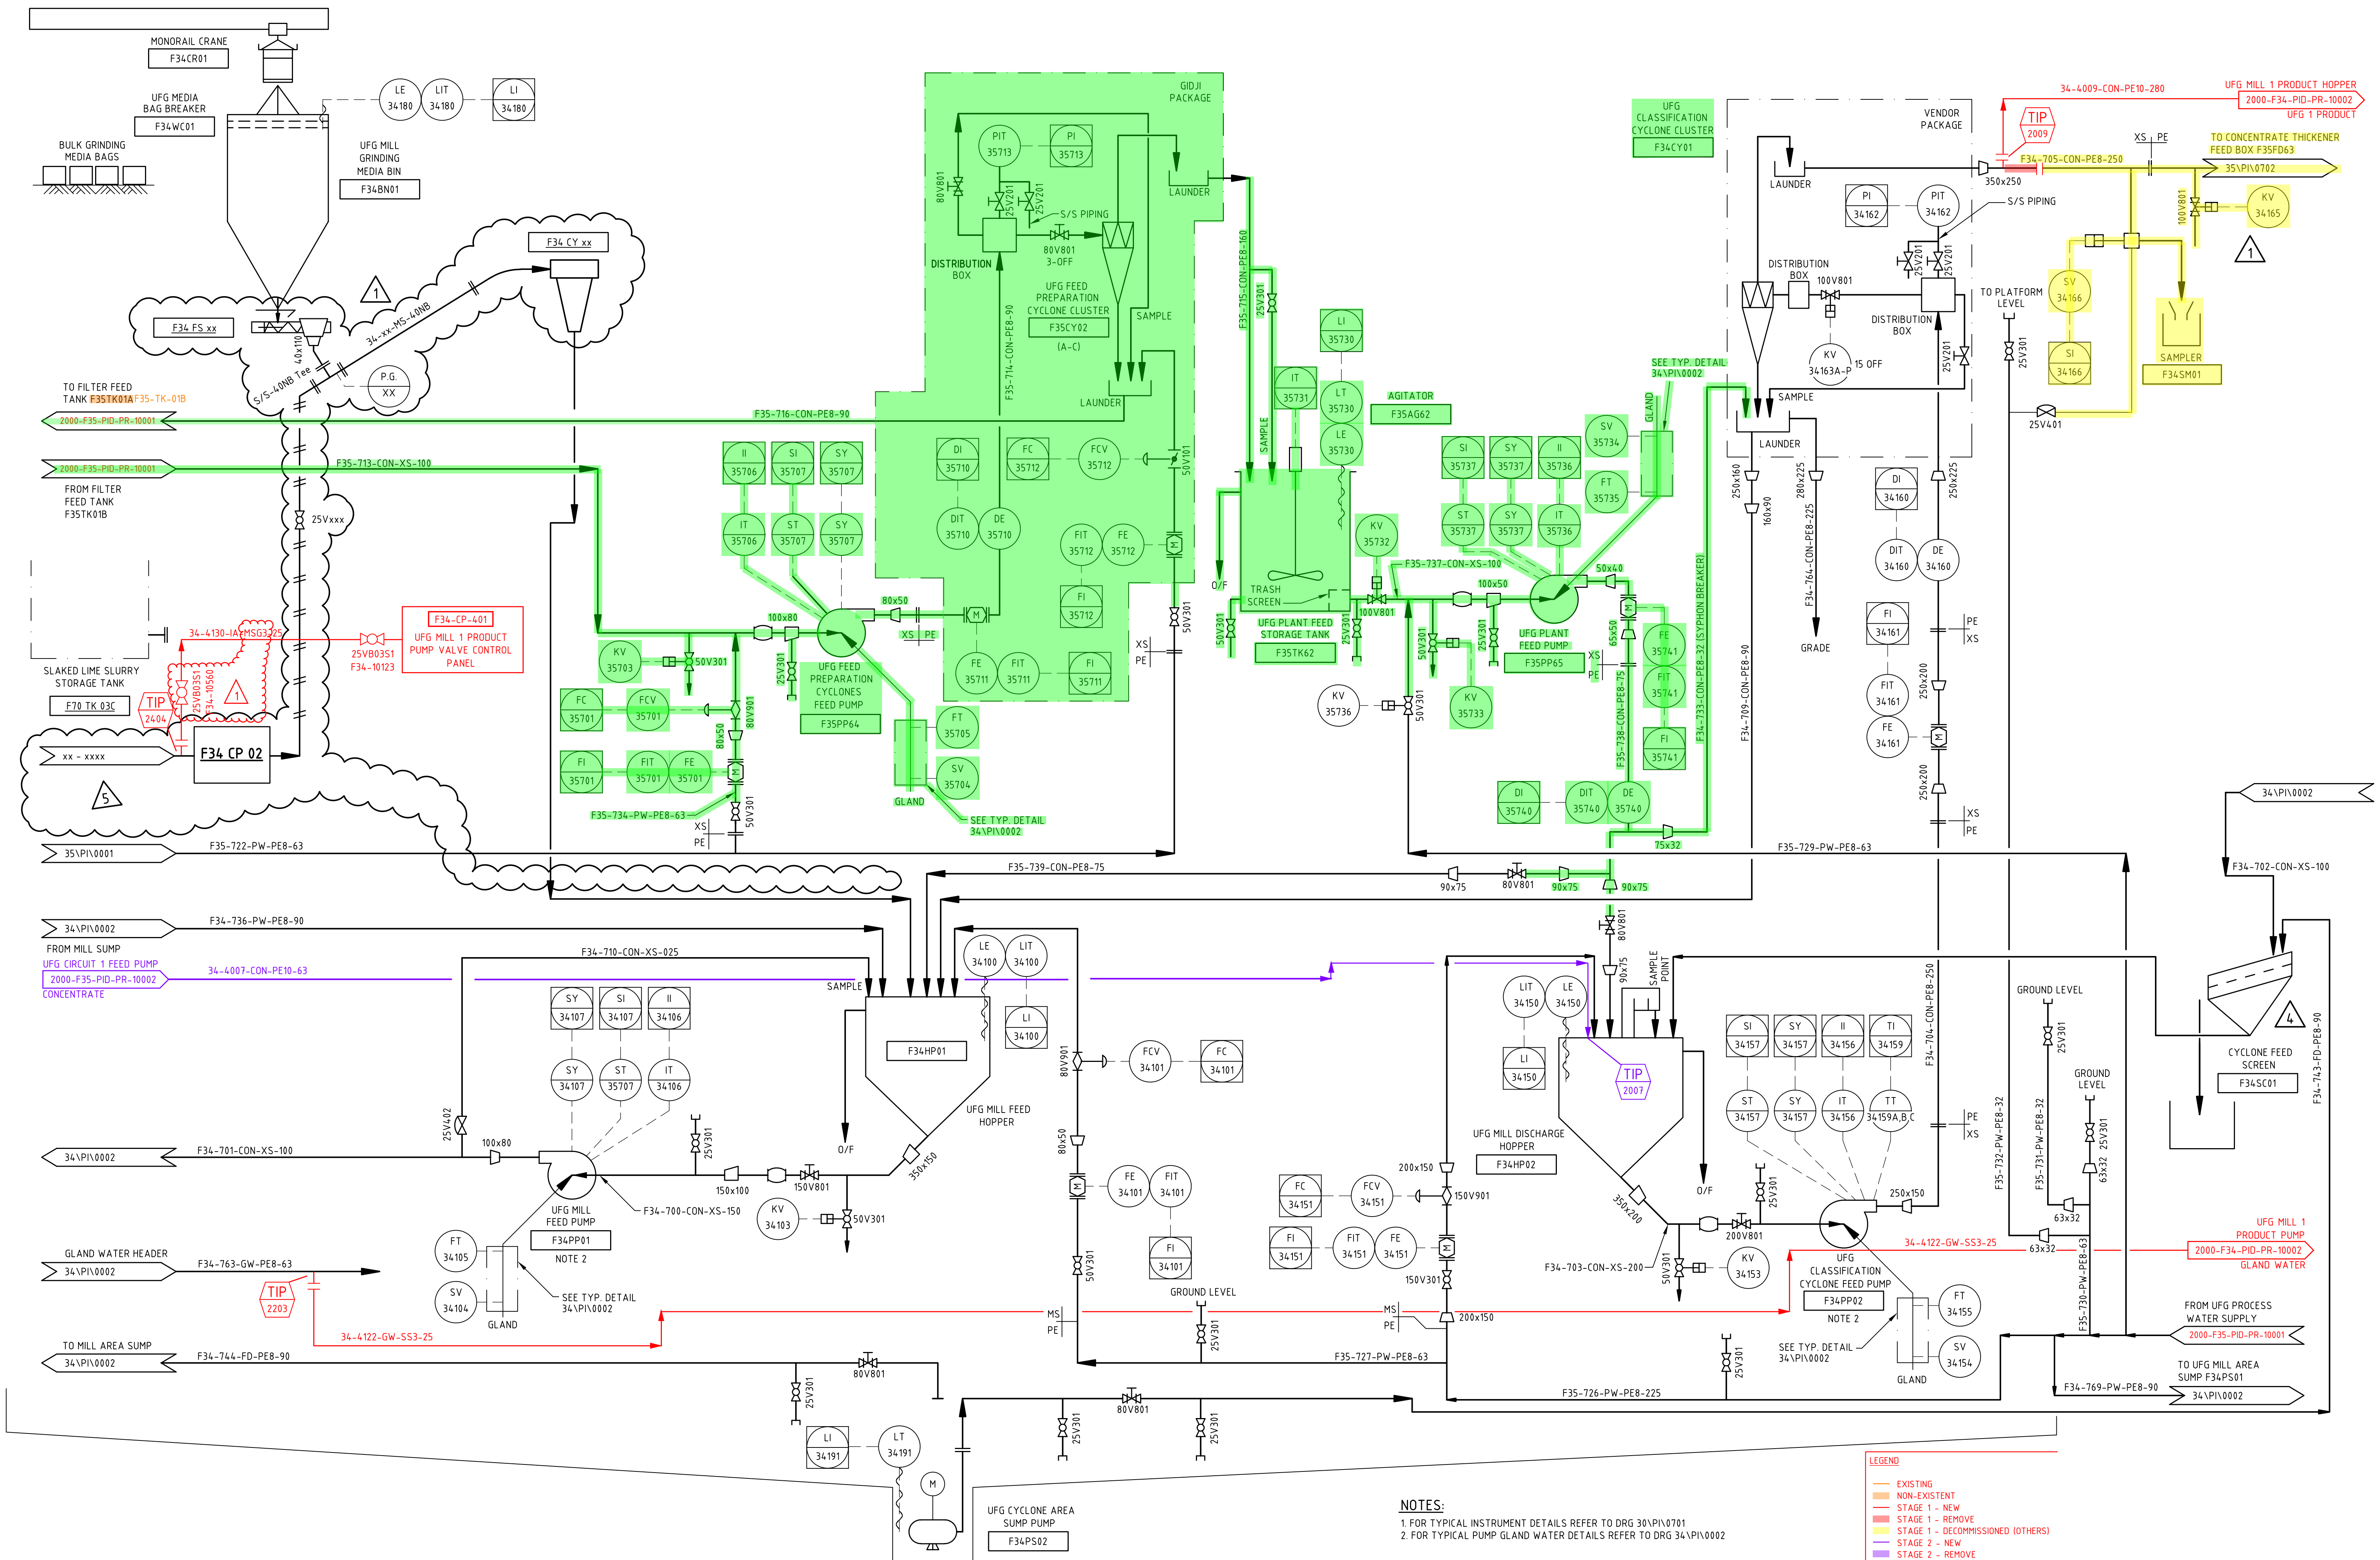

NOTES:

1. FOR TYPICAL INSTRUMENT DETAILS REFER TO DRG 30\PI\0701  
2. FOR TYPICAL PUMP GLAND WATER DETAILS REFER TO DRG 34\PI\0002

**LEGEND**

- EXISTING
- NON-EXISTENT
- STAGE 1 - NEW
- STAGE 1 - REMOVE
- STAGE 1 - DECOMMISSIONED (OTHERS)
- STAGE 2 - NEW
- STAGE 2 - REMOVE
- STAGE 2 - DECOMMISSIONED (OTHERS)