


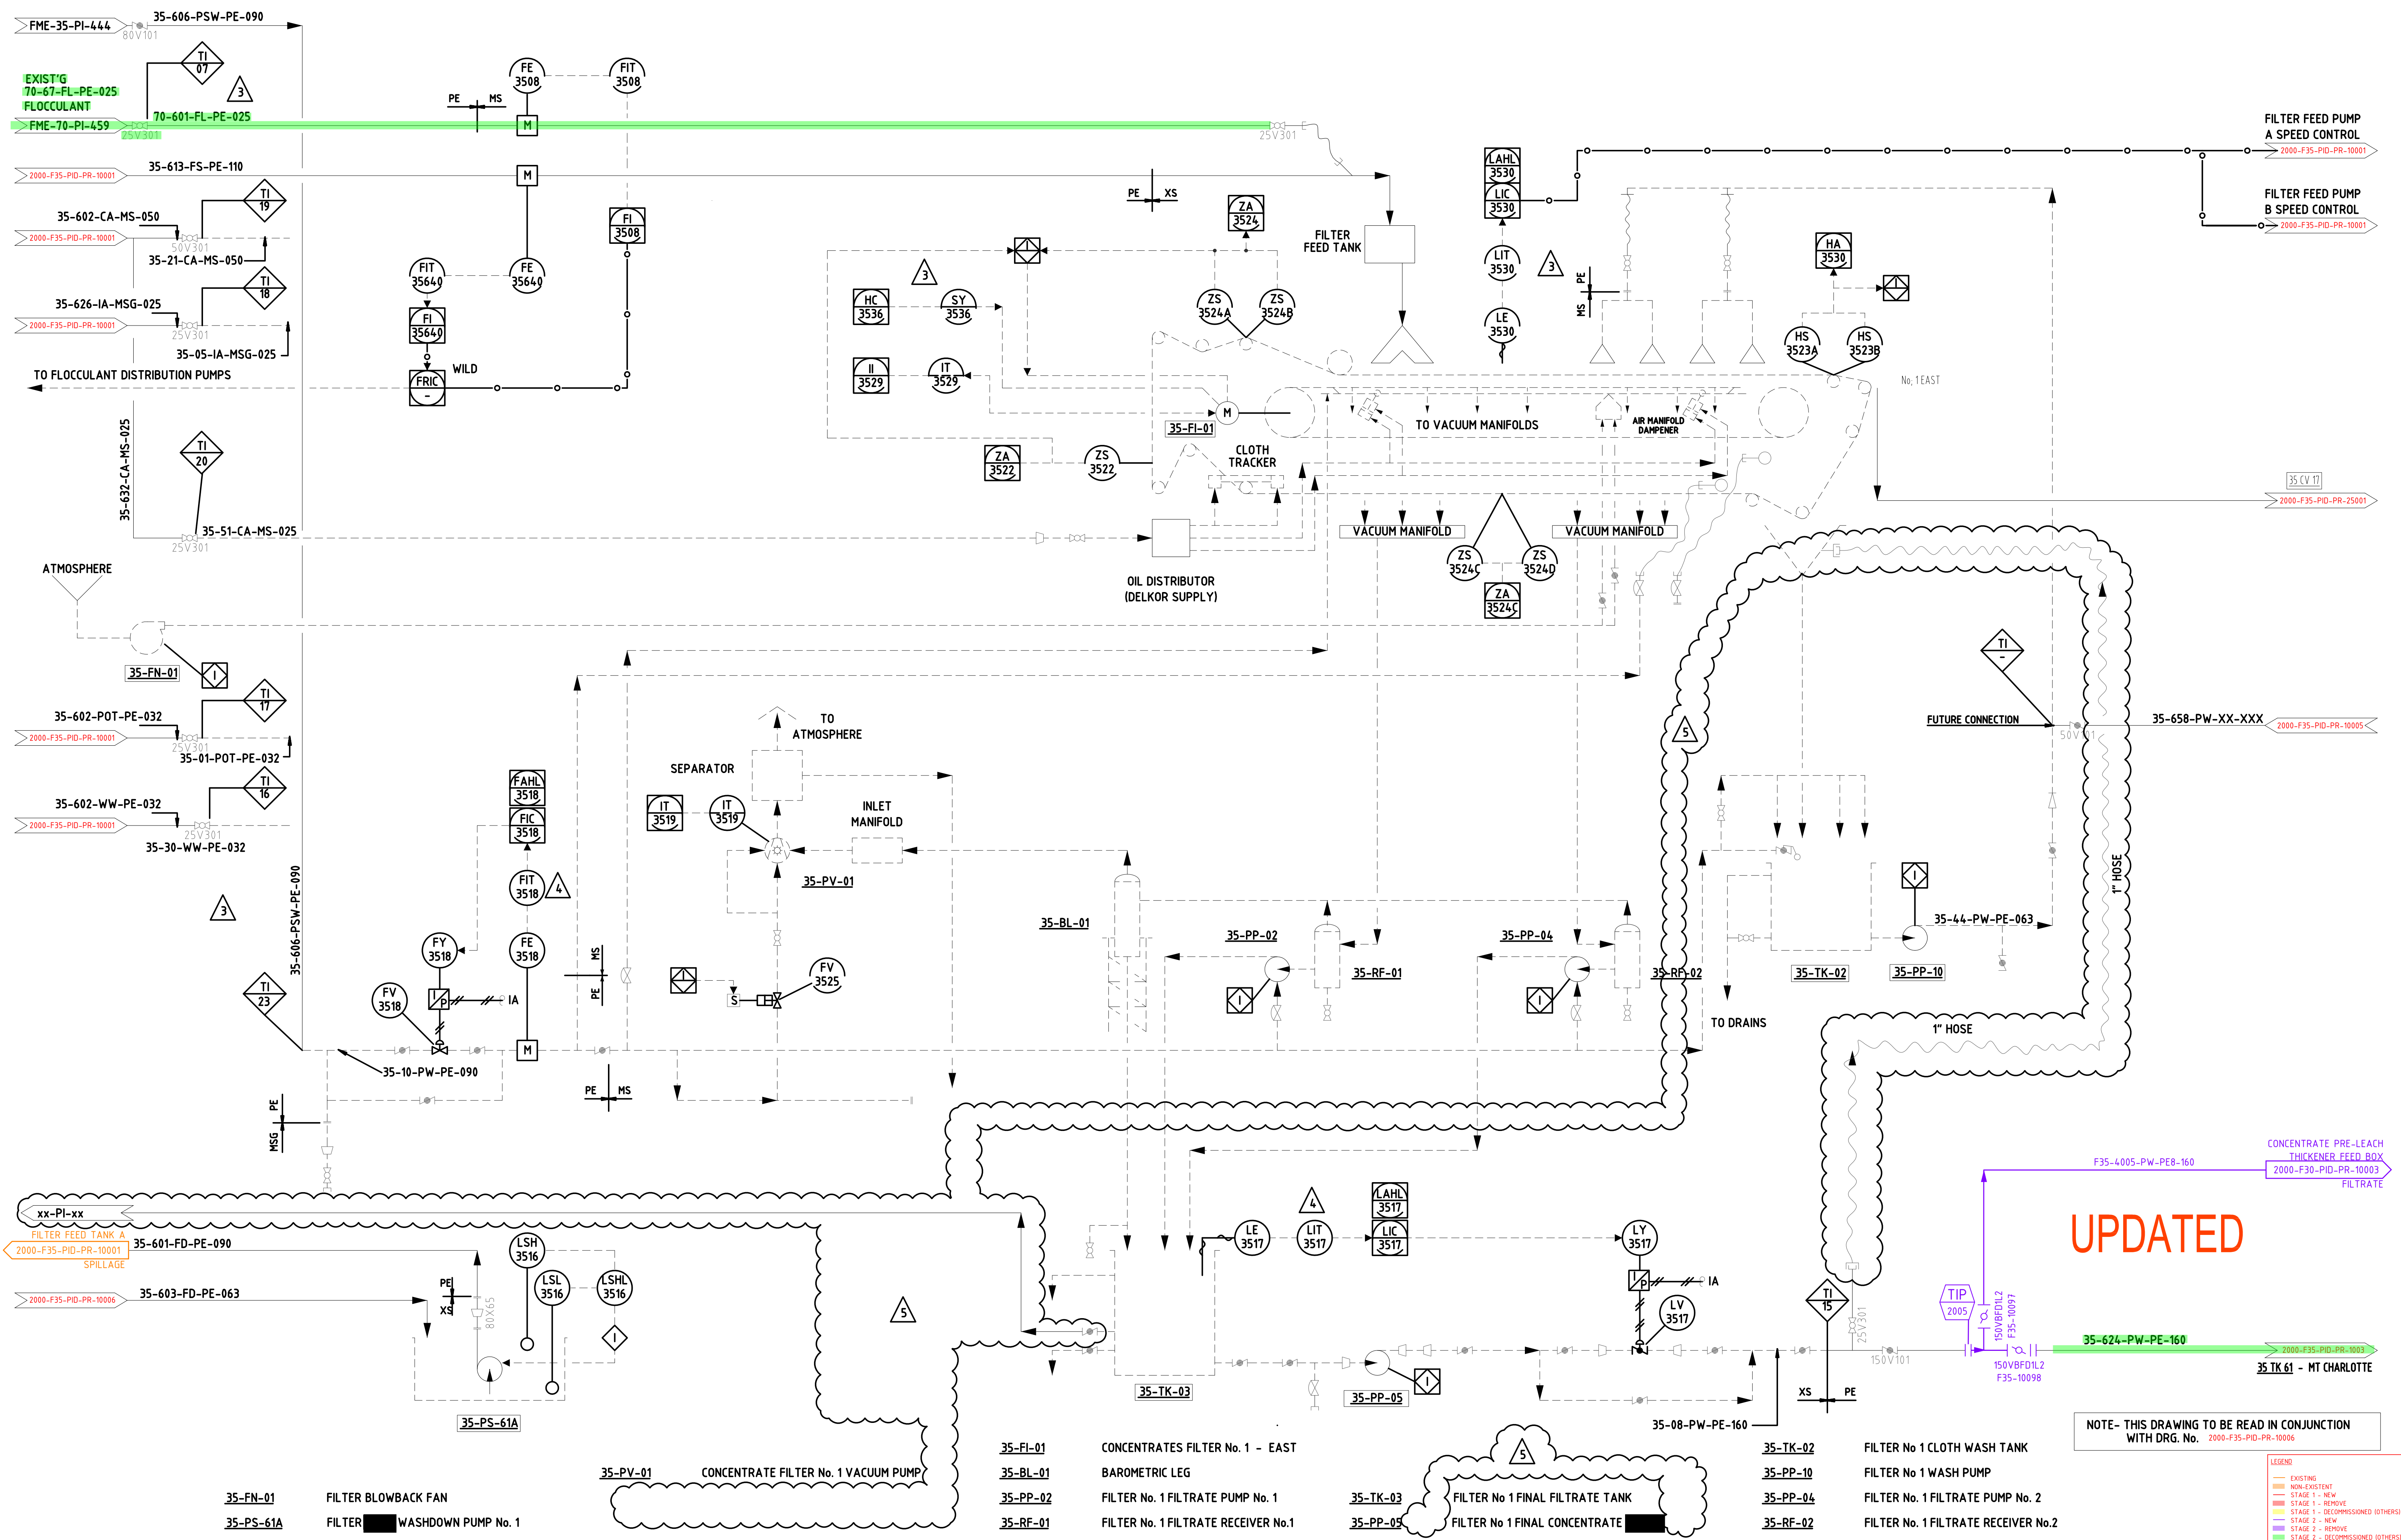

UPDATED

**NOTE- THIS DRAWING TO BE READ IN CONJUNCTION
WITH DRG. No. 2000-F35-PID-PR-10006**

LEGEND

- EXISTING
- NON-EXISTENT
- STAGE 1 - NEW
- STAGE 1 - REMOVE
- STAGE 1 - DECOMMISSIONED (OTHERS)
- STAGE 2 - NEW
- STAGE 2 - REMOVE
- STAGE 2 - DECOMMISSIONED (OTHERS)