


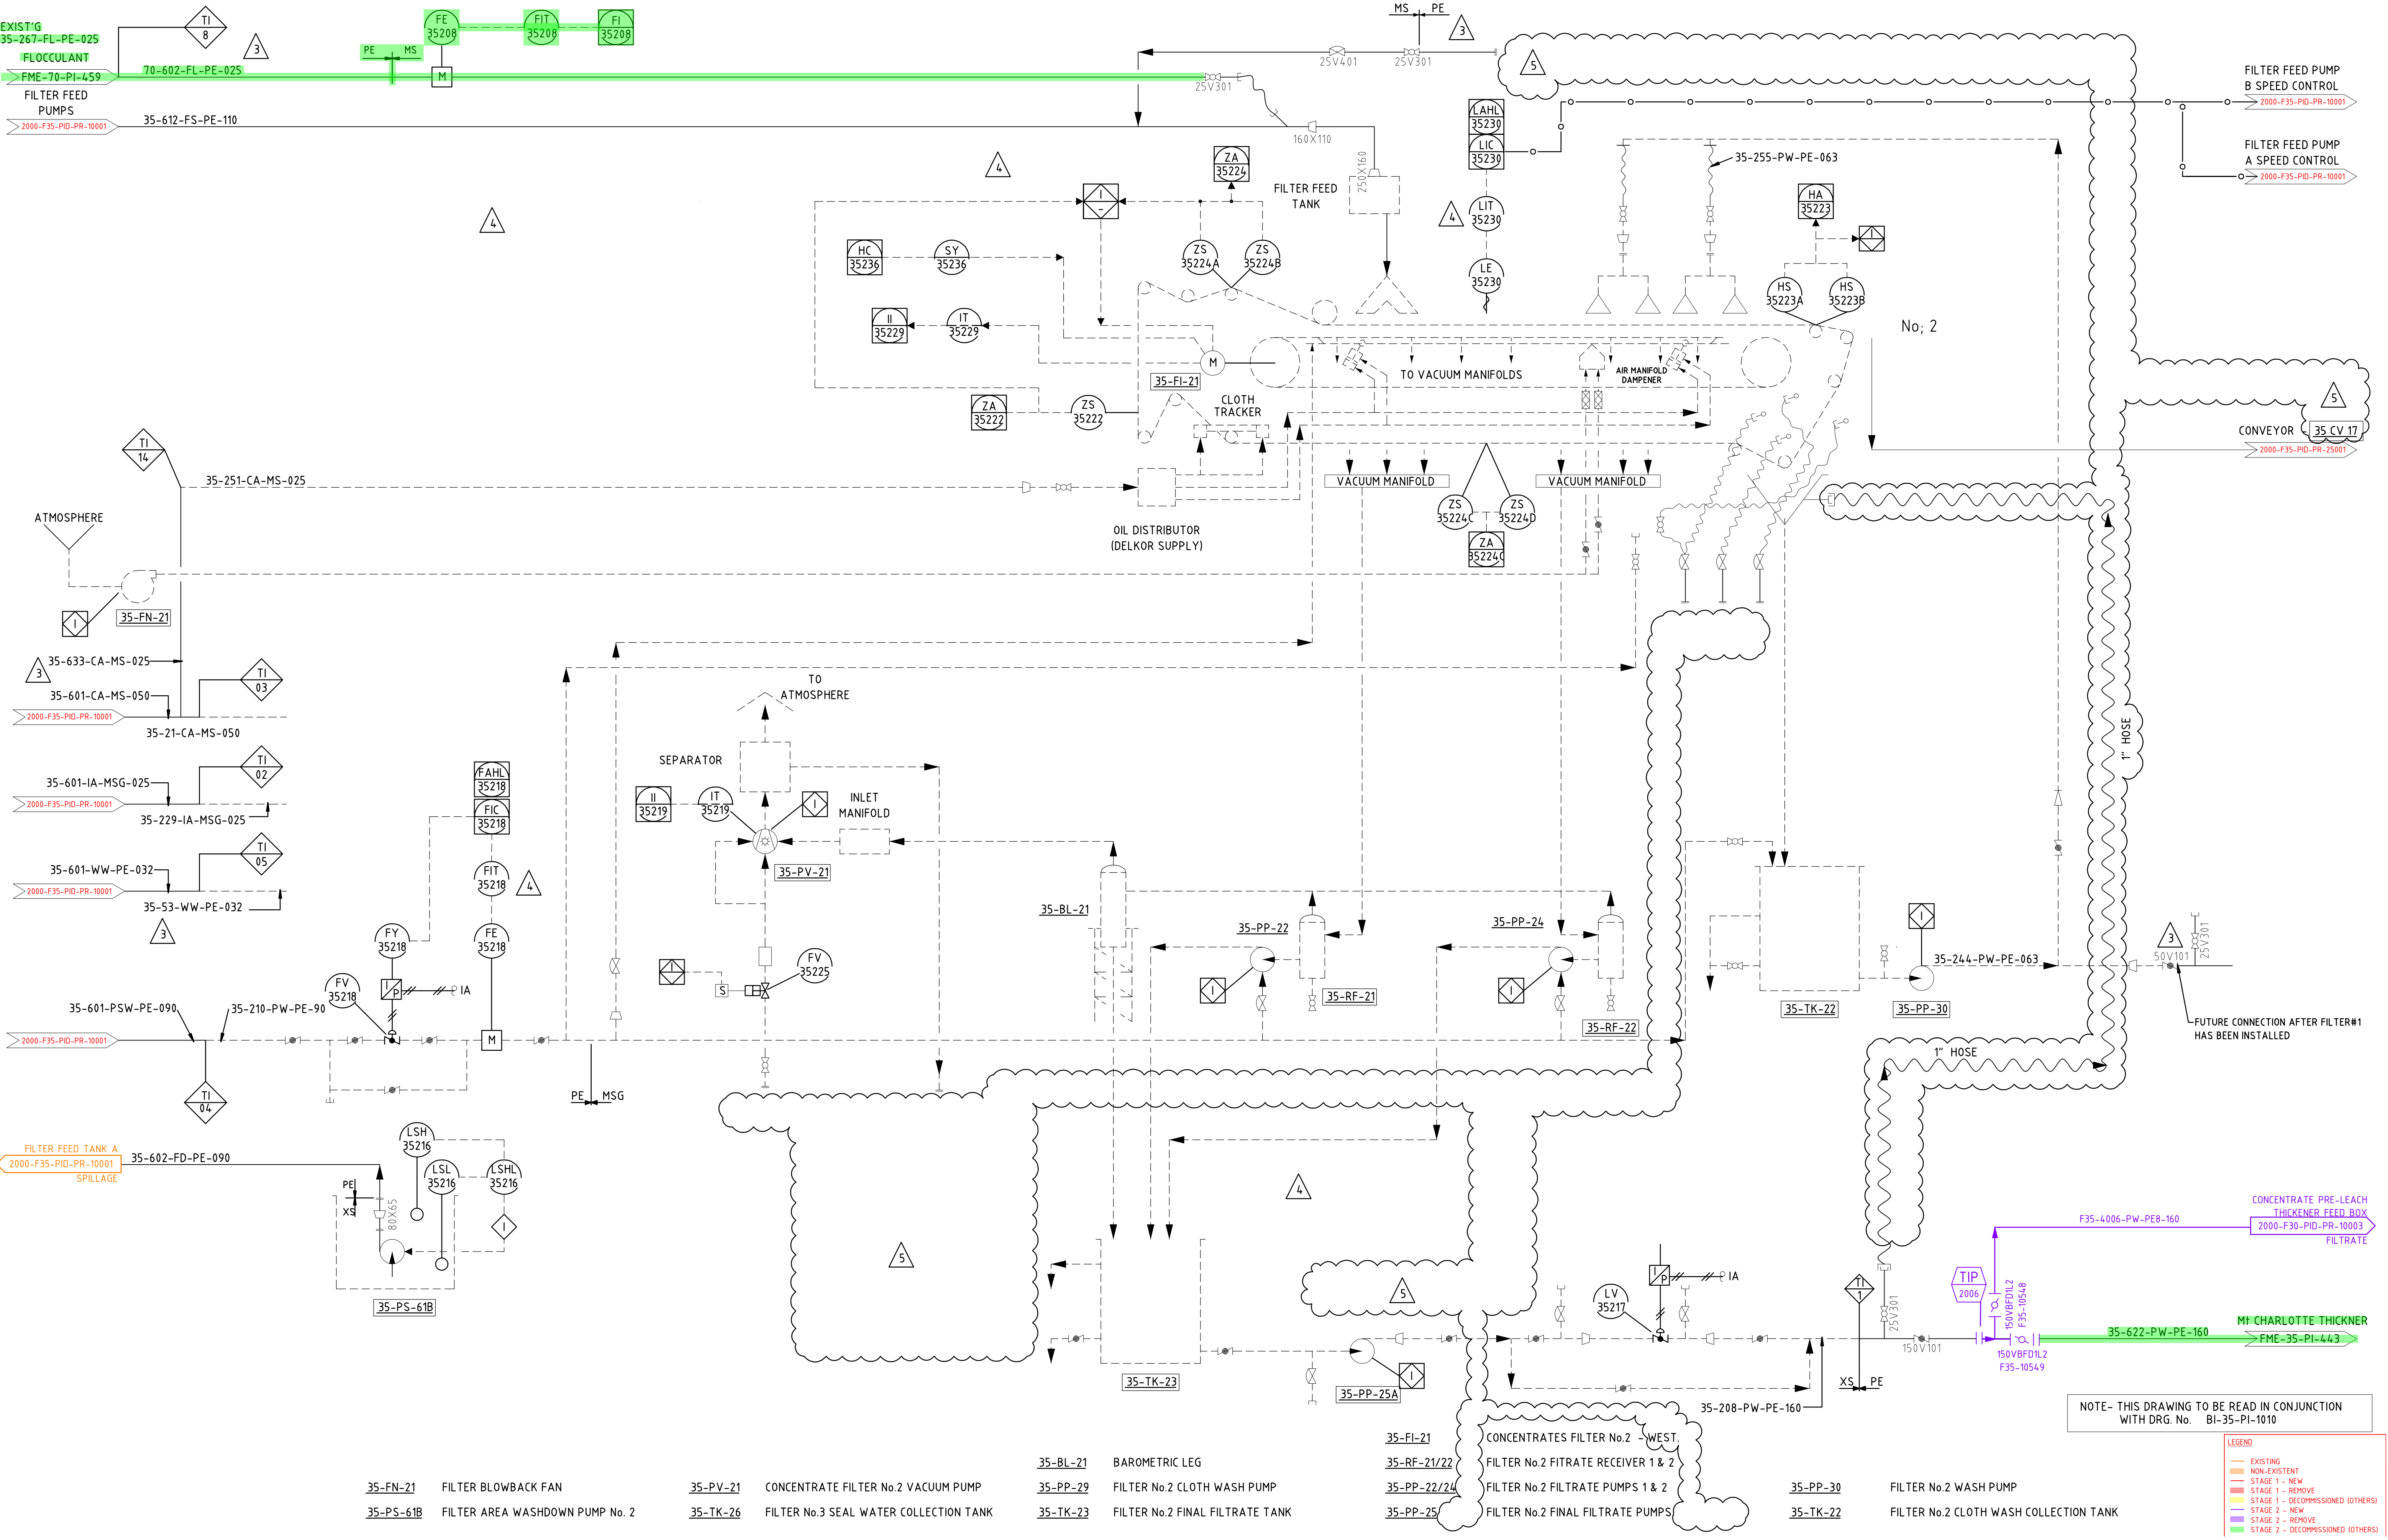

35-FN-21 FILTER BLOWBACK FAN
35-PS-61B FILTER AREA WASHDOWN PUMP No. 2

35-PV-21 CONCENTRATE FILTER No.2 VACUUM PUMP
35-TK-26 FILTER No.3 SEAL WATER COLLECTION TANK

35-BL-21 BAROMETRIC LEG
35-PP-29 FILTER No.2 CLOTH WASH PUMP
35-TK-23 FILTER No.2 FINAL FILTRATE TANK

35-FI-21 CONCENTRATES FILTER No.2 - WEST
35-RF-21/22 FILTER No.2 FITRATE RECEIVER 1 & 2
35-PP-22/24 FILTER No.2 FILTRATE PUMPS 1 & 2
35-PP-25 FILTER No.2 FINAL FILTRATE PUMPS

35-PP-30 FILTER No.2 WASH PUMP
35-TK-22 FILTER No.2 CLOTH WASH COLLECTION TANK

LEGEND
EXISTING
NON-EXISTENT
STAGE 1 - NEW
STAGE 1 - REMOVE
STAGE 1 - DECOMMISSIONED (OTHERS)
STAGE 2 - NEW
STAGE 2 - REMOVE
STAGE 2 - DECOMMISSIONED (OTHERS)