


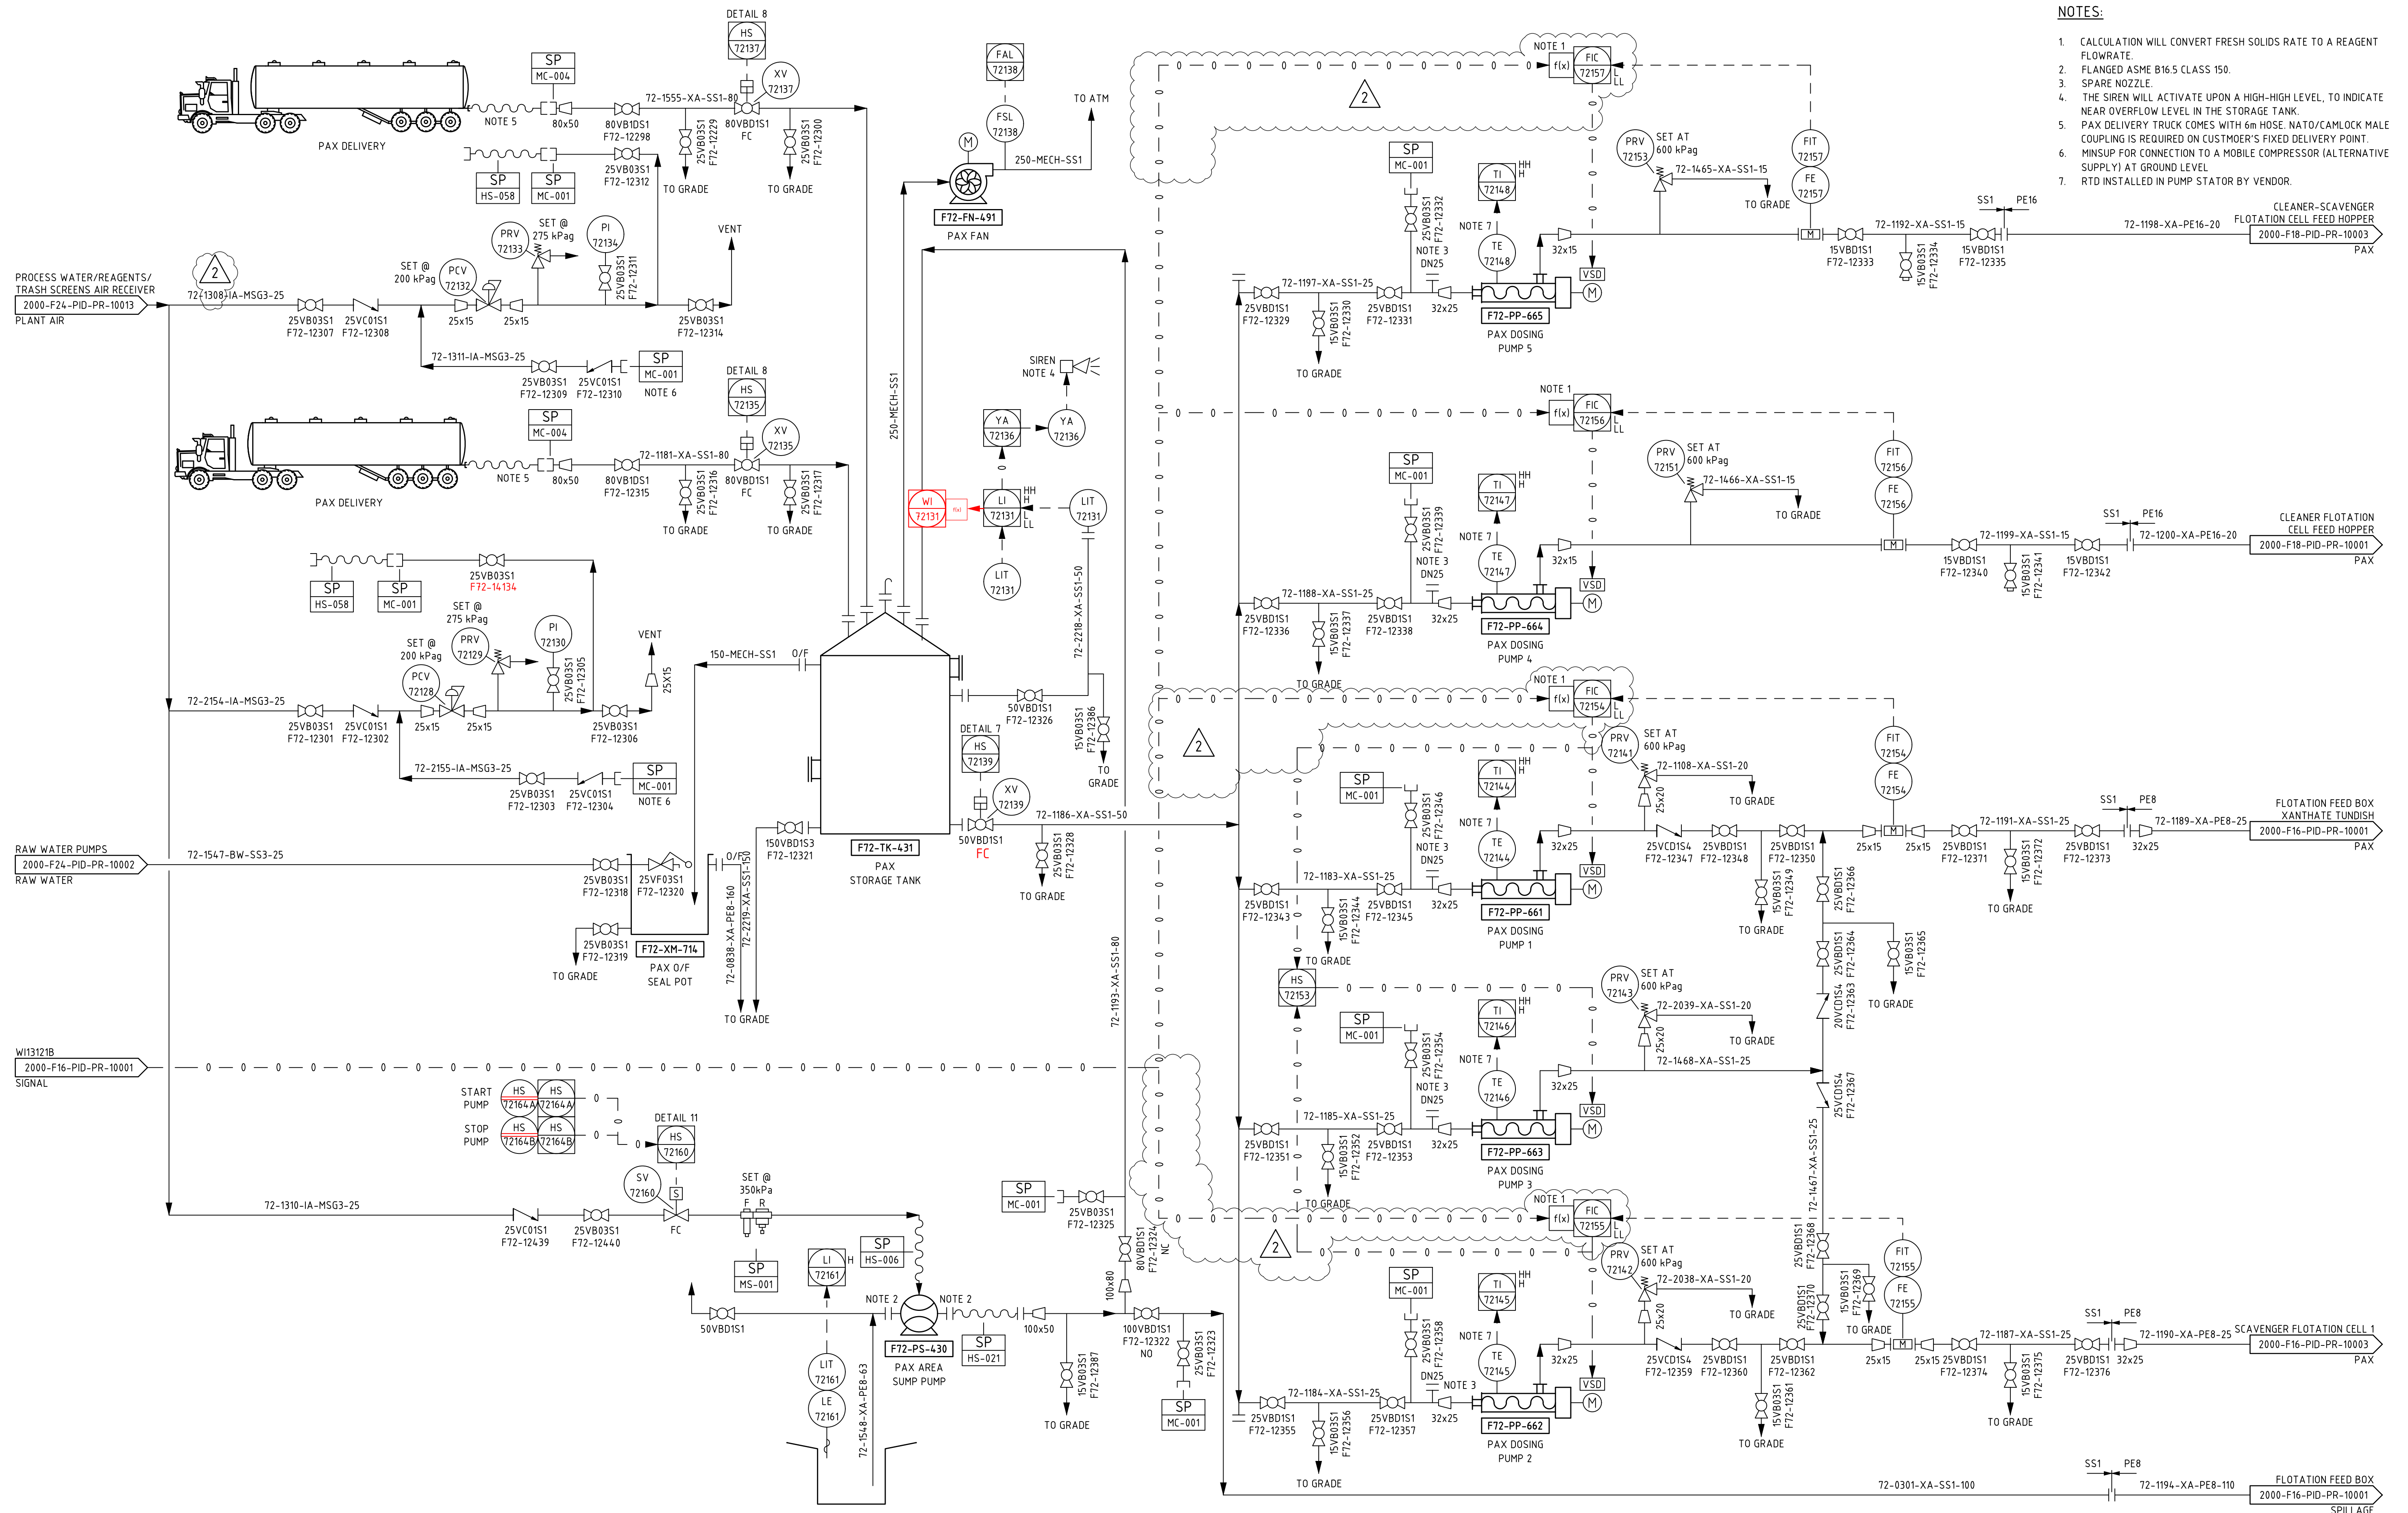

NOTES:

1. CALCULATION WILL CONVERT FRESH SOLIDS RATE TO A REAGENT FLOWRATE.
2. FLANGED ASME B16.5 CLASS 150.
3. SPARE NOZZLE.
4. THE SIREN WILL ACTIVATE UPON A HIGH-HIGH LEVEL, TO INDICATE NEAR OVERFLOW LEVEL IN THE STORAGE TANK.
5. PAX DELIVERY TRUCK COMES WITH 6m HOSE. NATO/CAMLOCK MALE COUPLING IS REQUIRED ON CUSTOMER'S FIXED DELIVERY POINT.
6. MINSUP FOR CONNECTION TO A MOBILE COMPRESSOR (ALTERNATIVE SUPPLY) AT GROUND LEVEL.
7. RTD INSTALLED IN PUMP STATOR BY VENDOR.