


WI30411

2000-F30-PID-PR-10004
SIGNAL

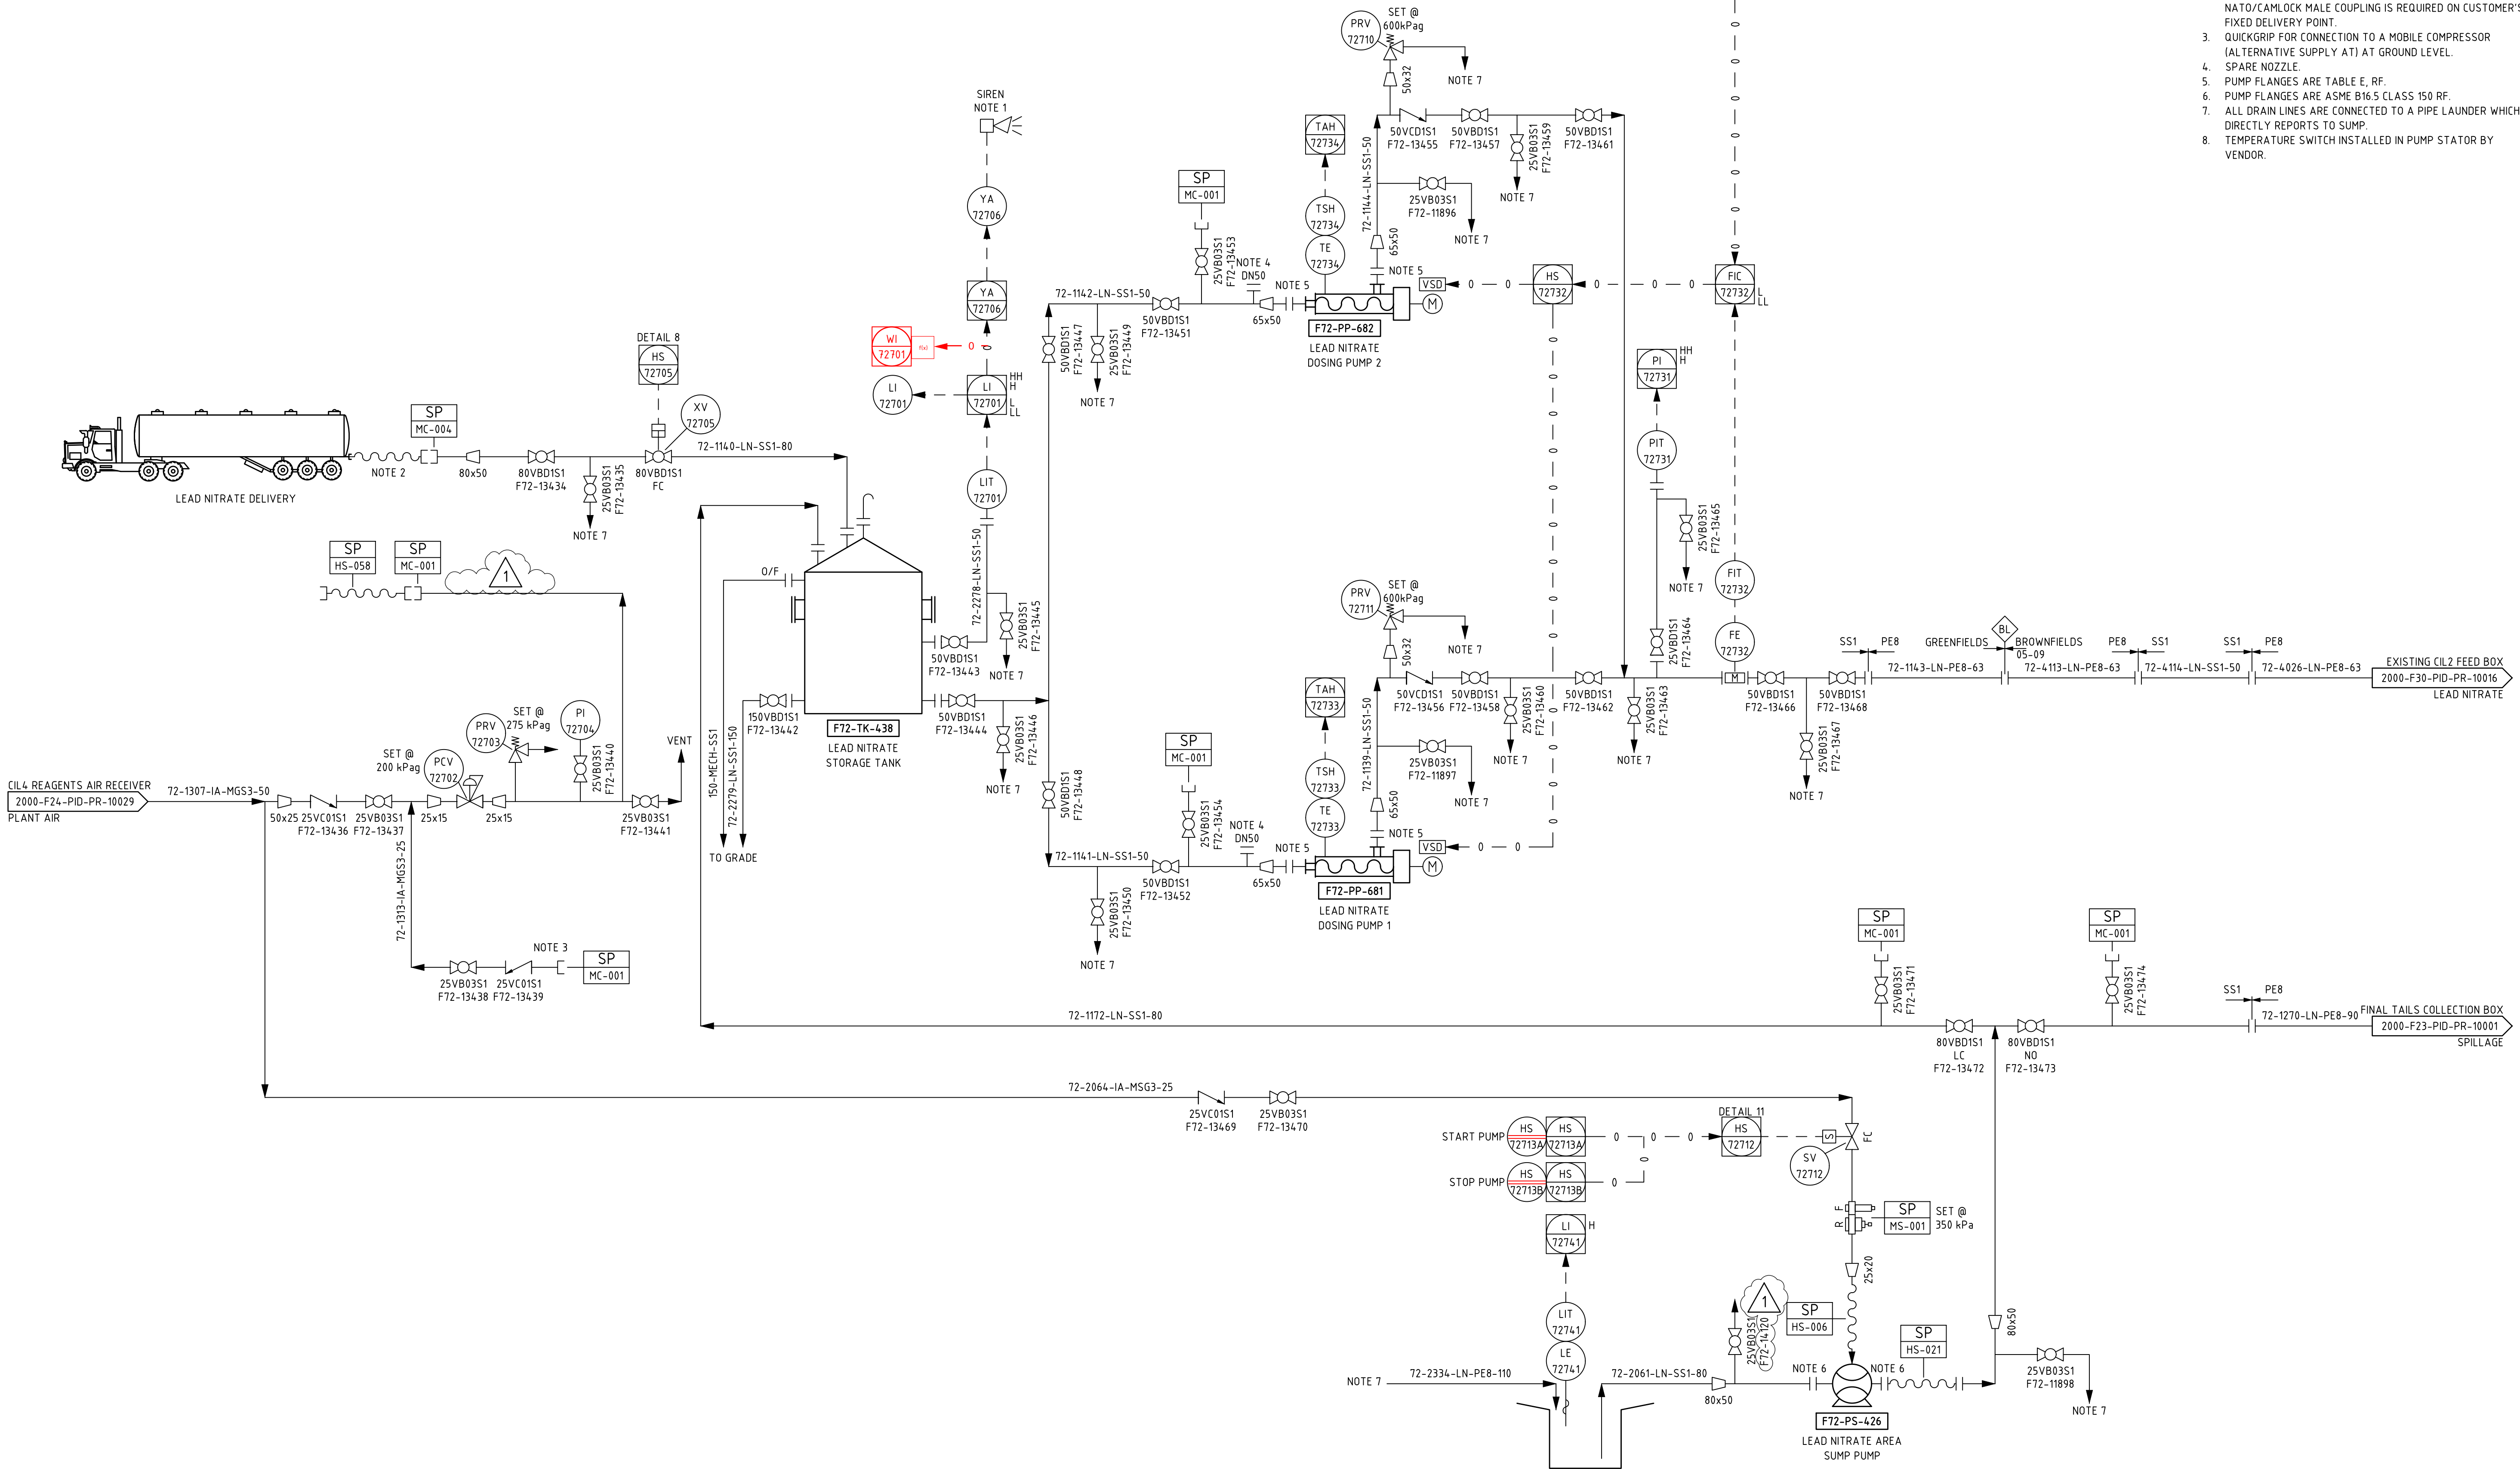

NOTES:

1. THE SIREN & BEACON WILL ACTIVATE UPON A HIGH-HIGH LEVEL, TO INDICATE NEAR OVERFLOW LEVEL IN THE STORAGE TANK.
2. LEAD NITRATE DELIVERY TRUCK COMES WITH 6m HOSE. NATO/CAMLOCK MALE COUPLING IS REQUIRED ON CUSTOMER'S FIXED DELIVERY POINT.
3. QUICKGRIP FOR CONNECTION TO A MOBILE COMPRESSOR (ALTERNATIVE SUPPLY AT) AT GROUND LEVEL.
4. SPARE NOZZLE.
5. PUMP FLANGES ARE TABLE E, RF.
6. PUMP FLANGES ARE ASME B16.5 CLASS 150 RF.
7. ALL DRAIN LINES ARE CONNECTED TO A PIPE LAUNDER WHICH DIRECTLY REPORTS TO SUMP.
8. TEMPERATURE SWITCH INSTALLED IN PUMP STATOR BY VENDOR.