


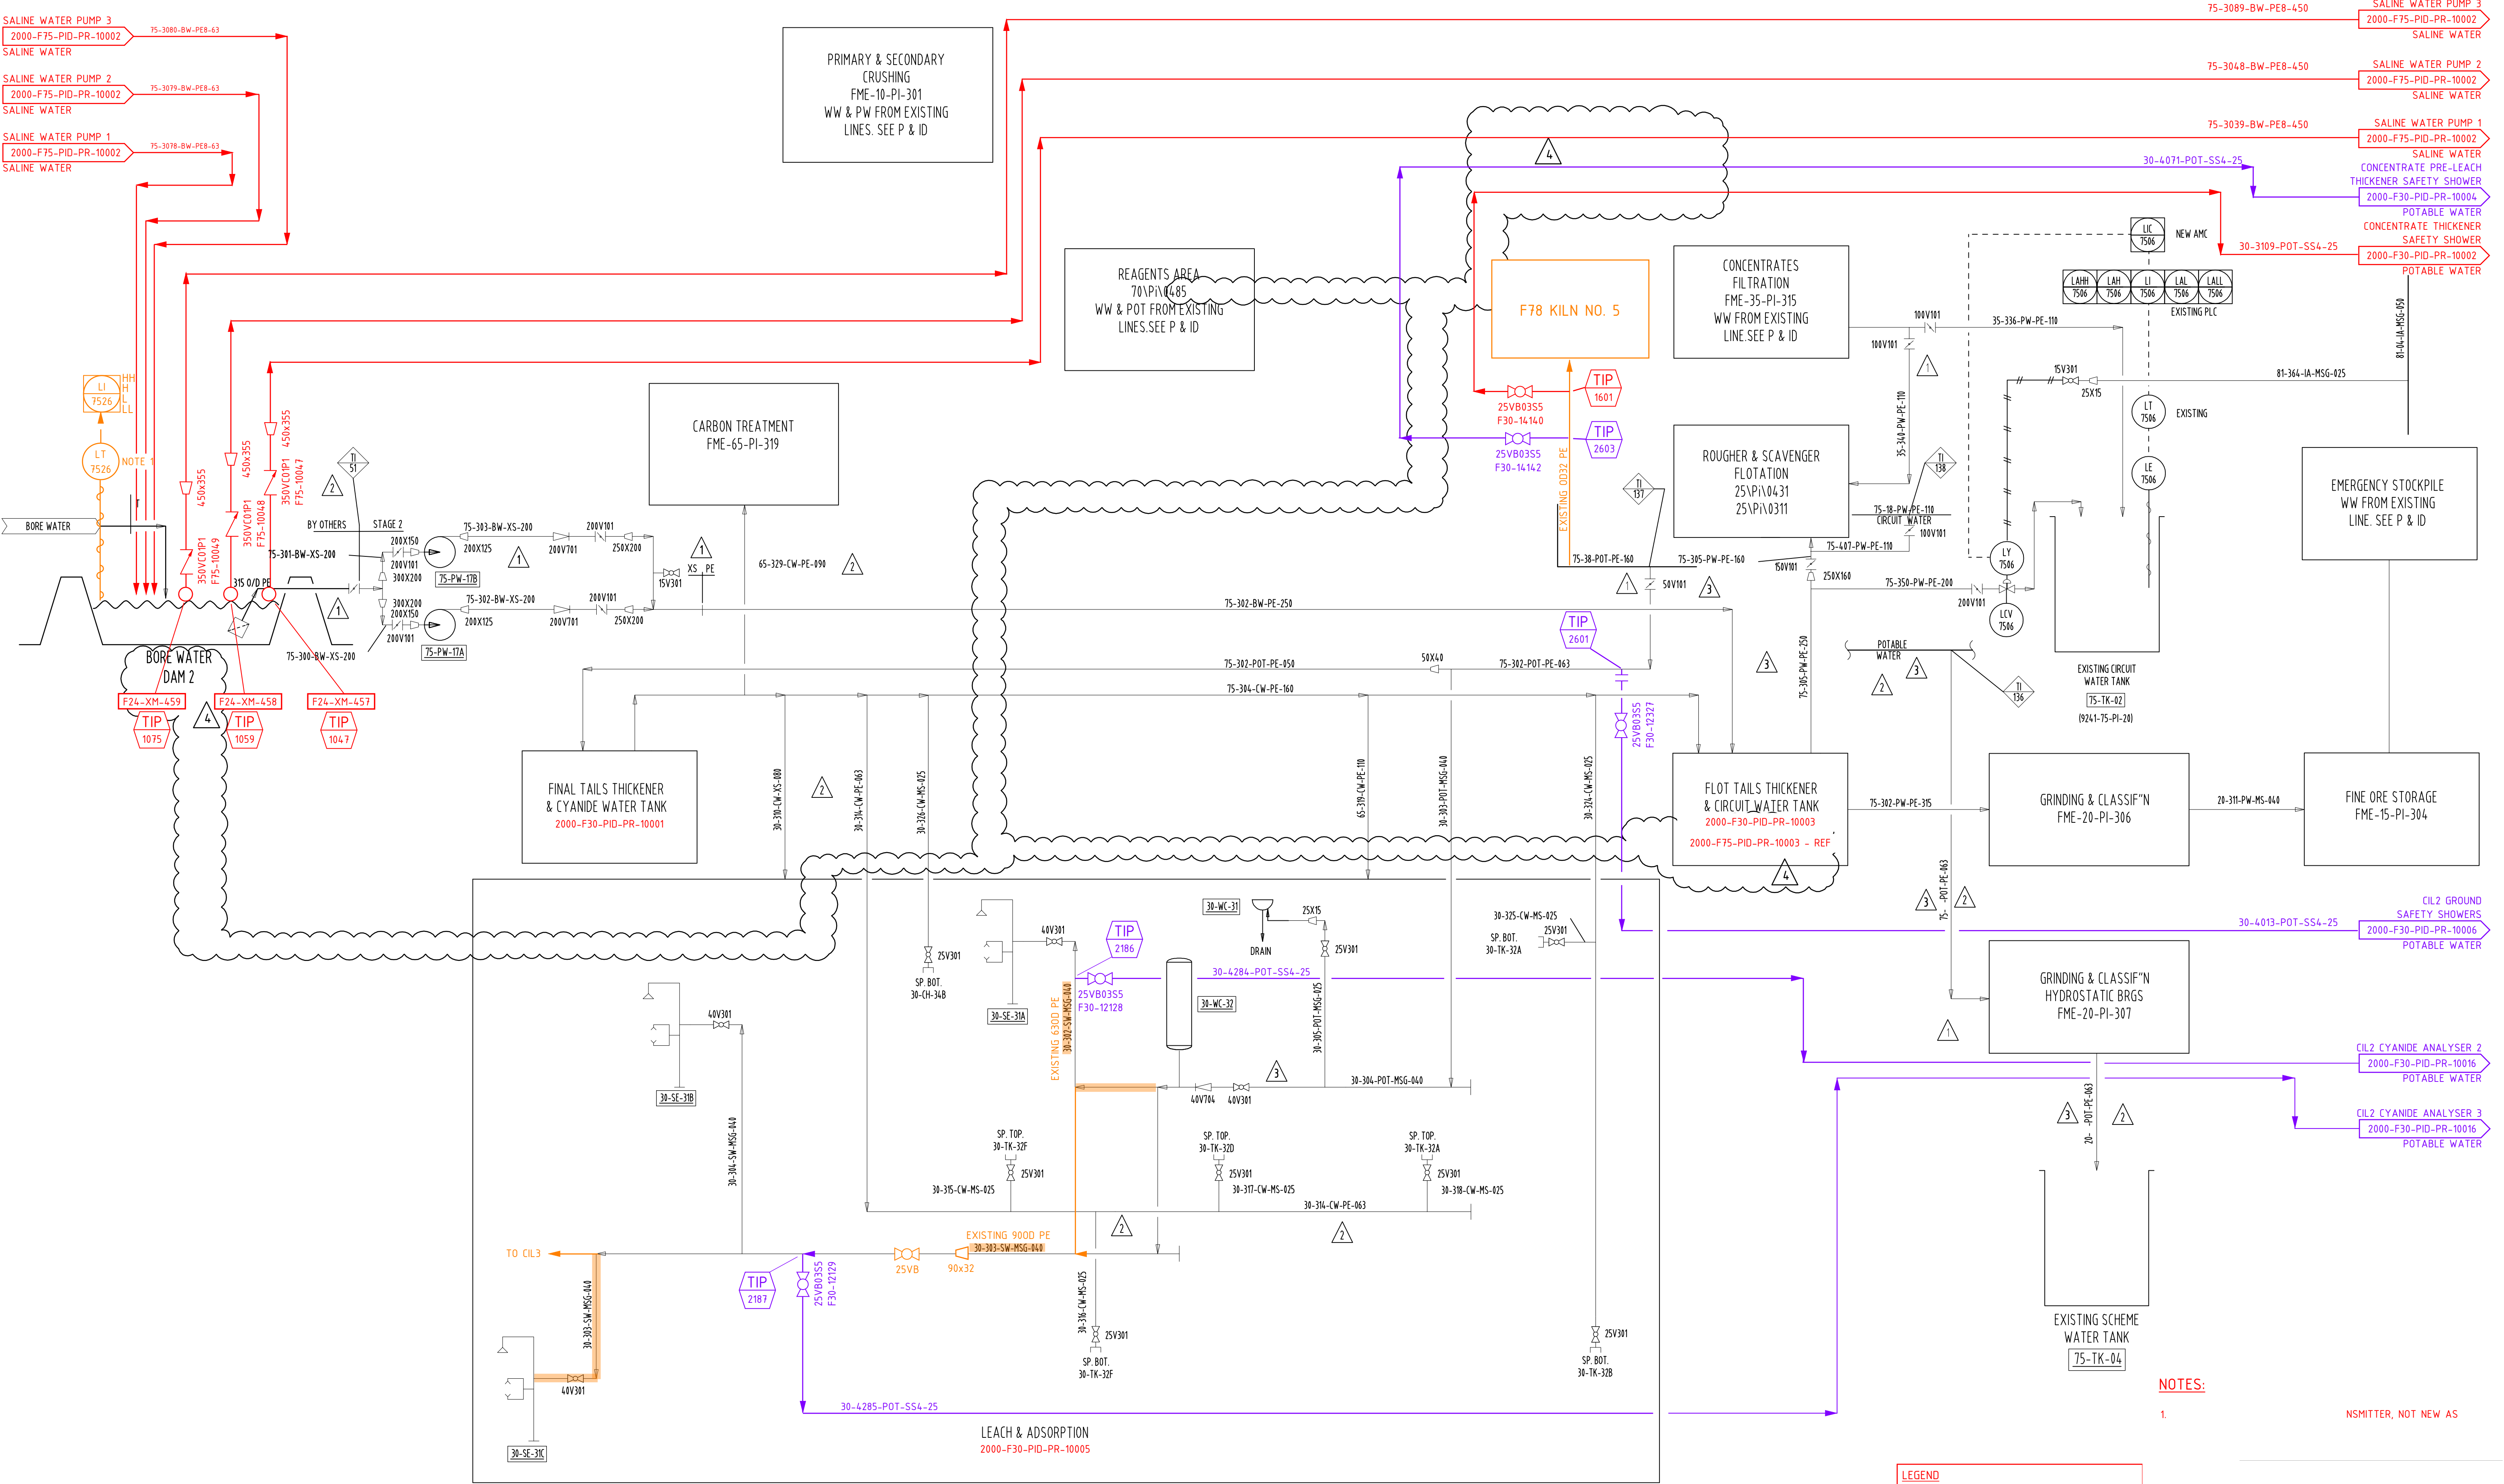

30-SE-31A/C SHOWER/EYEWASH - C.I.L. TANKS
30-WC-31 DRINKING FOUNTAIN
30-WC-32 SHOWER/ACCUMULATOR - C.I.L. TANKS

75-PW-17A/B BORE WATER/DAM PUMP

F24-XM-457 SALINE WATER PUMP 1 SUCTION TURRET
F24-XM-458 SALINE WATER PUMP 2 SUCTION TURRET
F24-XM-459 SALINE WATER PUMP 3 SUCTION TURRET