


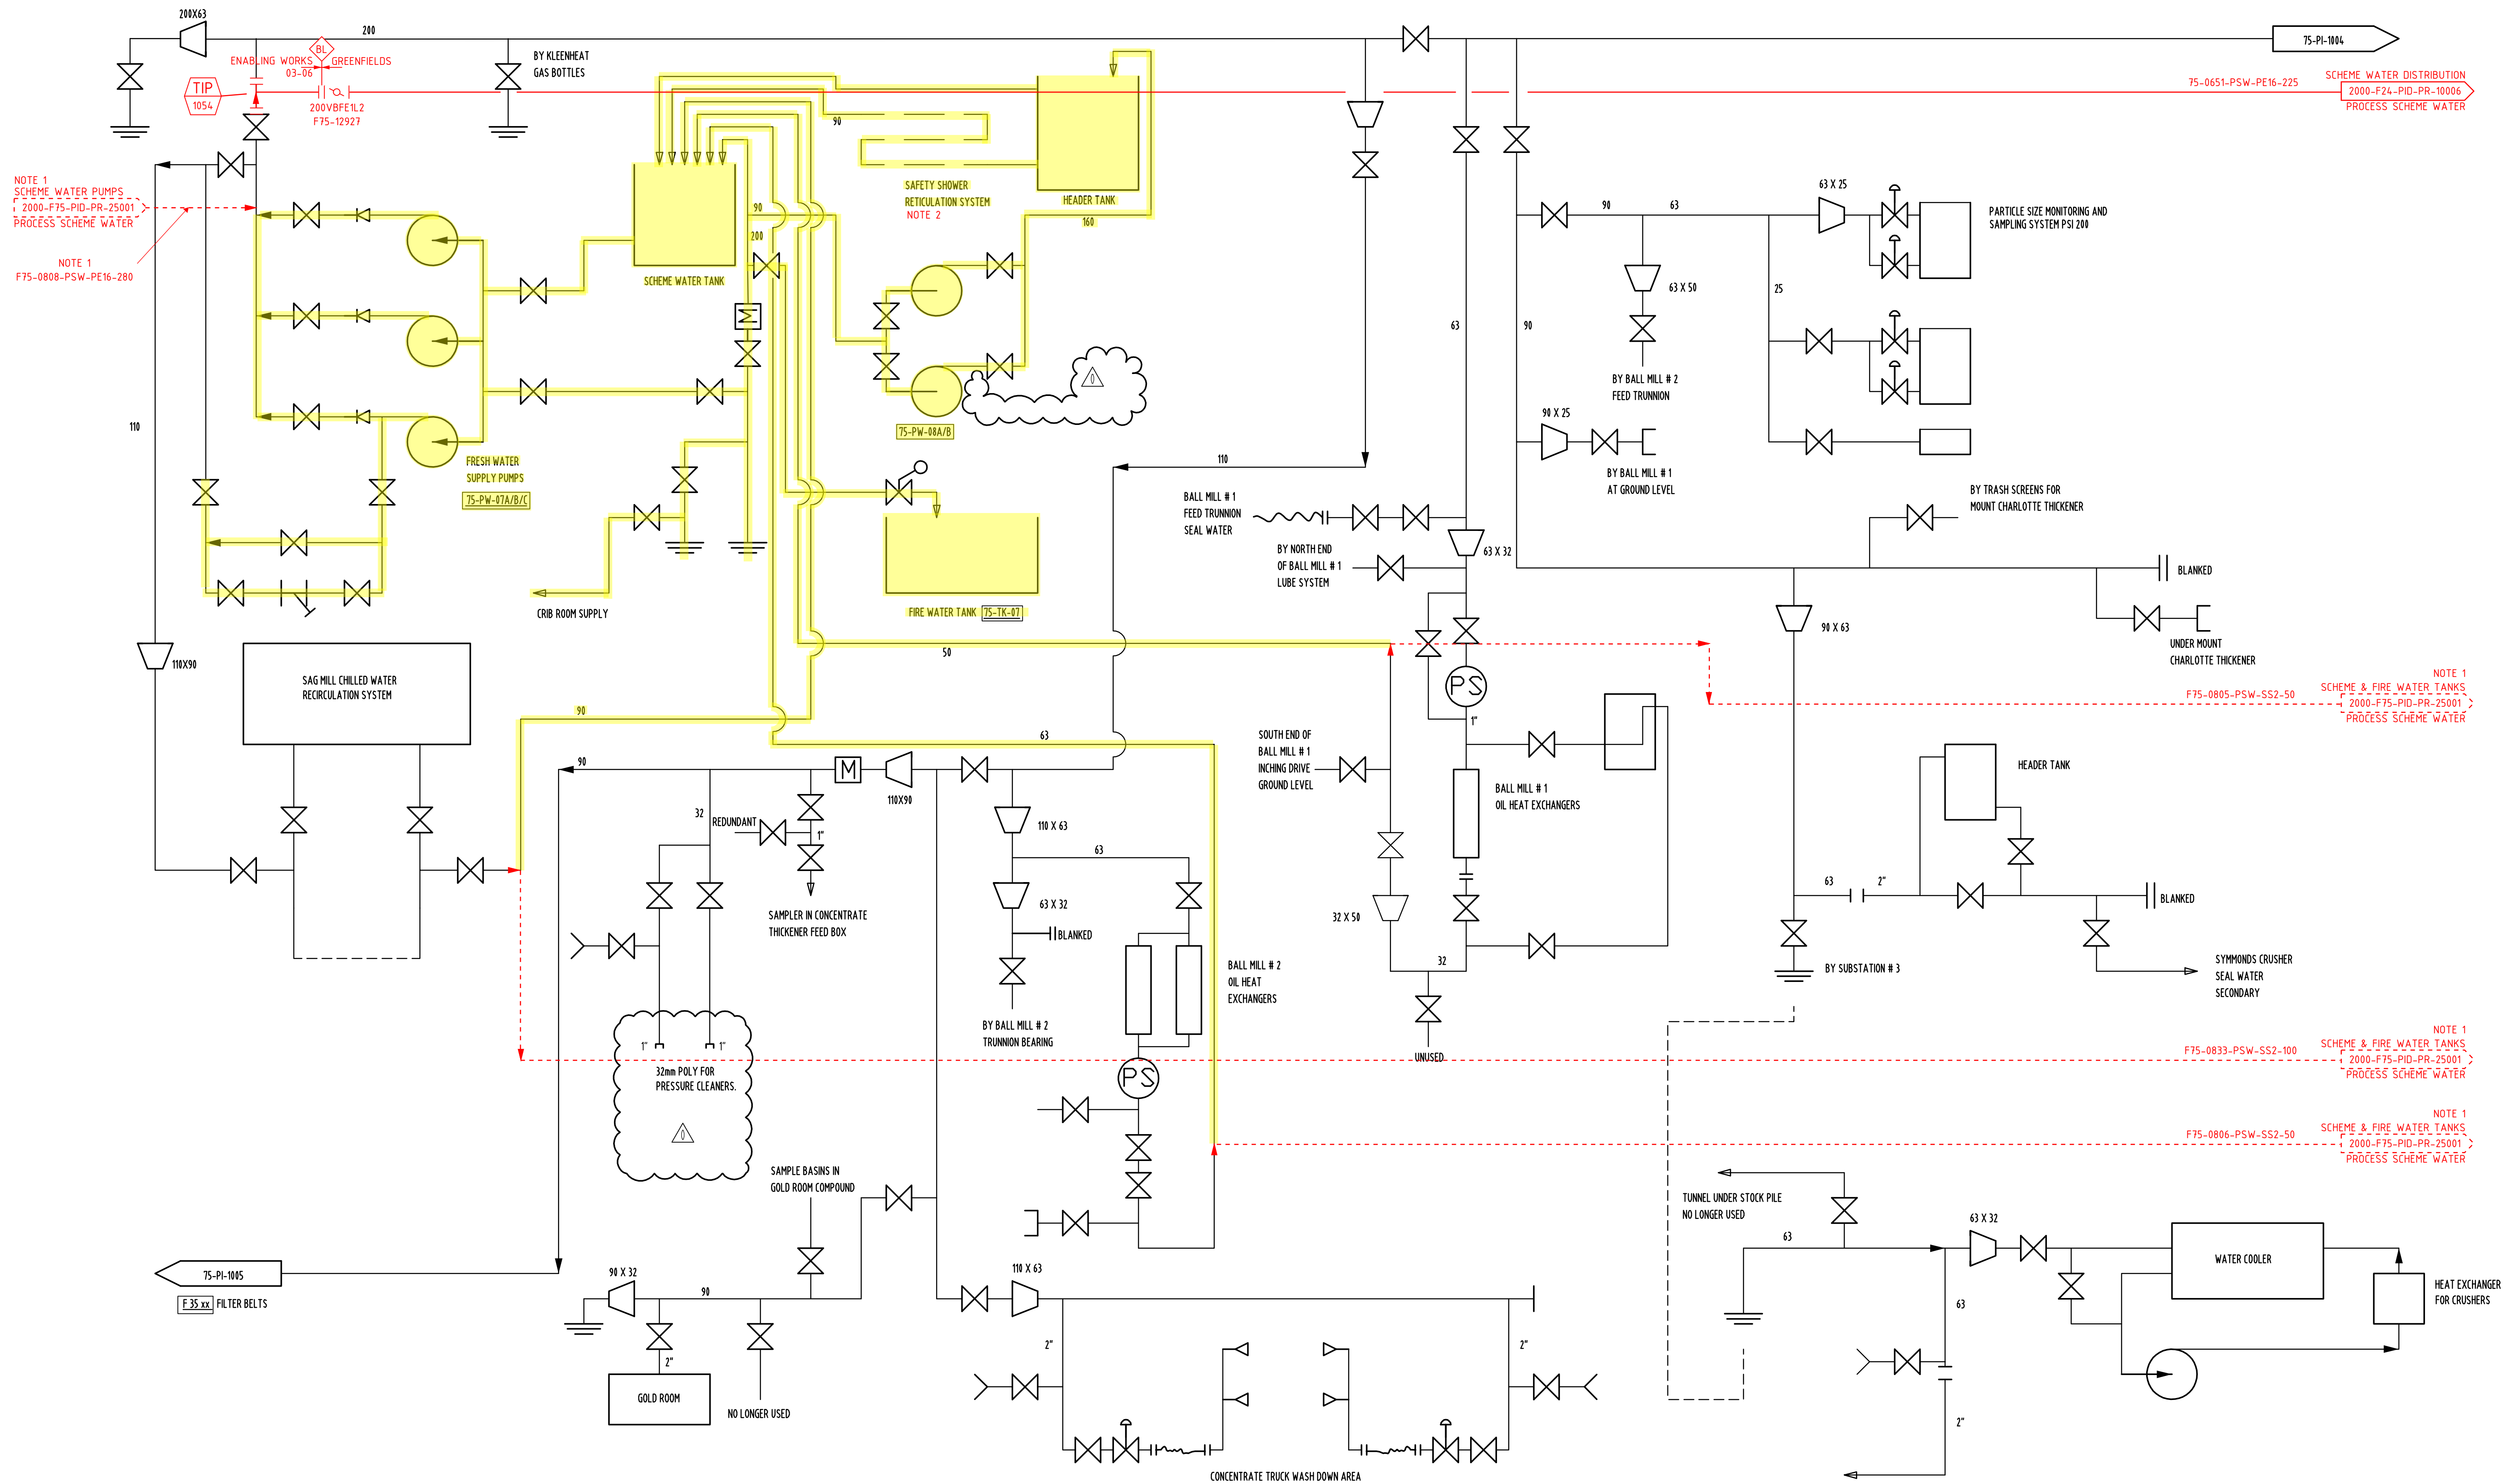

NOTES:

1. ADDED PER REFER TO
2. SAFETY SHOWER RETICULATION NOT SHOWN ON ANY DRAWING. ENABLING WORKS UPGRADE SHOWN ON 2000-F75-PID-PR-25002.

LEGEND

- STAGE 1 - NEW
- STAGE 1 - REMOVE
- STAGE 1 - DECOMMISSIONED (OTHERS)
- STAGE 2 - NEW
- STAGE 2 - REMOVE
- STAGE 2 - DECOMMISSIONED (OTHERS)