


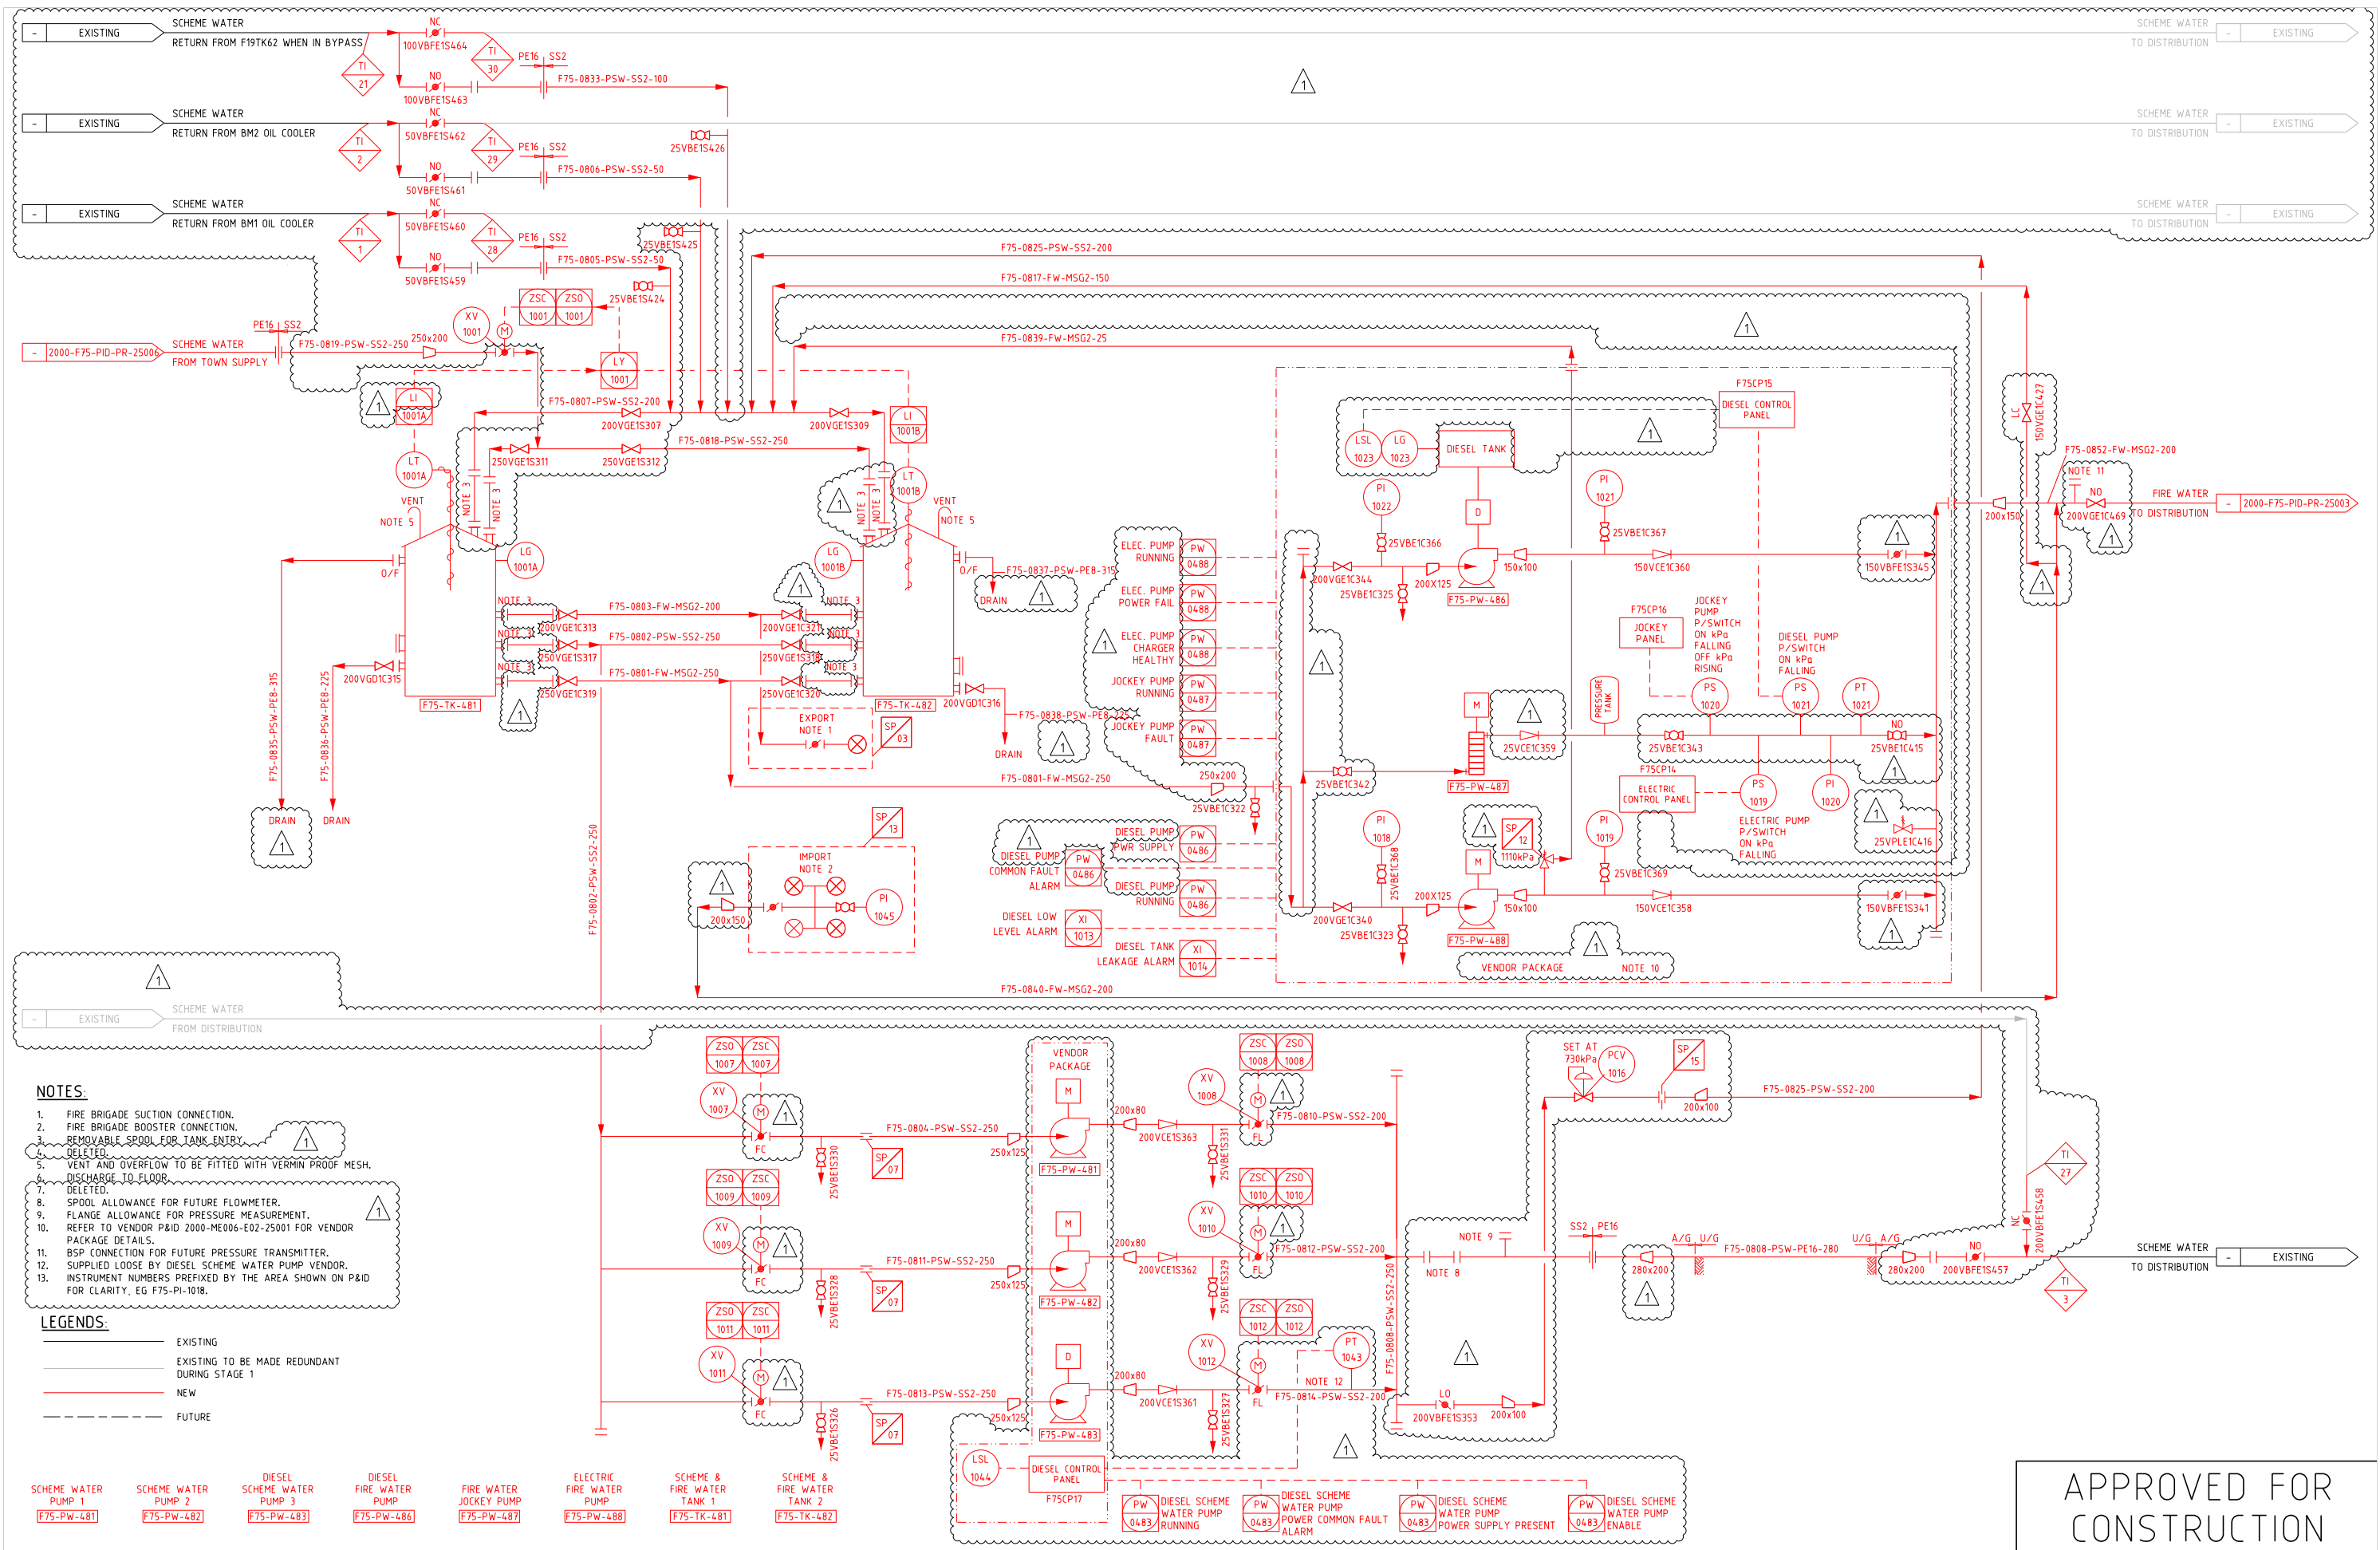

- NOTES:**
1. FIRE BRIGADE SUCTION CONNECTION.
 2. FIRE BRIGADE BOOSTER CONNECTION.
 3. REMOVABLE SPOOL FOR TANK ENTRY.
 4. DELETED.
 5. VENT AND OVERFLOW TO BE FITTED WITH VERMIN PROOF MESH.
 6. DISCHARGE TO FLOOR.
 7. DELETED.
 8. SPOOL ALLOWANCE FOR FUTURE FLOWMETER.
 9. FLANGE ALLOWANCE FOR PRESSURE MEASUREMENT.
 10. REFER TO VENDOR P&ID 2000-ME006-E02-25001 FOR VENDOR PACKAGE DETAILS.
 11. BSP CONNECTION FOR FUTURE PRESSURE TRANSMITTER.
 12. SUPPLIED LOOSE BY DIESEL SCHEME WATER PUMP VENDOR.
 13. INSTRUMENT NUMBERS PREFIXED BY THE AREA SHOWN ON P&ID FOR CLARITY. EG F75-PI-1018.

- LEGENDS:**
- EXISTING
 - EXISTING TO BE MADE REDUNDANT DURING STAGE 1
 - NEW
 - FUTURE

- SCHEME WATER PUMP 1 (F75-PW-481) SCHEME WATER PUMP 2 (F75-PW-482) DIESEL SCHEME WATER PUMP 3 (F75-PW-483) DIESEL FIRE WATER PUMP (F75-PW-486) FIRE WATER JOCKEY PUMP (F75-PW-487) ELECTRIC FIRE WATER PUMP (F75-PW-488) SCHEME & FIRE WATER TANK 1 (F75-TK-481) SCHEME & FIRE WATER TANK 2 (F75-TK-482) DIESEL CONTROL PANEL (F75CP17) DIESEL SCHEME WATER PUMP RUNNING (PW 0483) DIESEL SCHEME WATER PUMP POWER COMMON FAULT ALARM (PW 0483) DIESEL SCHEME WATER PUMP POWER SUPPLY PRESENT (PW 0483) DIESEL SCHEME WATER PUMP ENABLE (PW 0483)

APPROVED FOR CONSTRUCTION