


NOTES:
1. INSTRUMENT NUMBERS PREFIXED BY THE AREA SHOWN ON P&ID FOR CLARITY, EG F75-PI-1015.

LEGENDS:

- EXISTING
- EXISTING TO BE MADE REDUNDANT DURING STAGE 1
- NEW
- FUTURE

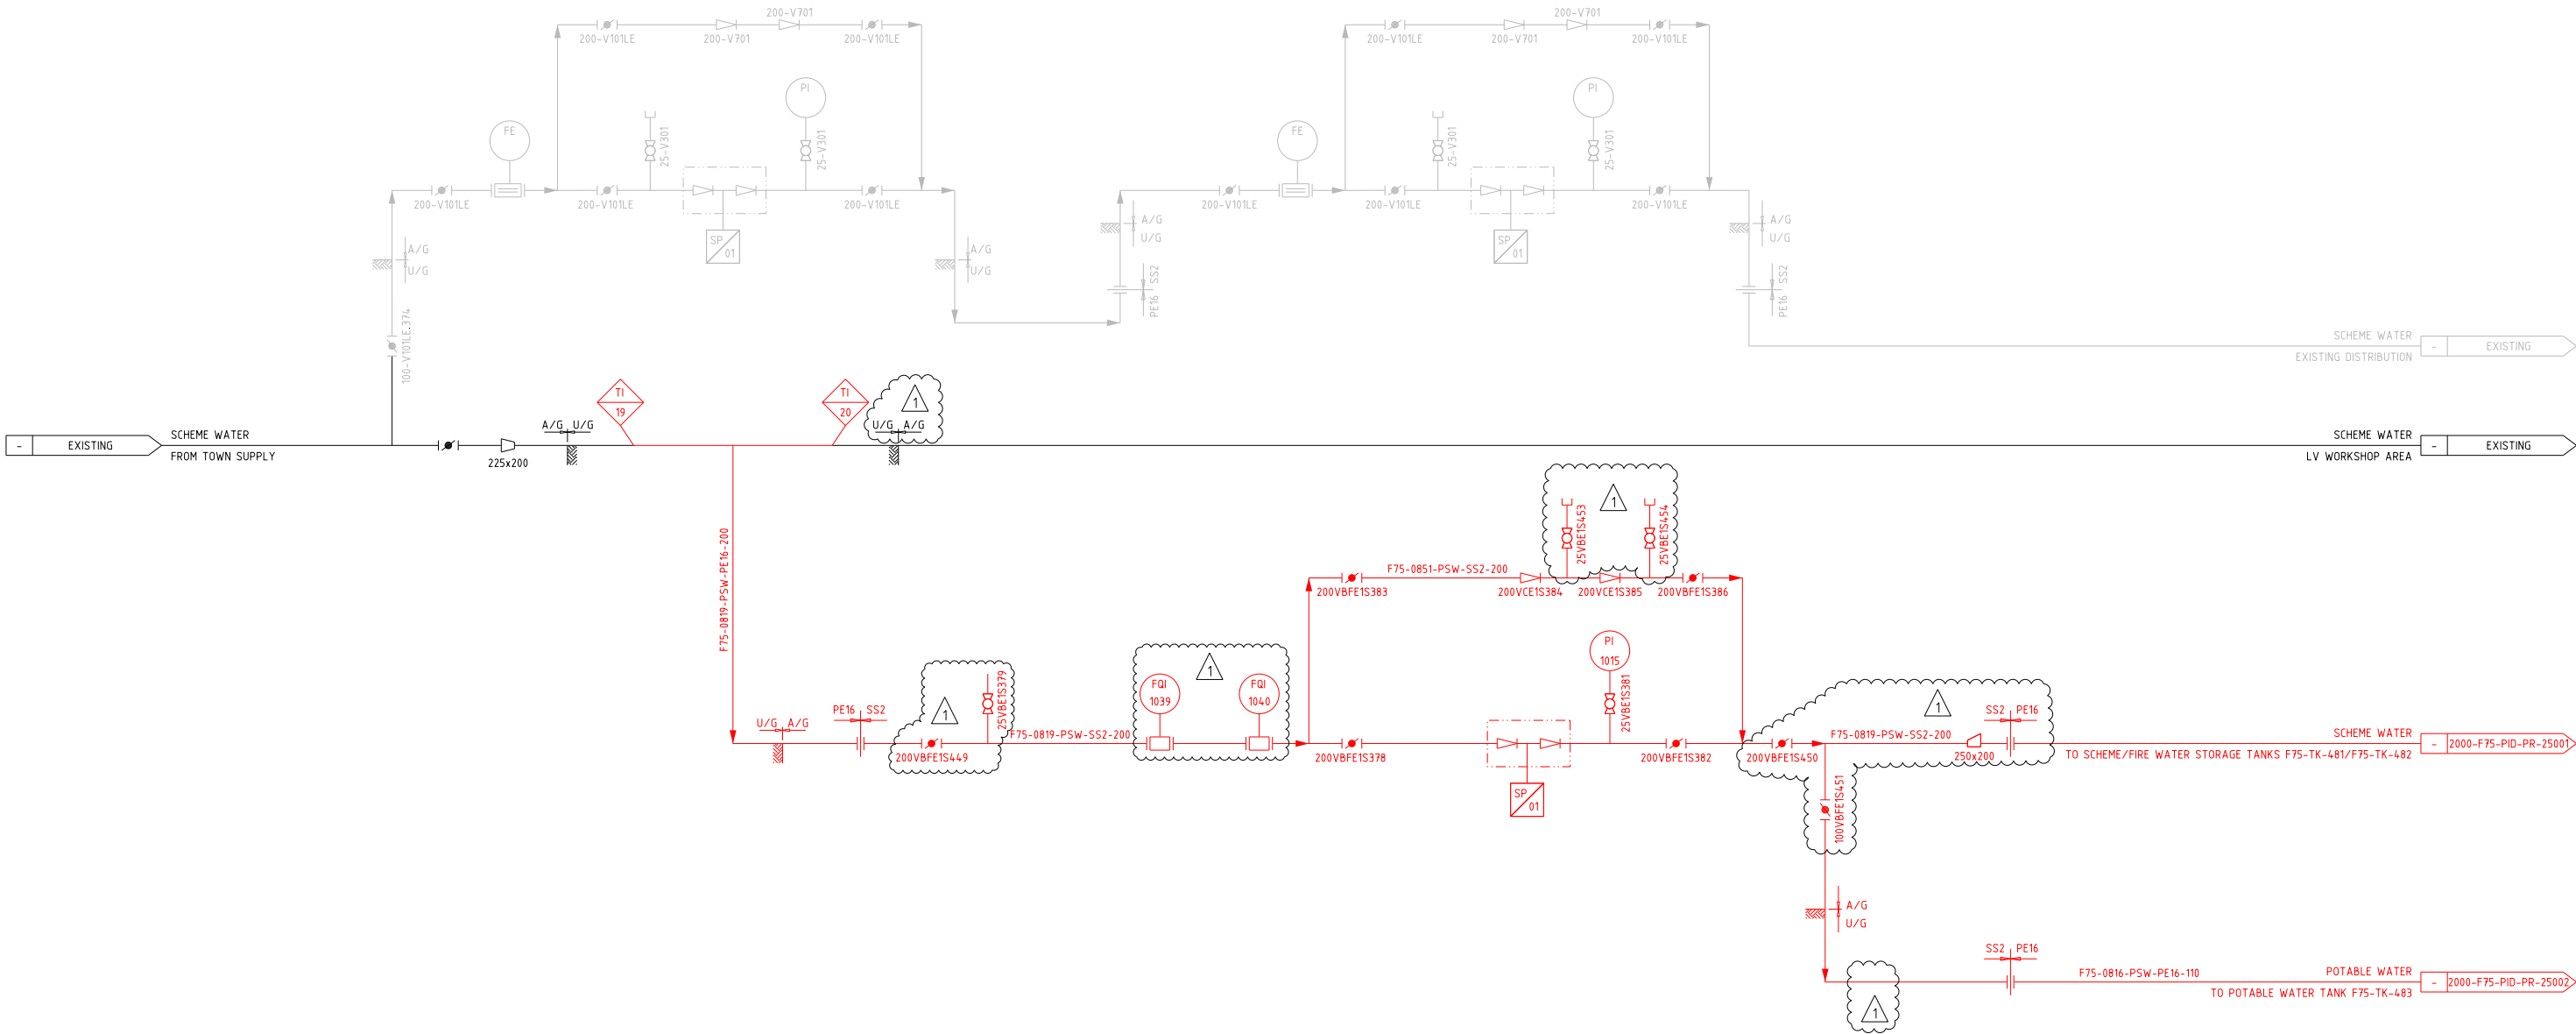

APPROVED FOR
CONSTRUCTION