


- LEGEND:
- EXISTING
 - NEW
 - FUTURE
 - DECOMMISSIONED

- NOTES:
- PIPE ON TOP OF TSF TO BE FLANGED EVERY 40m.
 - VALVE TO BE INSTALLED WITHOUT A HANDLE.

- HOLDS:
- ON HOLD PENDING CONFIRMATION OF VENDOR DATA.

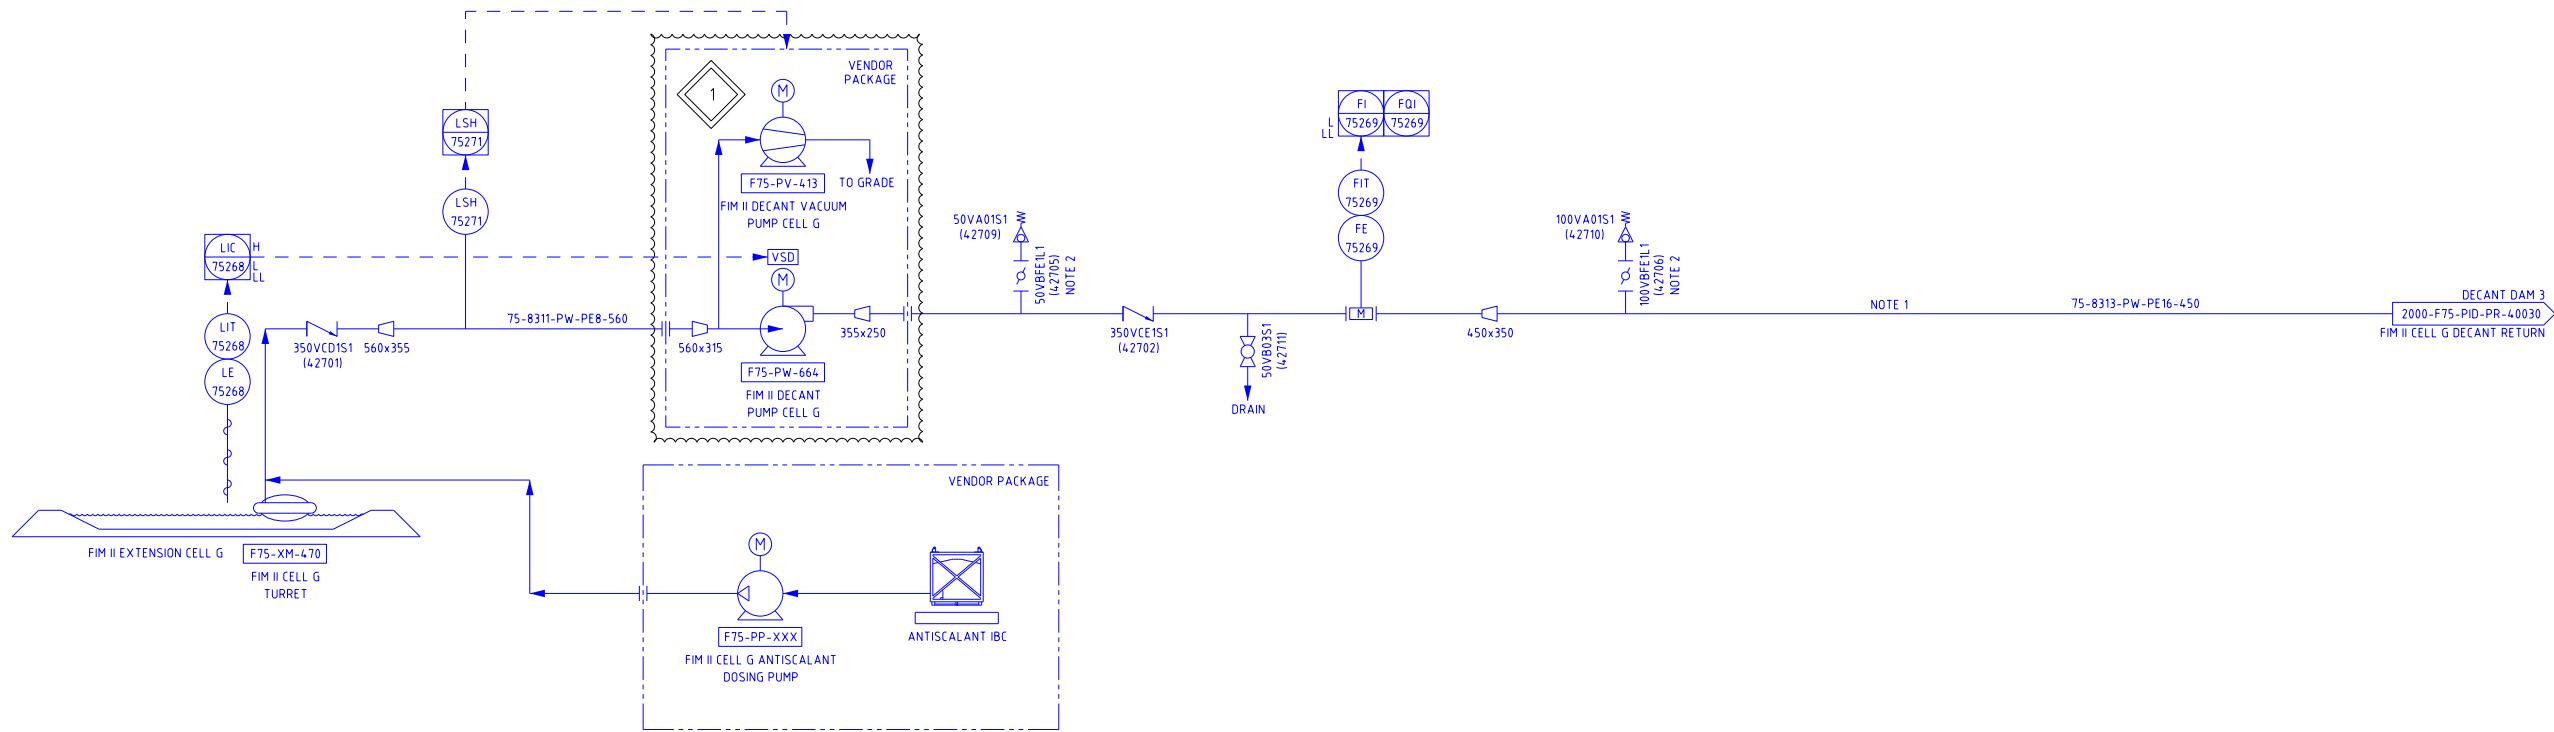

APPROVED FOR
CONSTRUCTION